

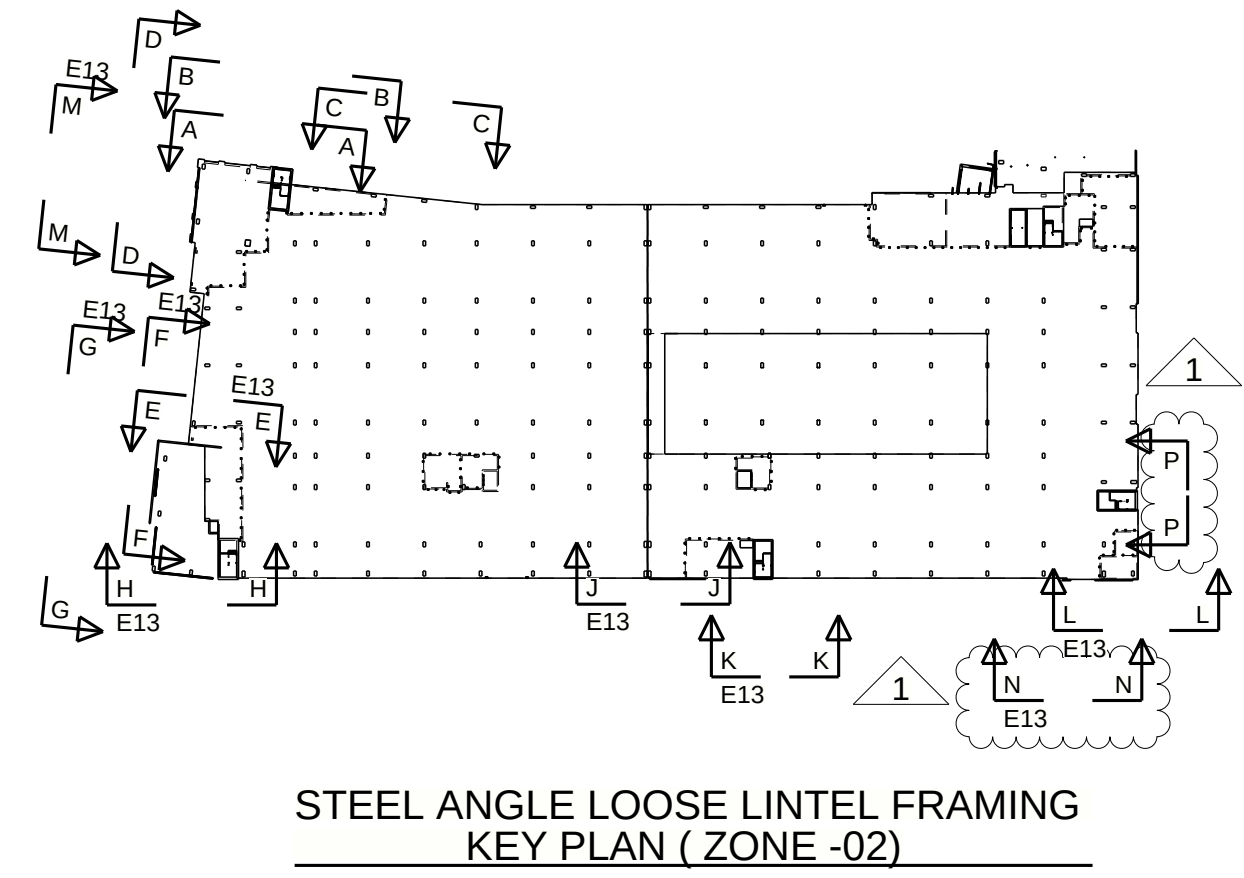


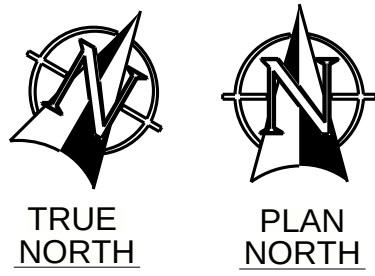

STEEL ANGLE LOOSE LINTEL FRAMING
KEY PLAN (ZONE -02)

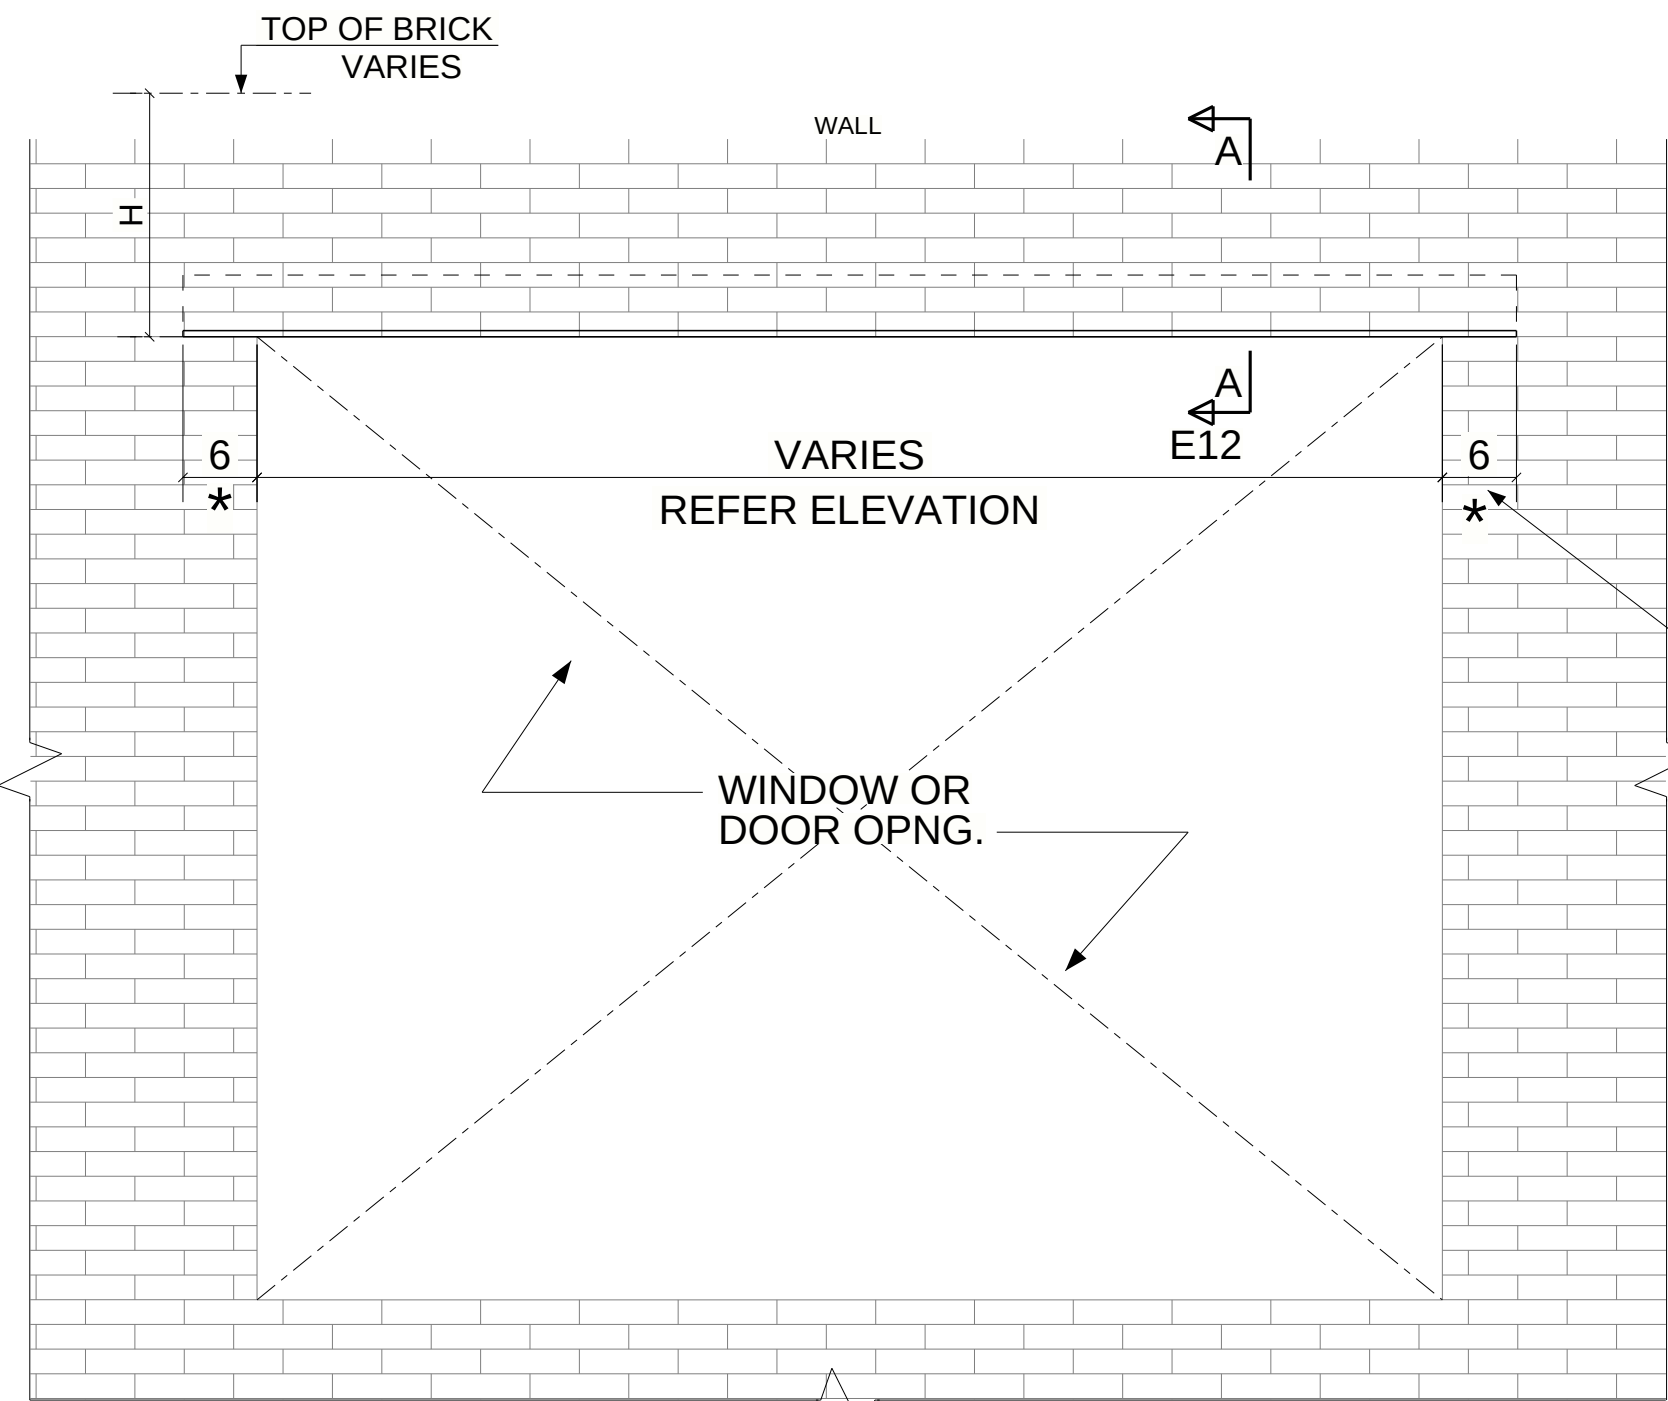

TYPICAL STEEL ANGLE BRICK LOOSE LINTEL ELEVATION DETAIL AT
WINDOWS, DOORS AND STORE FRONTS.
(REF: 12/S-421)

* NOTE:
BEARING WILL BE 7" FOR 12'-0
OPENING SPAN AND ABOVE
PER BRICK LOOSE LINTEL
SCHEDULE.

TYP.
MIN. BRG.


CMU
VENEER

BREAK METAL
WHERE REQ,D
STEEL ANGLE LOOSE
LINTEL (LLV) (MARK
REFER ELEVATION).


A - A

GENERAL NOTE:


- 1.U.N.O ALL WINDOW LOCATIONS NOTED PER ELEVATIONS ARE TO BE FIELD VERIFIED WITH STORE FRONT OR WINDOW LOCATION DRAWINGS AS THESE ARE MEASURED PER ARCH REFERENCE.
2. REFER TYPICAL STEEL ANGLE BRICK LOOSE LINTEL DETAIL FOR BEARING DETAILS U.N.O.
3. ALL STEEL LINTELS SHALL BE HOT DIP GALV.

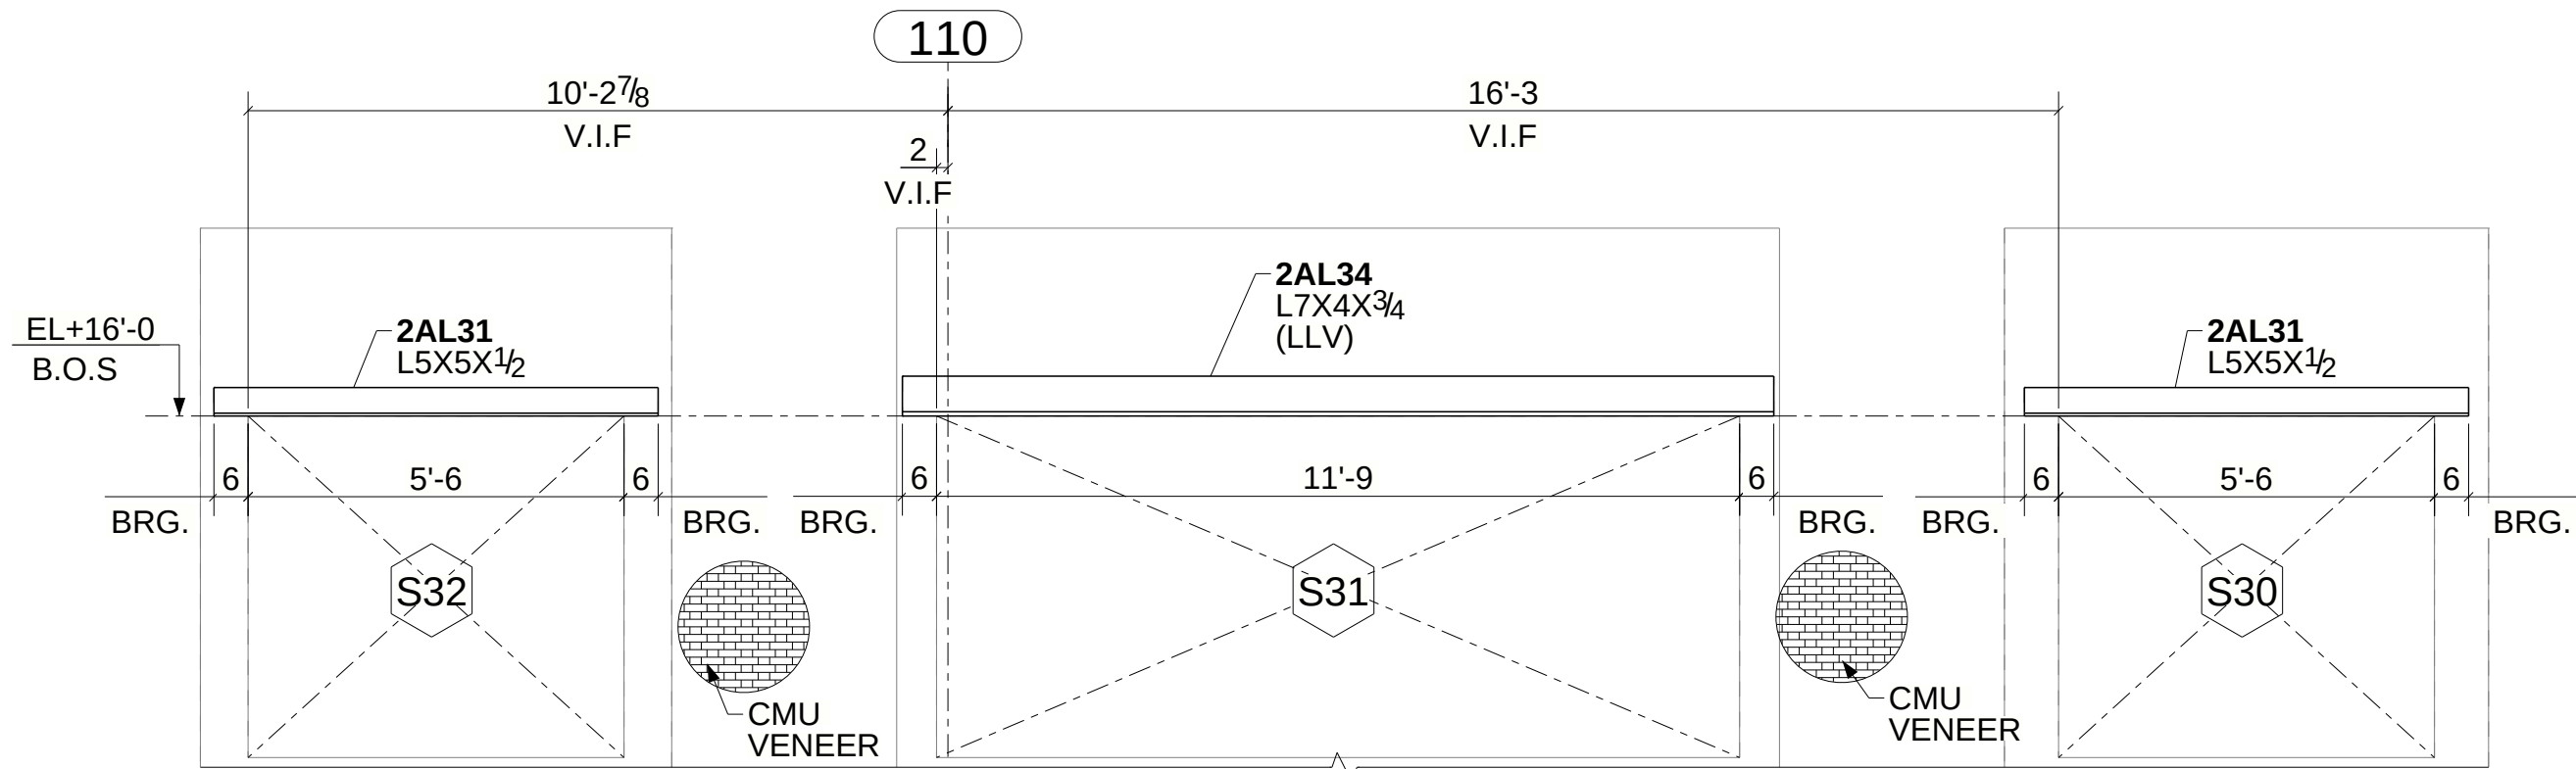


A - A
(REF:1/A-201) (NORTH ELEVATION)

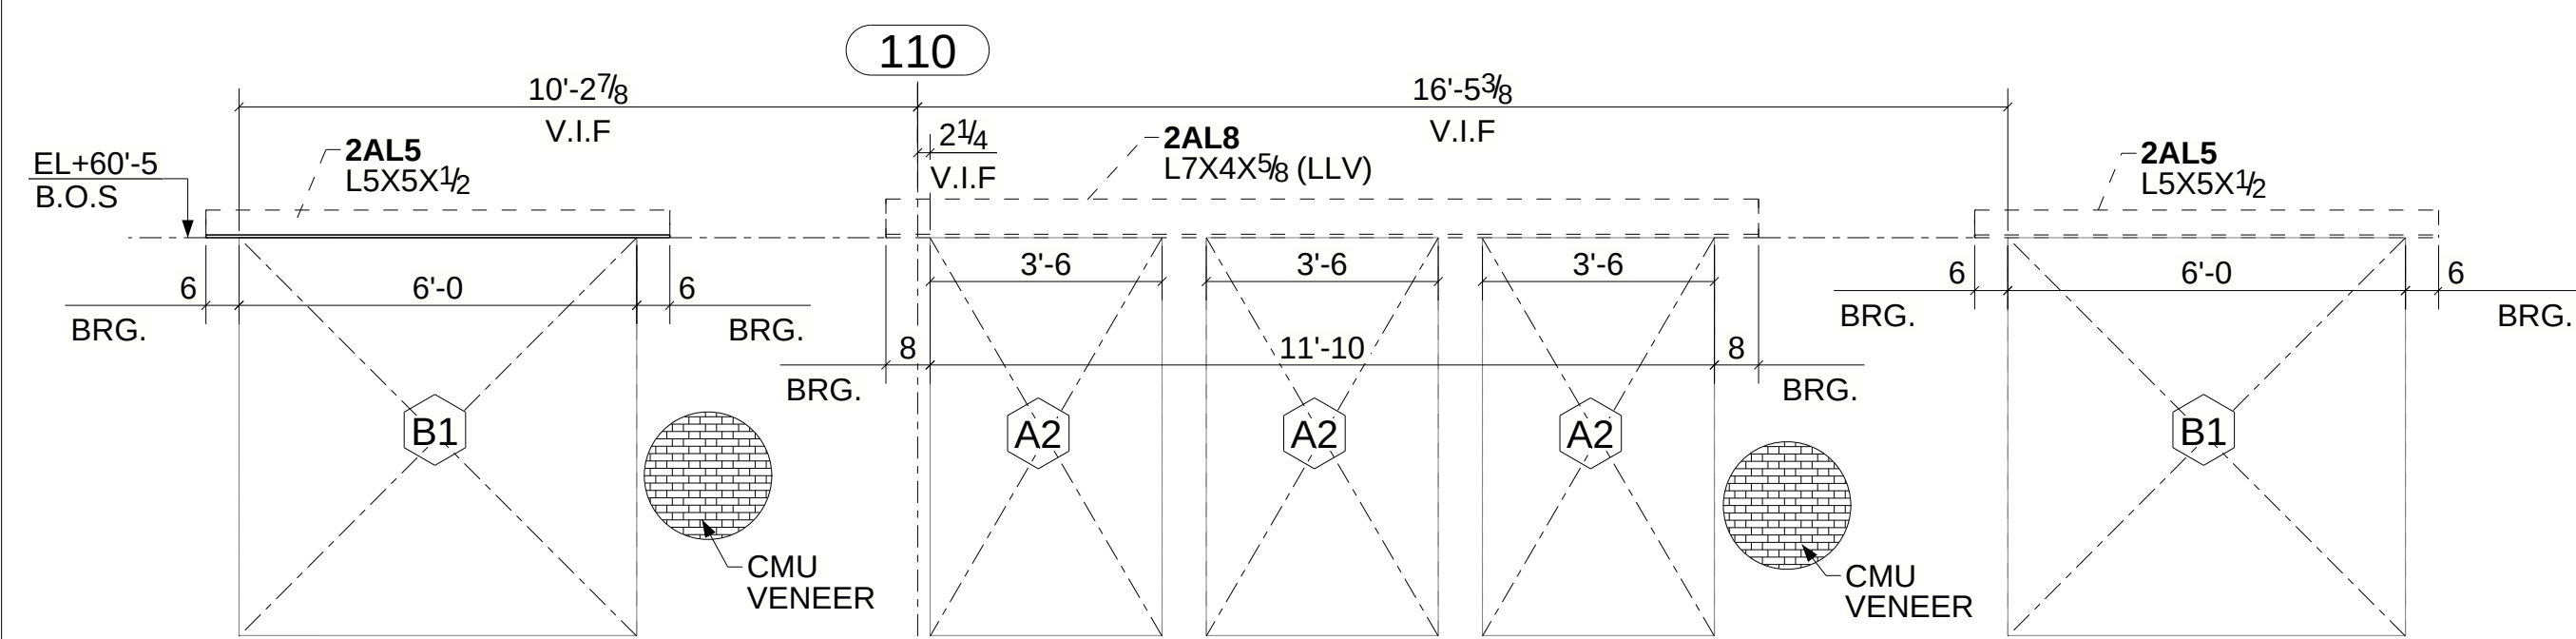


B - B
(REF:1/A-201) (NORTH ELEVATION)

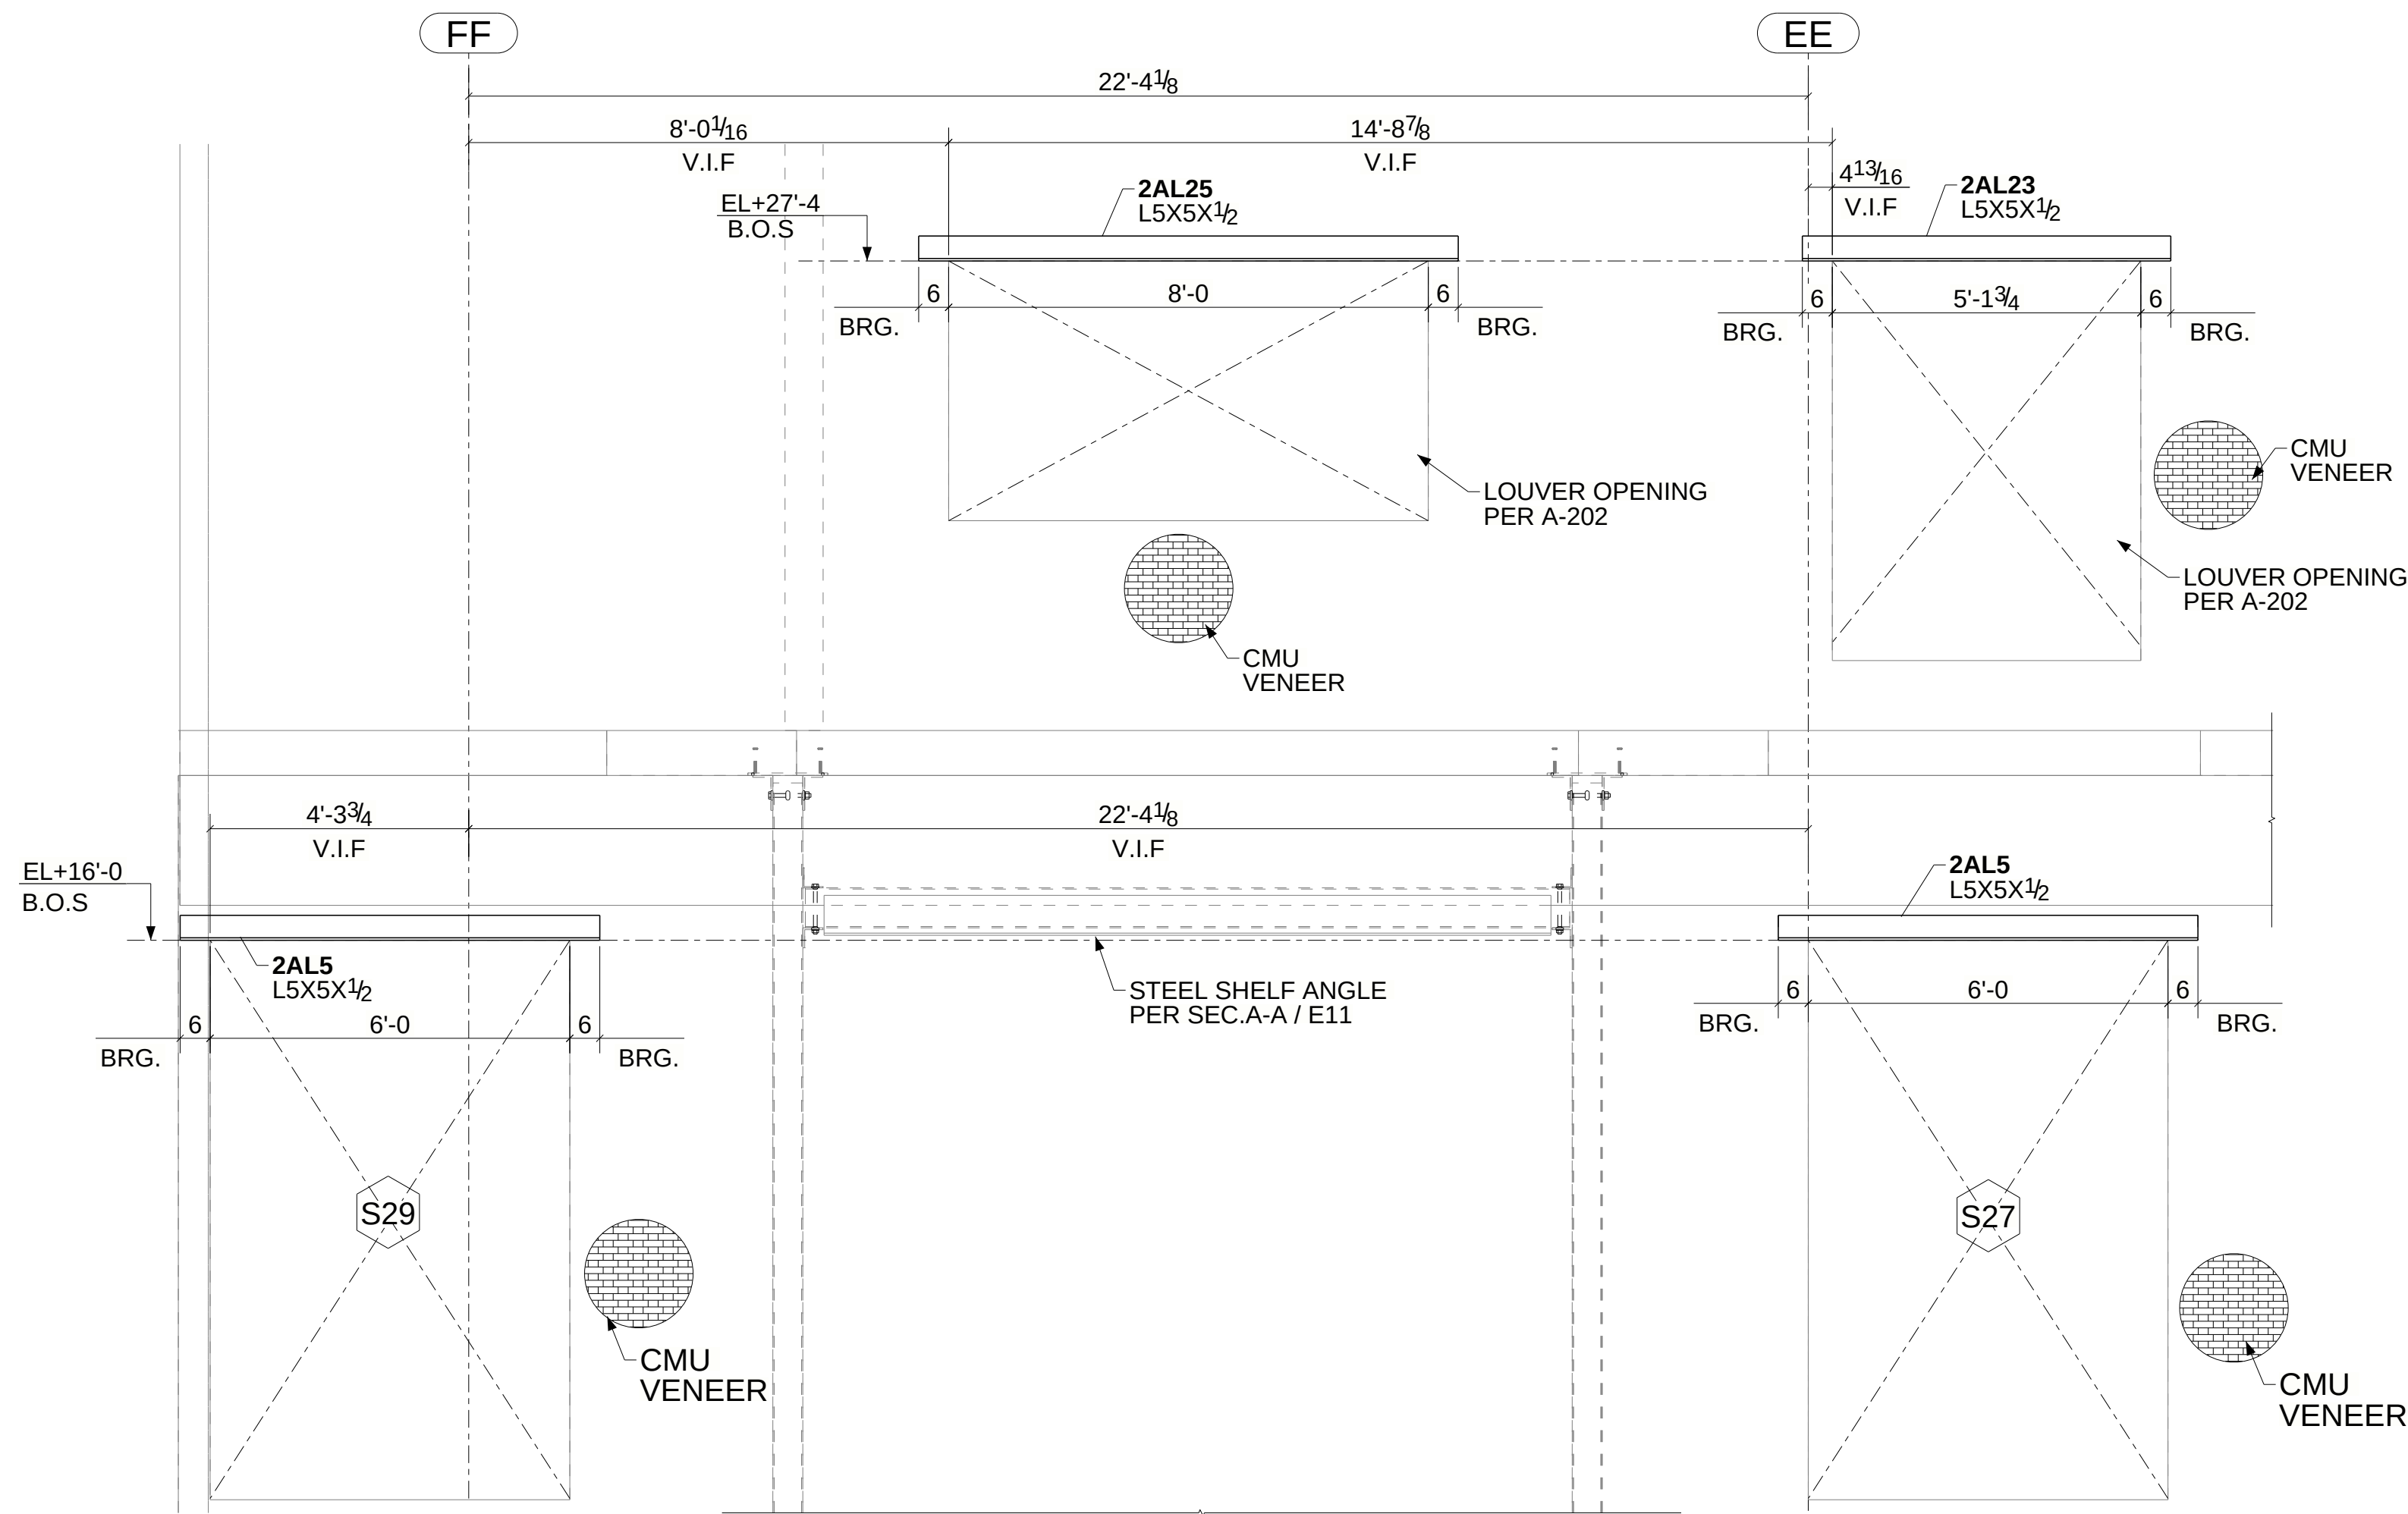

D - D
(REF:1/A-202) (WEST ELEVATION)

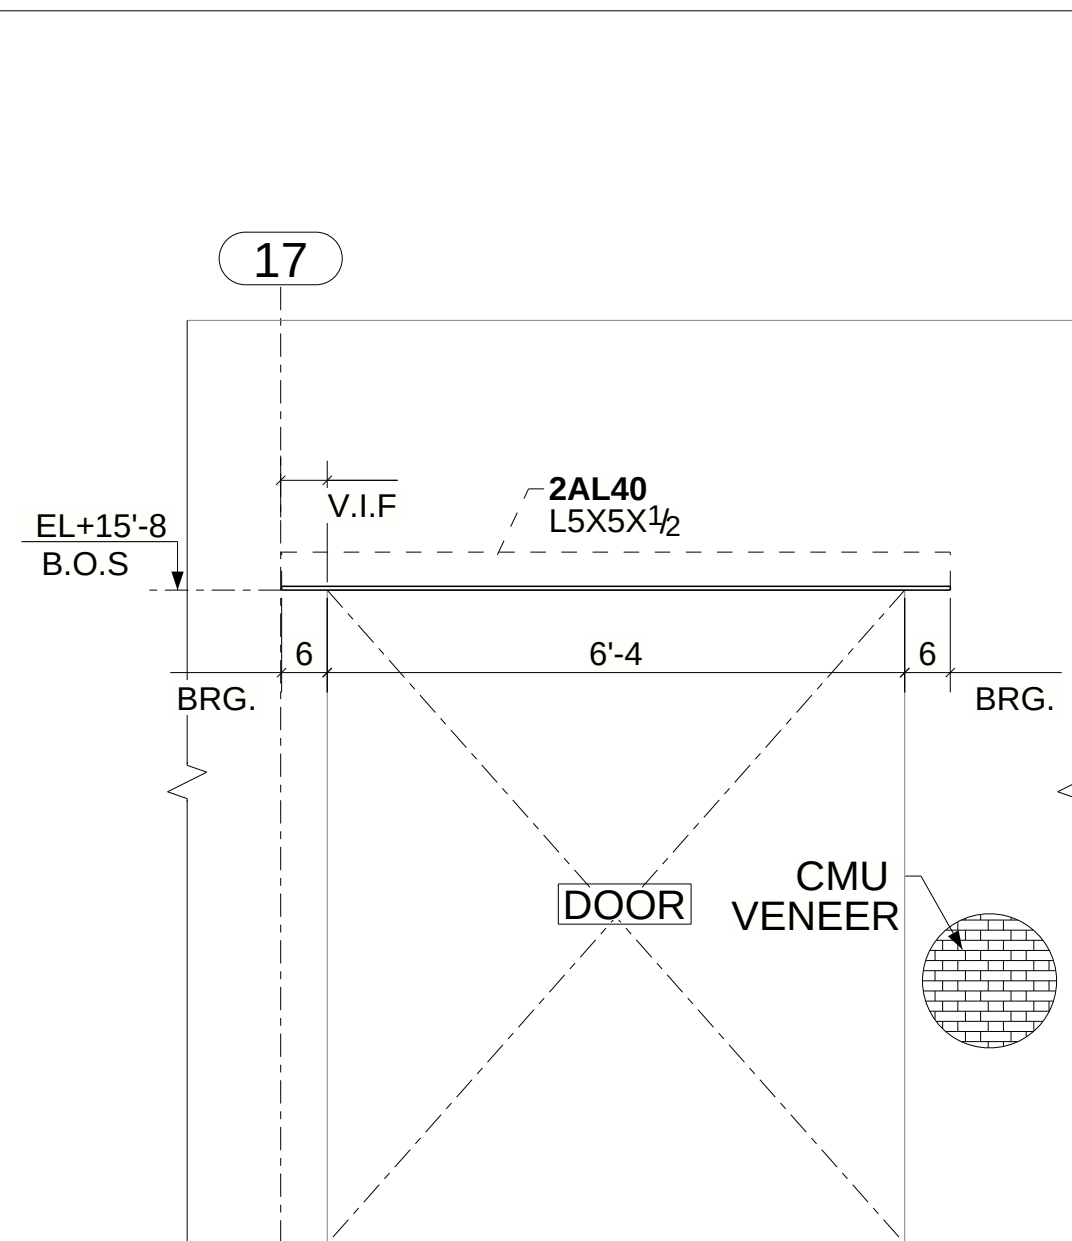

C - C
(REF:1/A-201) (NORTH ELEVATION)

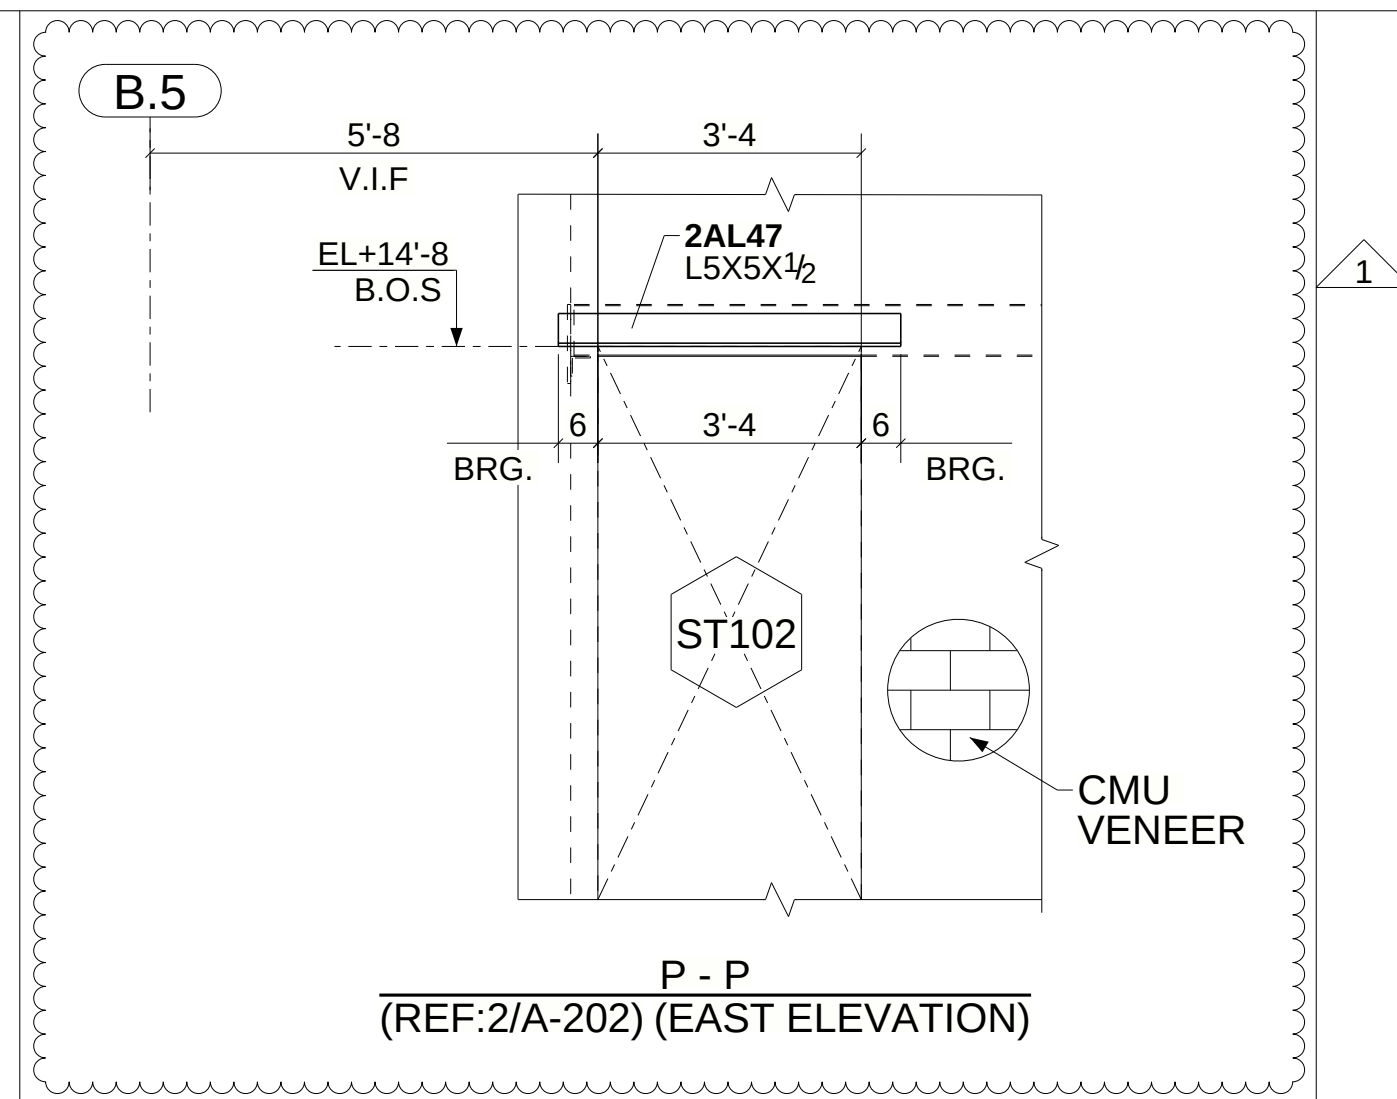

P - P
(REF:2/A-202) (EAST ELEVATION)

LEGEND:

- (X) - WINDOW / STORE FRONT TYPE.
- BRG - BEARING
- U.N.O - UNLESS NOTED OTHERWISE.
- V.I.F - VERIFY IN FIELD.

STEEL ANGLE SCHEDULE FOR MASONRY OPENING:

1. L5X5X5/16 FOR OPENING SPAN 3'-0.
2. L5X5X3/8 FOR OPENING SPAN 4'-0
3. L5X5X7/16 FOR OPENING SPAN 5'-0
4. L5X5X1/2 FOR OPENING SPAN 8'-0
5. L7X4X3/8 FOR OPENING SPAN 9'-0 W/ BRICK HEIGHT "H" < 2'-6".
6. L7X4X5/8 FOR OPENING SPAN 9'-0 W/ BRICK HEIGHT "H" < 11'-0".
7. L7X4X7/16 FOR OPENING SPAN 12'-0 W/ BRICK HEIGHT "H" < 2'-6".
8. L7X4X5/8 FOR OPENING SPAN 12'-0 W/ BRICK HEIGHT "H" < 10'-0".
9. L7X4X3/4 FOR OPENING SPAN 12'-0 W/ BRICK HEIGHT "H" < 12'-0".

**Building
Envelope
Systems**



20 HIGH STREET
PLAINSVILLE, MA 02762
PHONE (508) 381-0429
www.teambes.com

PROJECT NAME
GSC JUNIPER RBP PHASE-II

LOCATION
PARKWAY EVERETT, MA

CONTRACTOR

BUILDING ENVELOPE SYSTEMS

DWG TITLE

LOOSE LINTEL FRAMING PLAN (ZONE-2)

DRAWN BY

DRK

CHECKED BY

HSR

DATE DRAWN

06/26/2025

PLOT DATE

06/26/2025

DGSTS No.

--

REV.

1

CONTRACT No.24050

DWG No. E12

1 06/26/2025 Revised As Noted

0 04/18/2025 For Construction

A 10/16/2024 For Approval

REV. DATE DESCRIPTION