


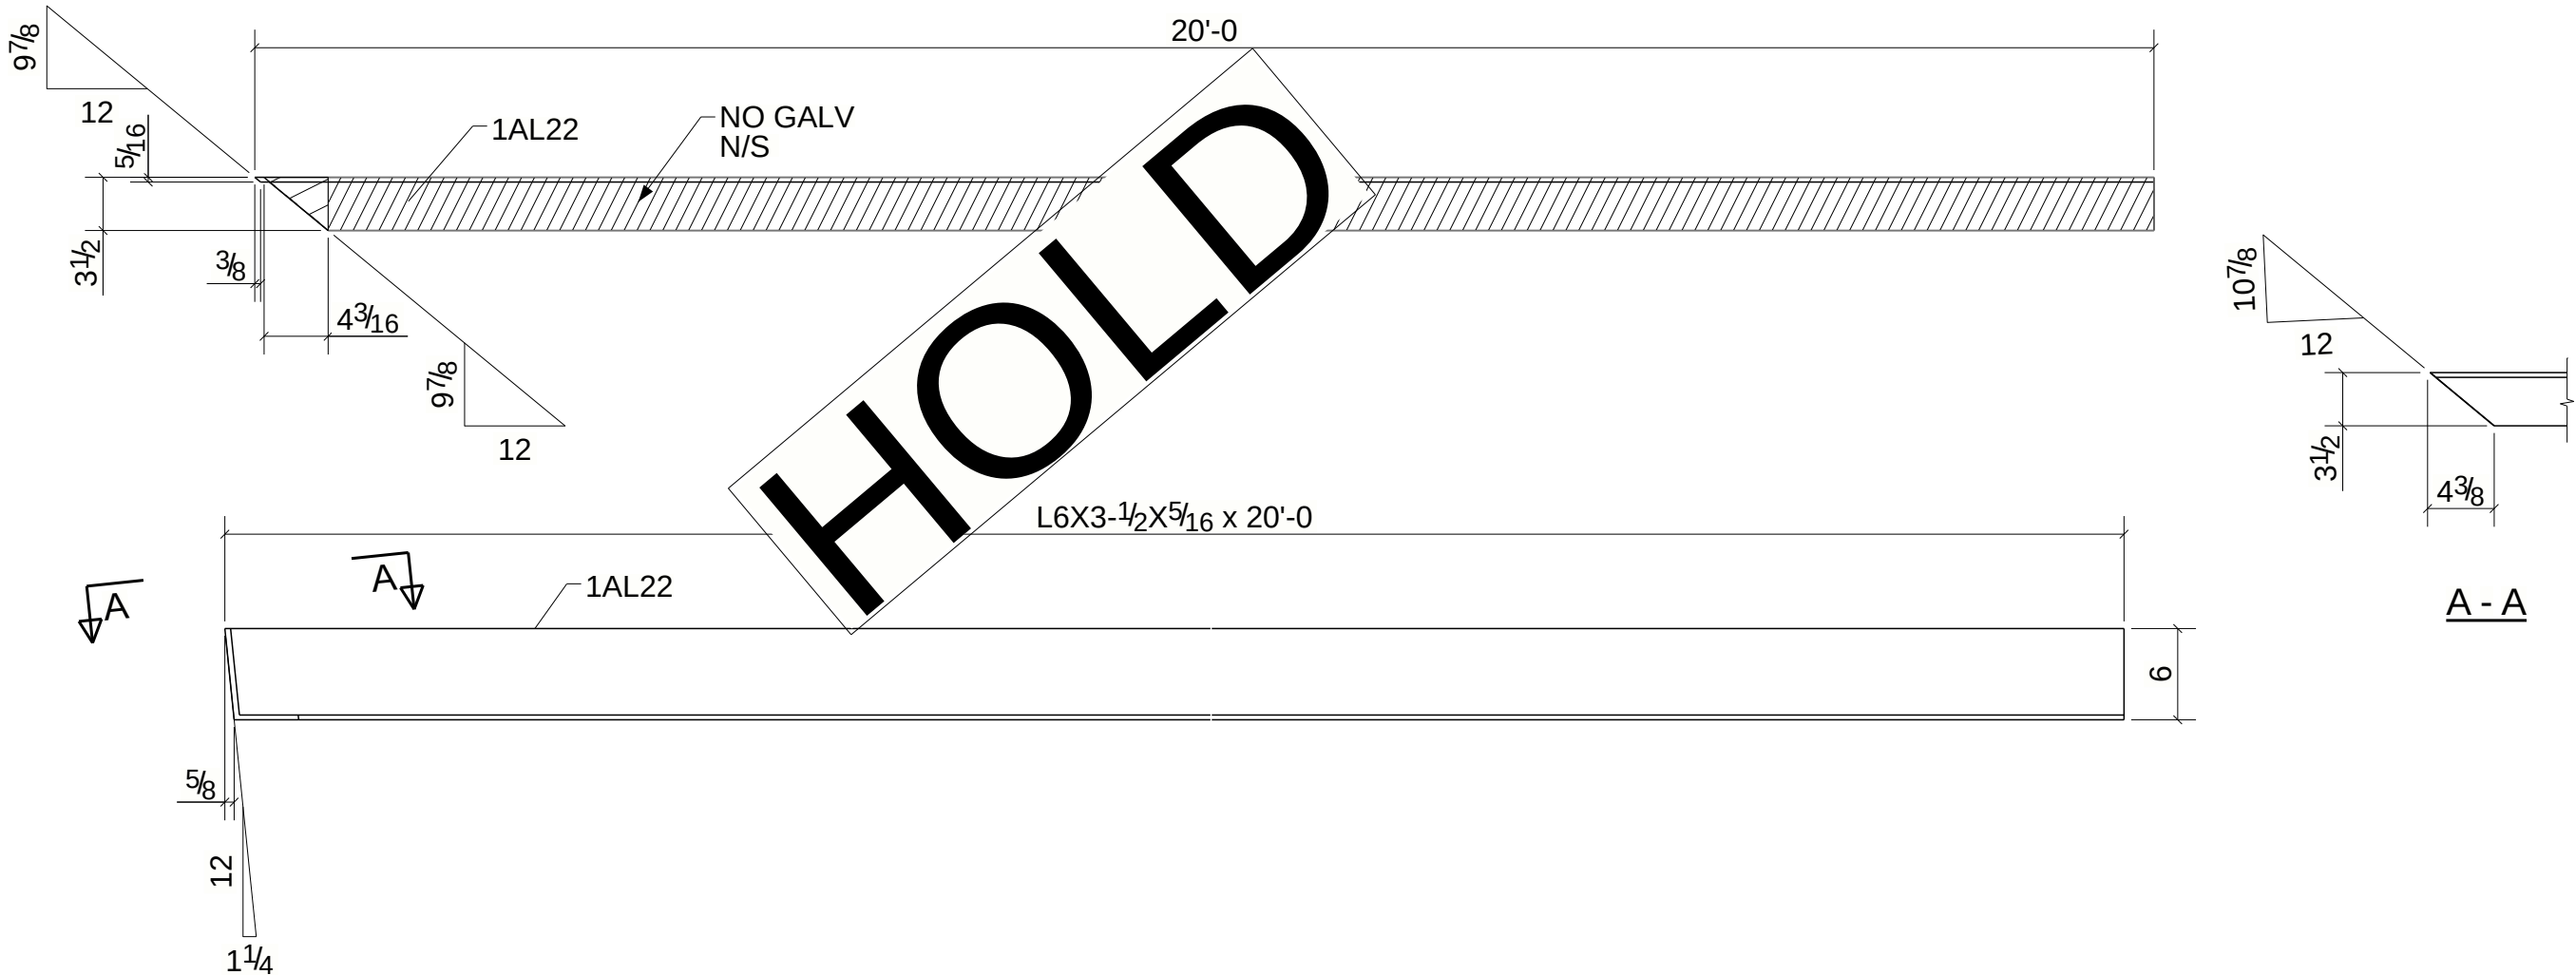

FABRICATOR NOTE:
NO GALV. & MASK HATCHED PORTION WITH TWO PART OF EPOXY BEFORE GALVANIZATION.

ONE - CLOSURE ANGLE - 1AL22

BILL OF MATERIAL

MARK	TOTAL QTY	SHAPE	LENGTH	TOTAL WEIGHT	REMARKS	ADV MILL #	STEEL GRADE
1AL22	1	L6X3-1/2X5/16	20'-0"	197	SQ-1/BEV-1 GALV		A36

0	04/11/2025	For Fabrication	Building Envelope Systems 20 HIGH STREET PLAINSVILLE, MA 02762 PHONE (508) 381-0429 www.teambes.com PROJECT NAME GSC JUNIPER RBP PHASE-II LOCATION PARKWAY EVERETT, MA CONTRACTOR BUILDING ENVELOPE SYSTEMS DWG TITLE ANGLE DRAWN BY ABJ CHECKED BY HSR DATE DRAWN 03/24/2025 PLOT DATE 03/24/2025 DGSTS No. --					
A	03/24/2025	For Approval						
REV.	DATE	DESCRIPTION						
MATERIAL A36 UNO								
HOLES 13/16Ø UNO								
WELDS E70XX								
SURFACE PREP. SSPC SP3								
PAINT NOTE : GALVANIZED			CONTRACT No. 24050			DWG No. 1AL22		REV. 0