


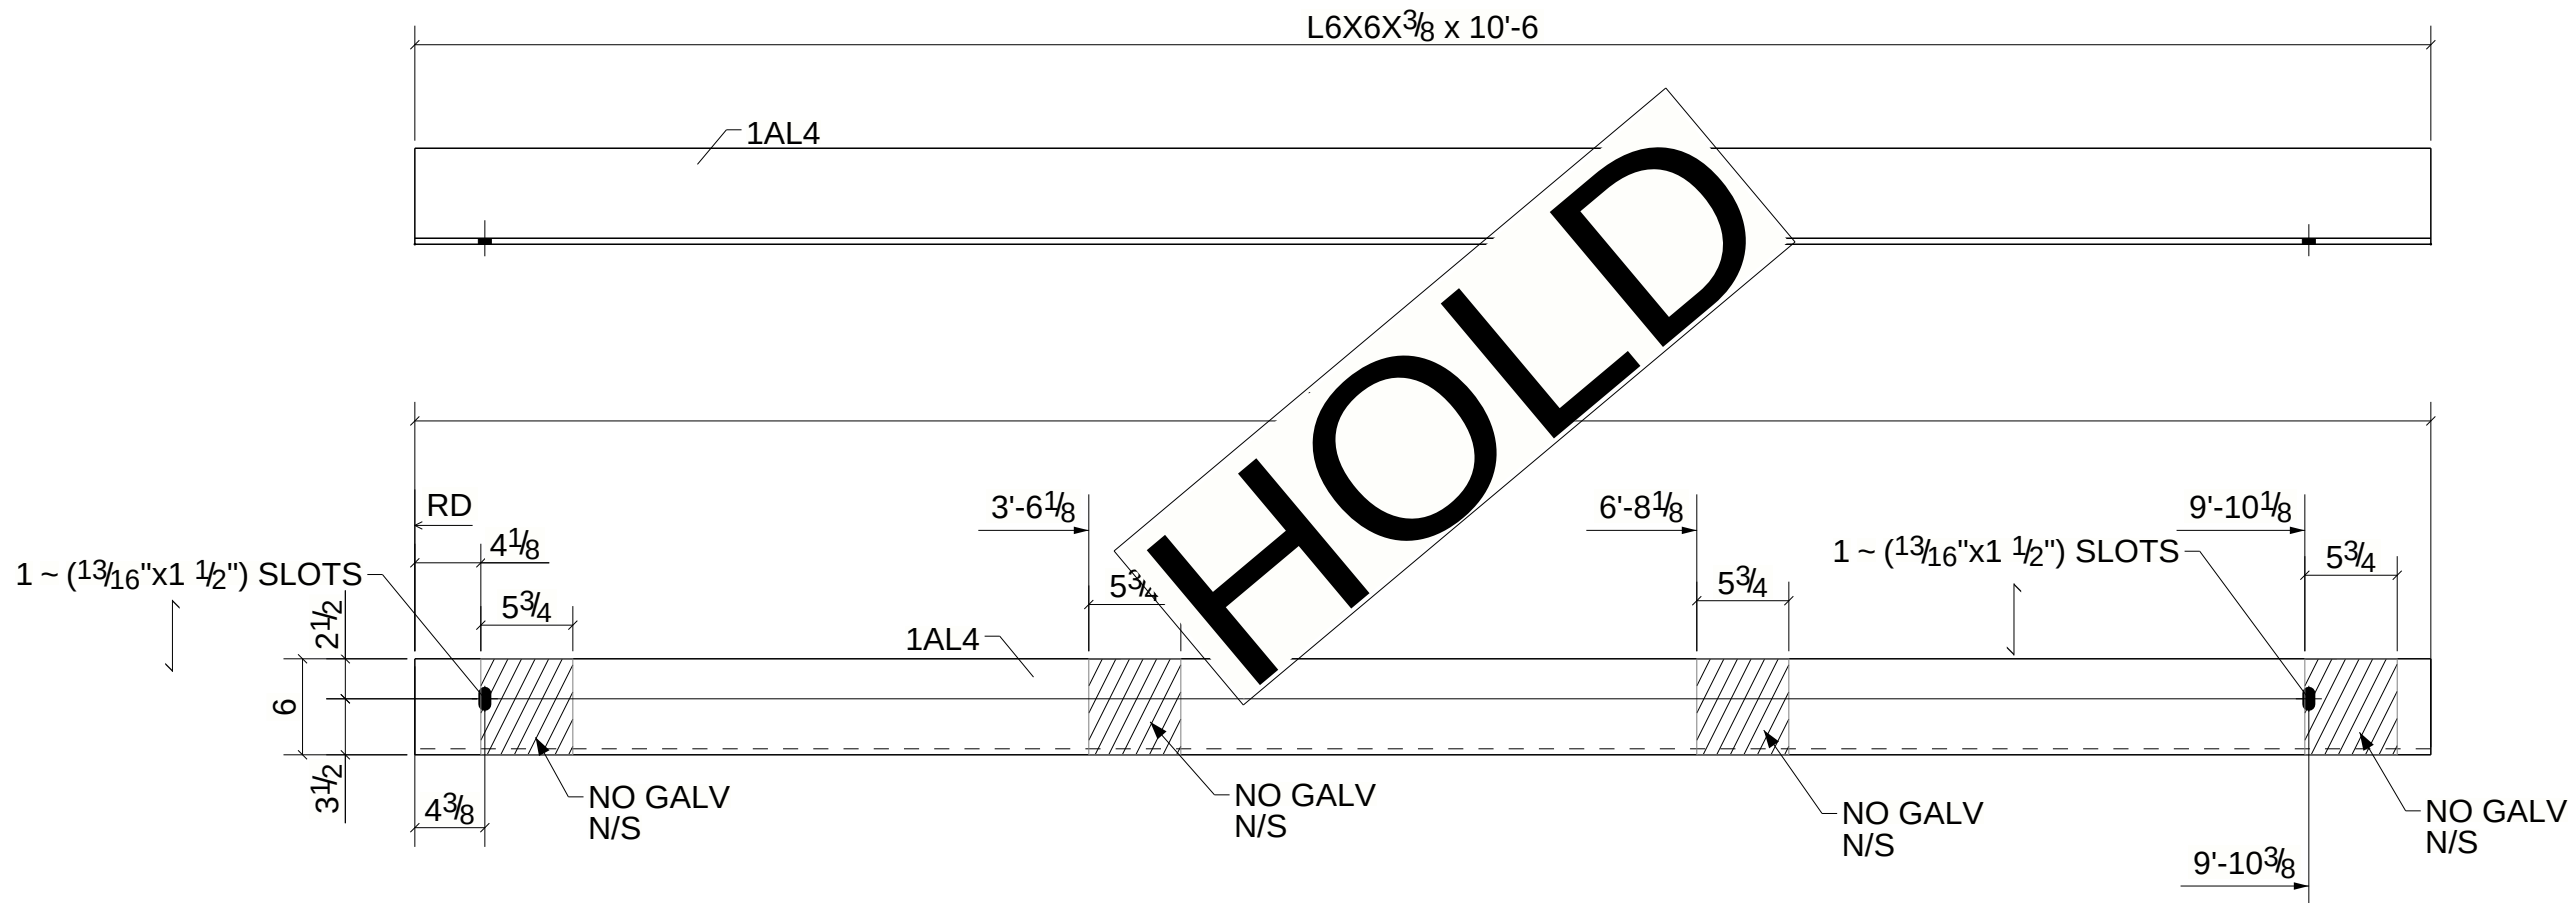

FABRICATOR NOTE:

NO GALV. & MASK HATCHED PORTION WITH TWO PART OF EPOXY BEFORE GALVANIZATION.

ONE - LINTEL ANGLE - 1AL4

BILL OF MATERIAL

MARK	TOTAL QTY	SHAPE	LENGTH	TOTAL WEIGHT	REMARKS	ADV MILL #	STEEL GRADE
1AL4	1	L6X6X3/8	10'-6"	157	SQ-2 GALV		A36

0	04/11/2025	For Fabrication
A	03/24/2025	For Approval
REV.	DATE	DESCRIPTION
MATERIAL A36 UNO		
HOLES 13/16Ø UNO		
WELDS E70XX		
SURFACE PREP. SSPC SP3		
PAINT NOTE : GALVANIZED		

Building Envelope Systems 		20 HIGH STREET PLAINSVILLE, MA 02762 PHONE (508) 381-0429 www.teambes.com	
PROJECT NAME GSC JUNIPER RBP PHASE-II			
LOCATION PARKWAY EVERETT, MA			
CONTRACTOR BUILDING ENVELOPE SYSTEMS			
DWG TITLE LINTEL ANGLE			
DRAWN BY ABJ	CHECKED BY HSR	DATE DRAWN 03/24/2025	PLOT DATE 03/24/2025
CONTRACT No. 24050		DWG No. 1AL4	DGSTS No. -- REV. 0