


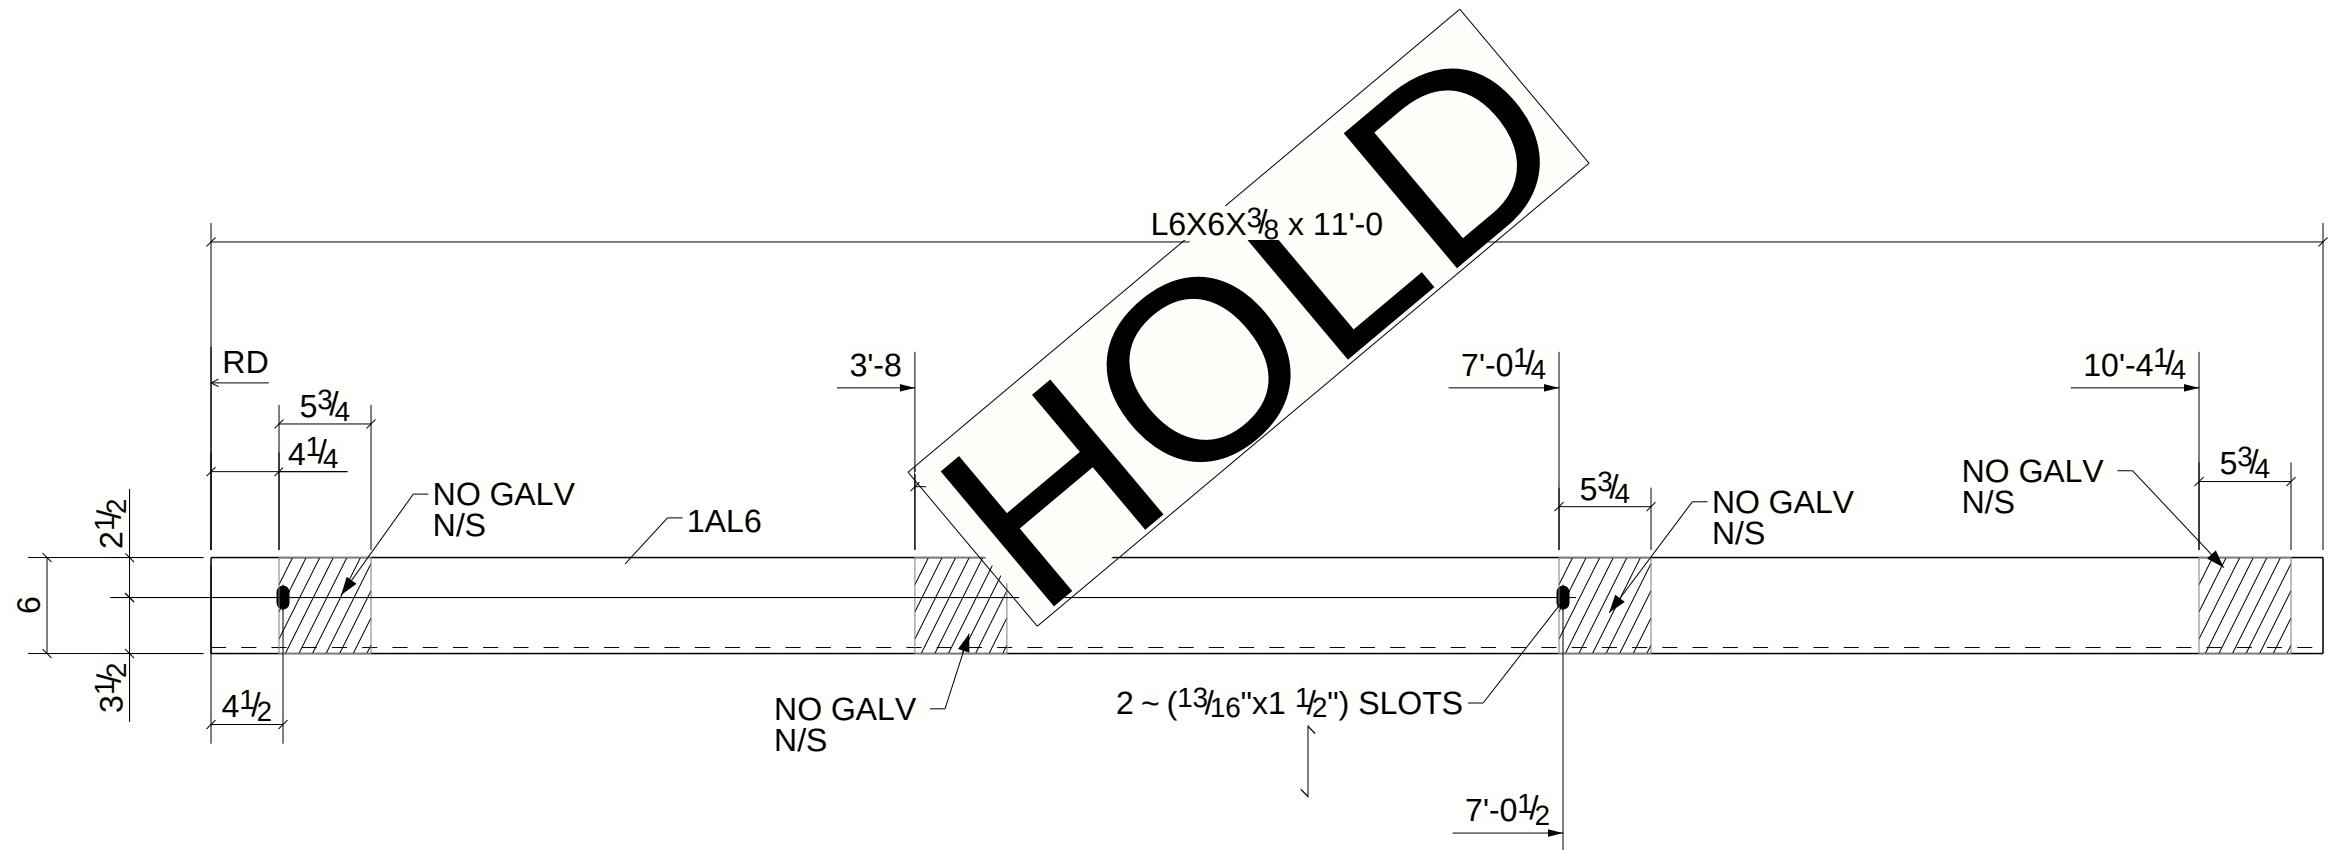

FABRICATOR NOTE:
NO GALV. & MASK HATCHED PORTION WITH TWO PART OF EPOXY BEFORE GALVANIZATION.

ONE - LINTEL ANGLE - 1AL6

BILL OF MATERIAL

MARK	TOTAL QTY	SHAPE	LENGTH	TOTAL WEIGHT	REMARKS	ADV MILL #	STEEL GRADE
1AL6	1	L6X6X3/8	11'-0"	164	SQ-2 GALV		A36

0	04/11/2025	For Fabrication	PROJECT NAME GSC JUNIPER RBP PHASE-II				
A	03/24/2025	For Approval					
REV.	DATE	DESCRIPTION					
MATERIAL A36 UNO			LOCATION PARKWAY EVERETT, MA				
HOLES 13/16Ø UNO			CONTRACTOR BUILDING ENVELOPE SYSTEMS				
WELDS E70XX			DWG TITLE LINTEL ANGLE				
SURFACE PREP. SSPC SP3			DRAWN BY ABJ	CHECKED BY HSR	DATE DRAWN 03/24/2025	PLOT DATE 03/24/2025	DGSTS No. --
PAINT NOTE : GALVANIZED			CONTRACT No. 24050		DWG No. 1AL6		REV. 0



20 HIGH STREET
PLAINSVILLE, MA 02762
PHONE (508) 381-0429
www.teambes.com