


Tekla Structures

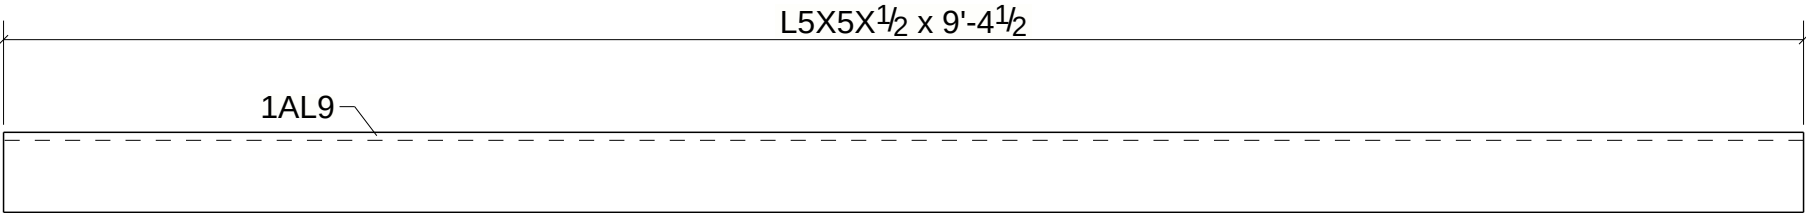

ONE - LINTEL ANGLE - 1AL9

BILL OF MATERIAL

MARK	TOTAL QTY	SHAPE	LENGTH	TOTAL WEIGHT	REMARKS	ADV MILL #	STEEL GRADE
1AL9	1	L5X5X1/2	9'-4 1/2"	153	SQ-2 GALV		A36

0	04/11/2025	For Fabrication	PROJECT NAME				
REV.	DATE	DESCRIPTION	GSC JUNIPER RBP PHASE-II				
MATERIAL A36 UNO			LOCATION PARKWAY EVERETT, MA				
HOLES 13/16Ø UNO			CONTRACTOR BUILDING ENVELOPE SYSTEMS				
WELDS E70XX			DWG TITLE LINTEL ANGLE				
SURFACE PREP. SSPC-SP3			DRAWN BY ABJ	CHECKED BY HSR	DATE DRAWN 10/16/2024	PLOT DATE 10/16/2024	DGSTS No. --
PAINT NOTE : GALV			CONTRACT No. 24050		DWG No. 1AL9		REV. 0



20 HIGH STREET
PLAINSVILLE, MA 02762
PHONE (508) 381-0429
www.teambes.com