

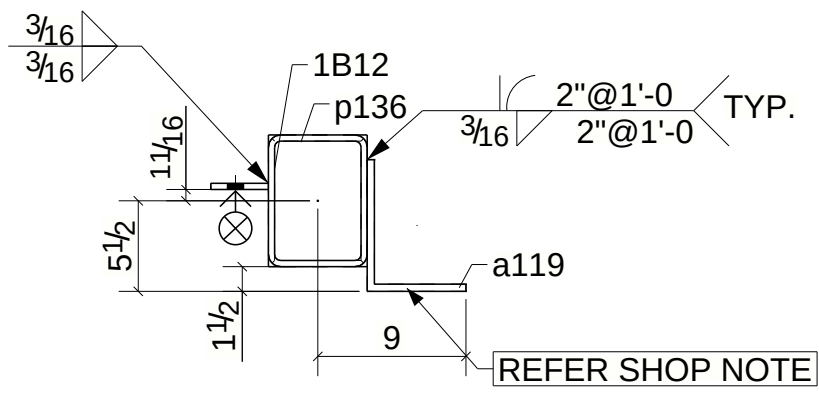
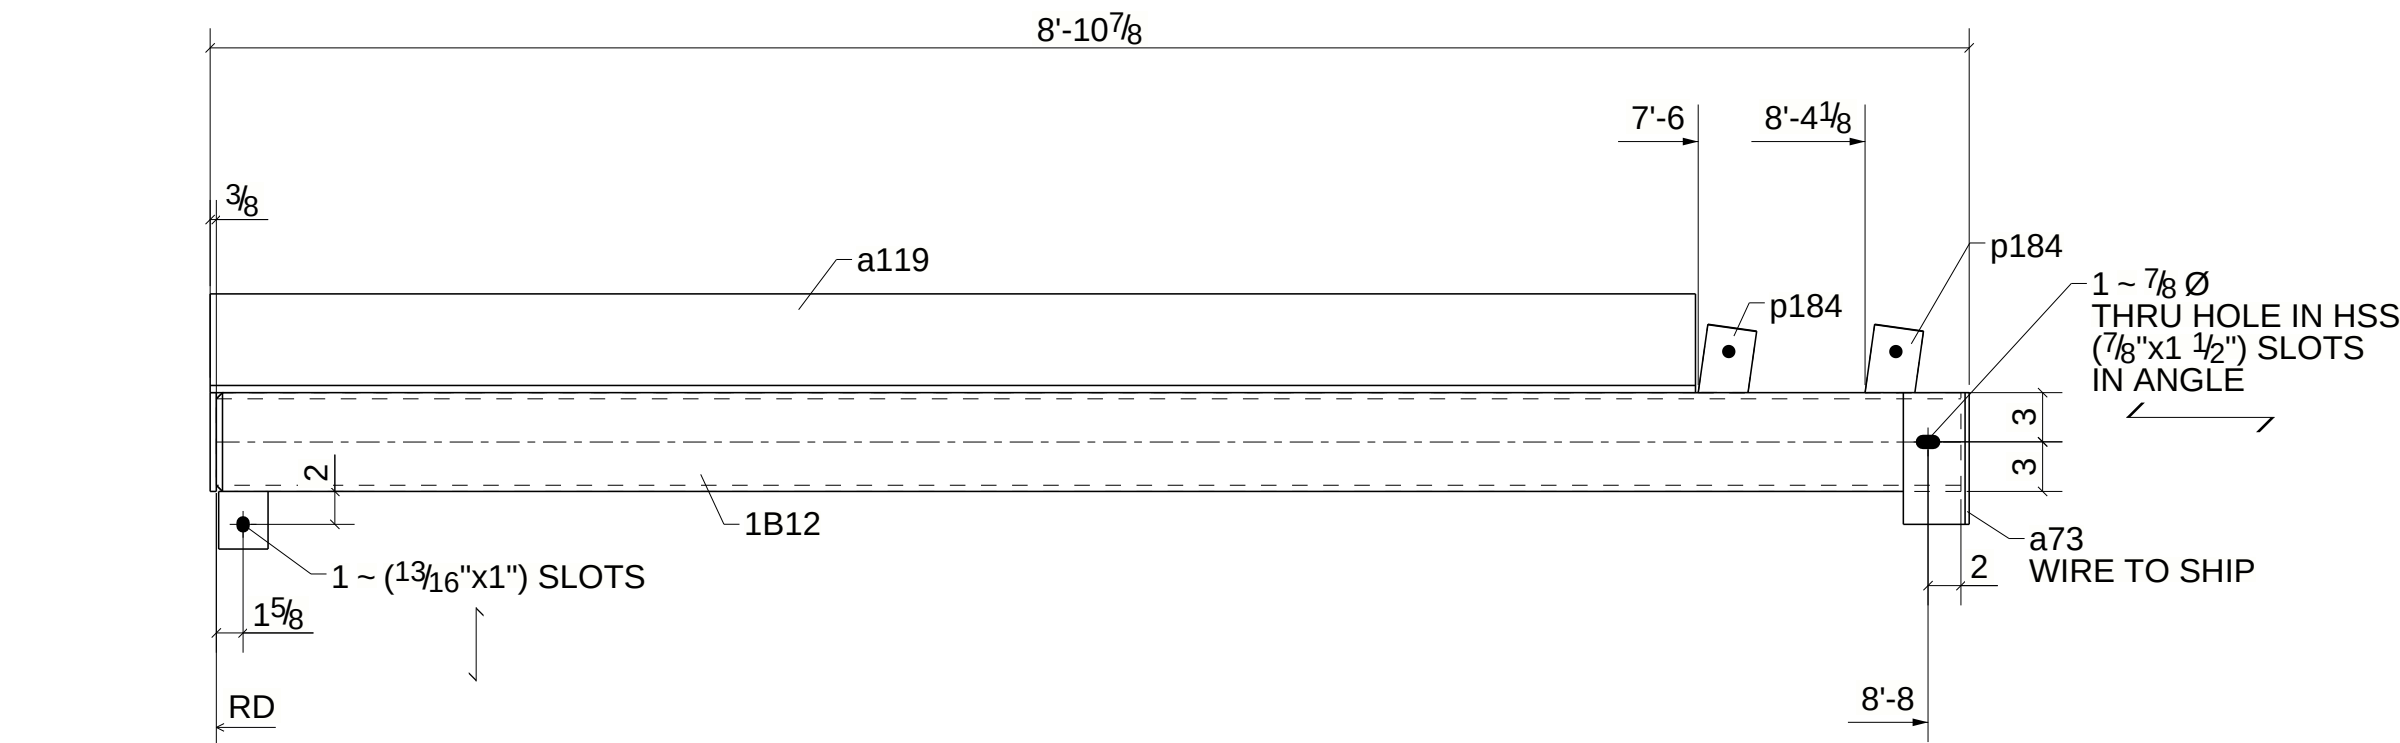
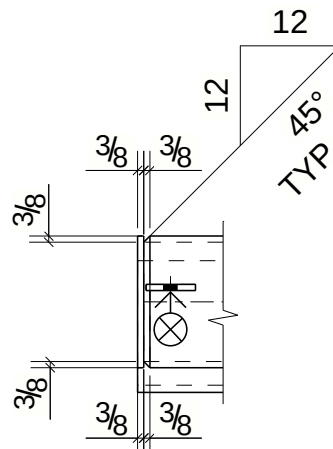
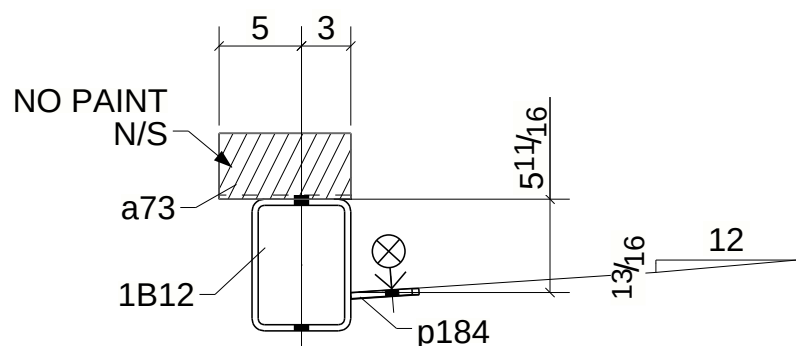



BILL OF MATERIAL							
MARK	TOTAL QTY	SHAPE	LENGTH	TOTAL WEIGHT	REMARKS	ADV MILL #	STEEL GRADE
1B12	1	HSS8X6X3/8	8'-10"	270	SQ-2		A500-GR B
a73	1	L4X4X1/4	0'-8"	4			A36
a119	1	L8X6X7/16	7'-6 1/4"	153	GALV.		A36
p43	1	PL3/8"X3"	0'-3 1/2"	1			A36
p136	1	PL3/8"X6"	0'-8"	5			A36
p184	2	PL3/8"X3"	0'-4 3/16"	3			A36

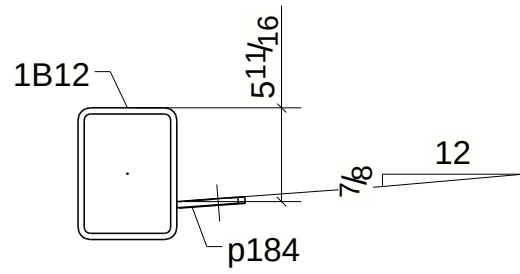

A - A

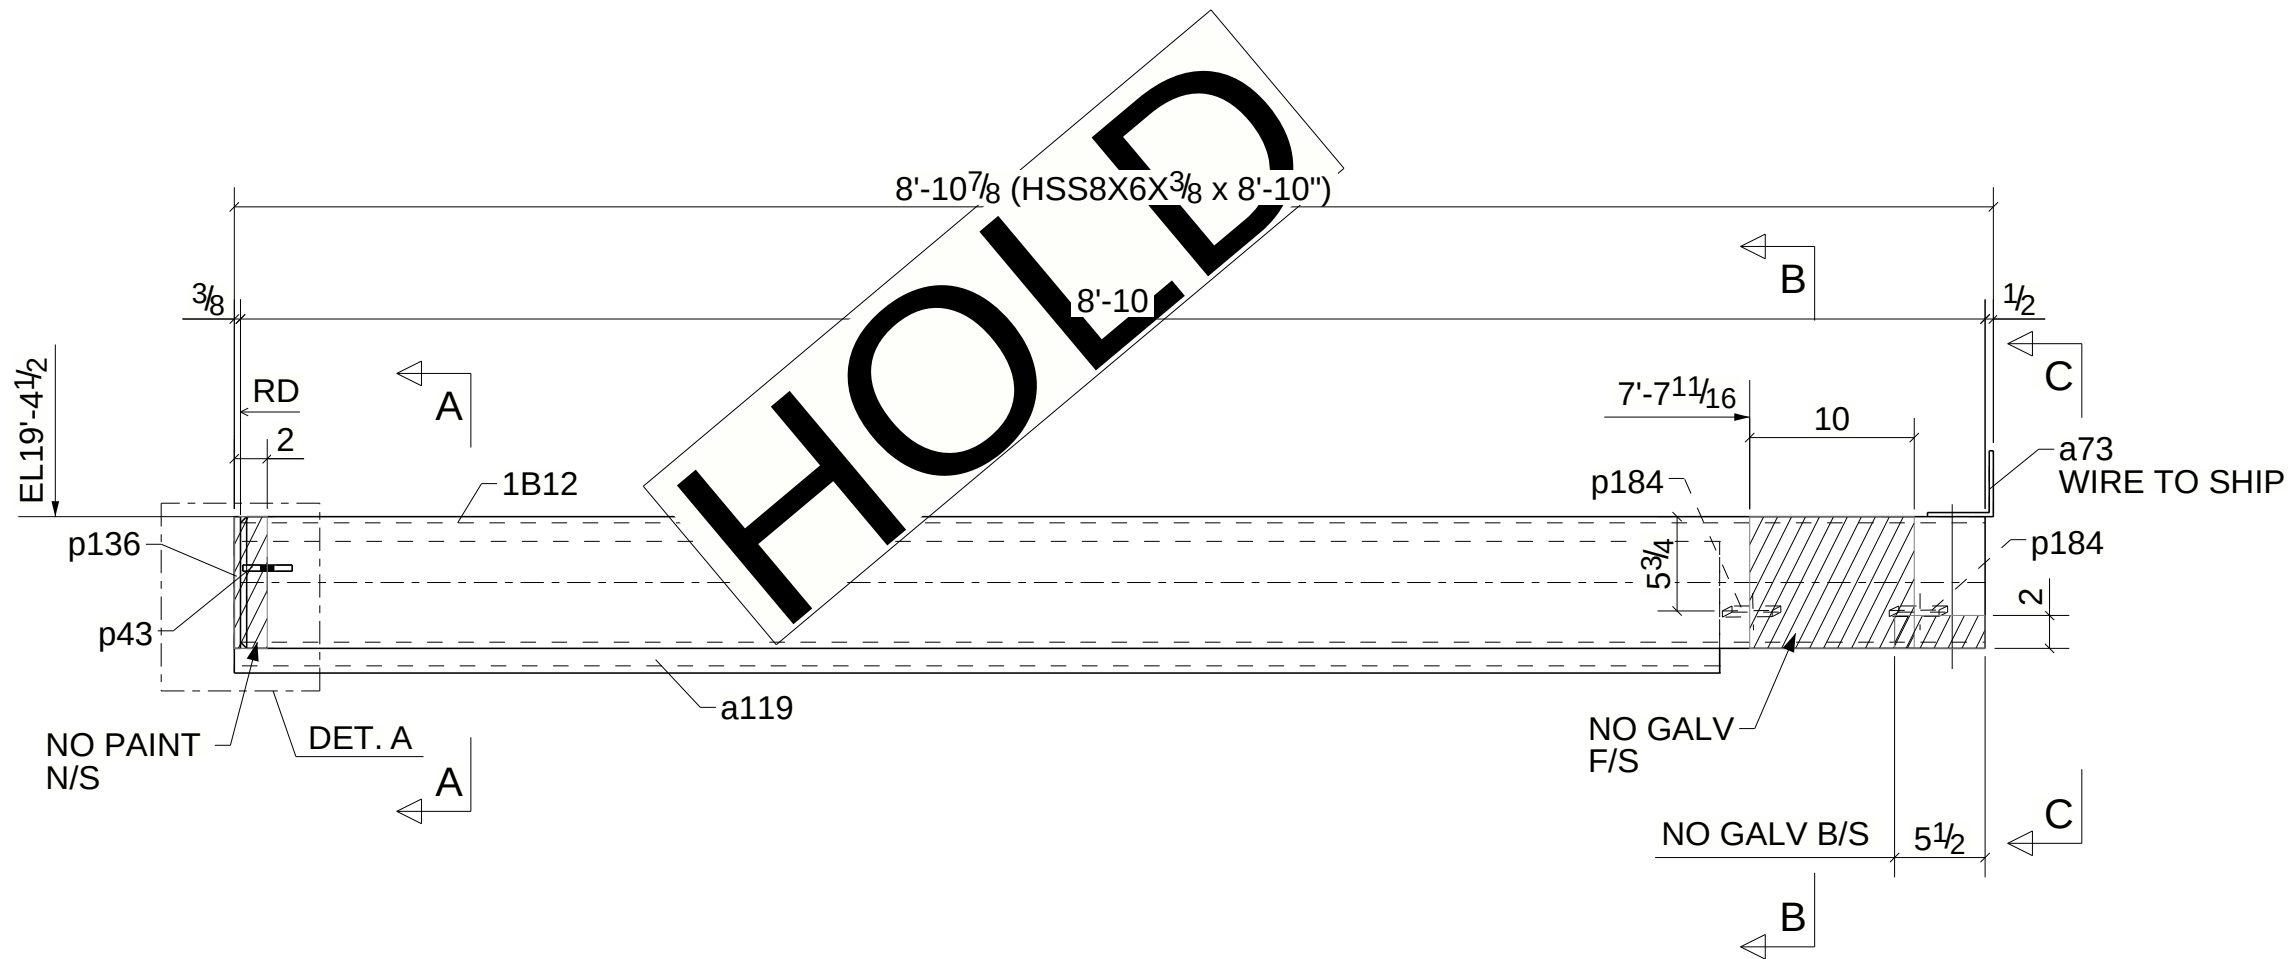

DETAIL A

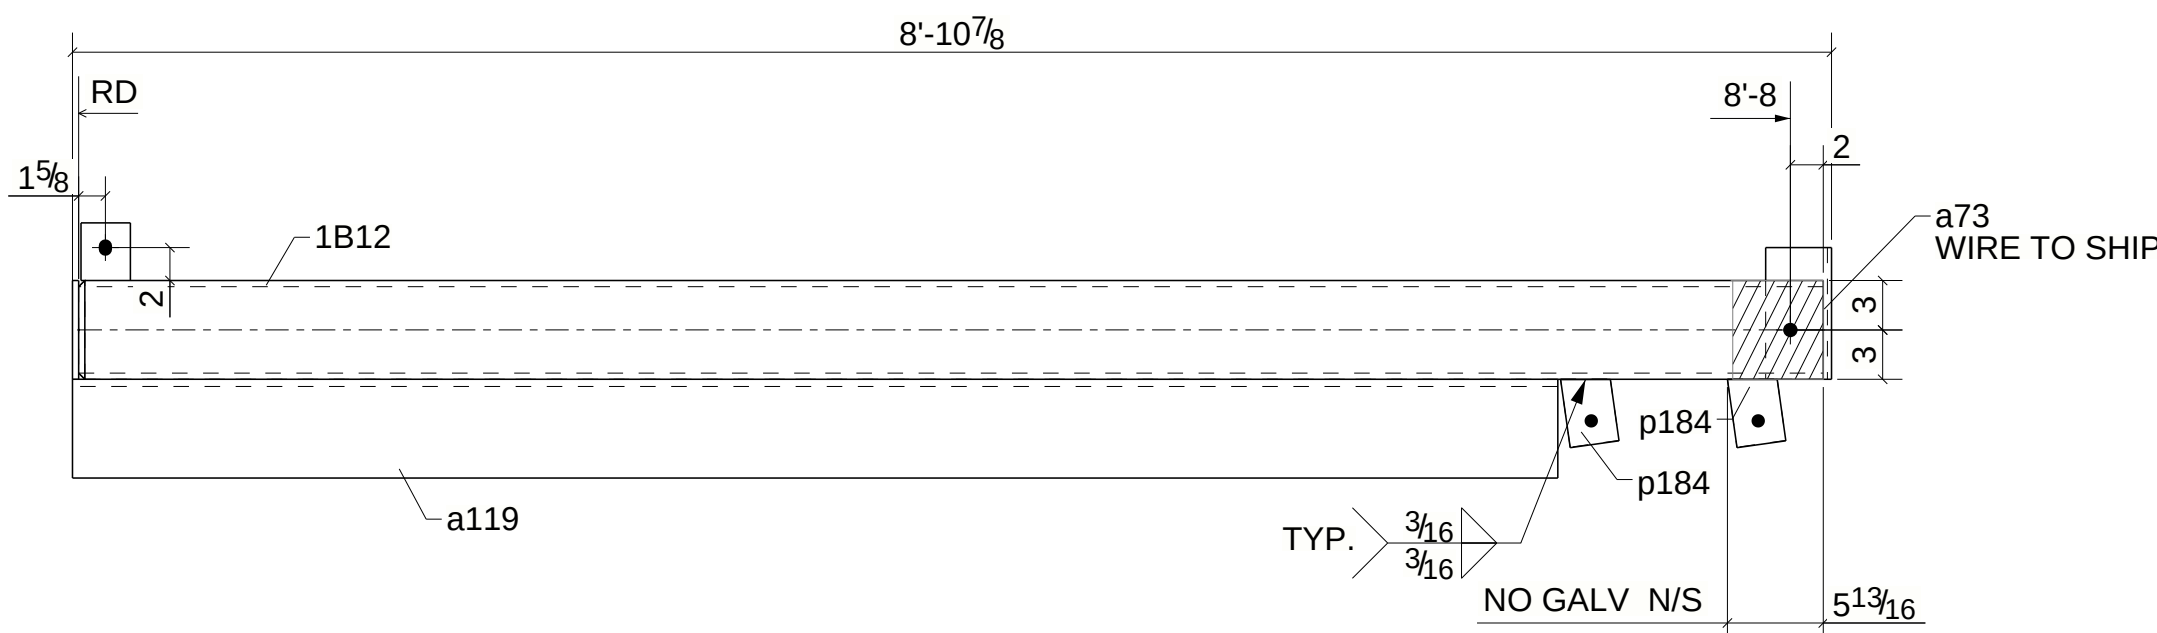

SHOP NOTE:

1. SHELF ANGLE SHOULD BE GALV. SEPERATELY BEFORE WELDING TO HSS,(SURFACE PREP : SSPC-SP3

ONE - HSS GIRT - 1B12

0	04/11/2025	For Fabrication
A	10/16/2024	For Approval
REV.	DATE	DESCRIPTION
MATERIAL A36 UNO		
HOLES 13/16 Ø UNO		
WELDS E70XX		
SURFACE PREP. SSPC SP2		
PAINT NOTE: SW SHOP PRIMER		

<