

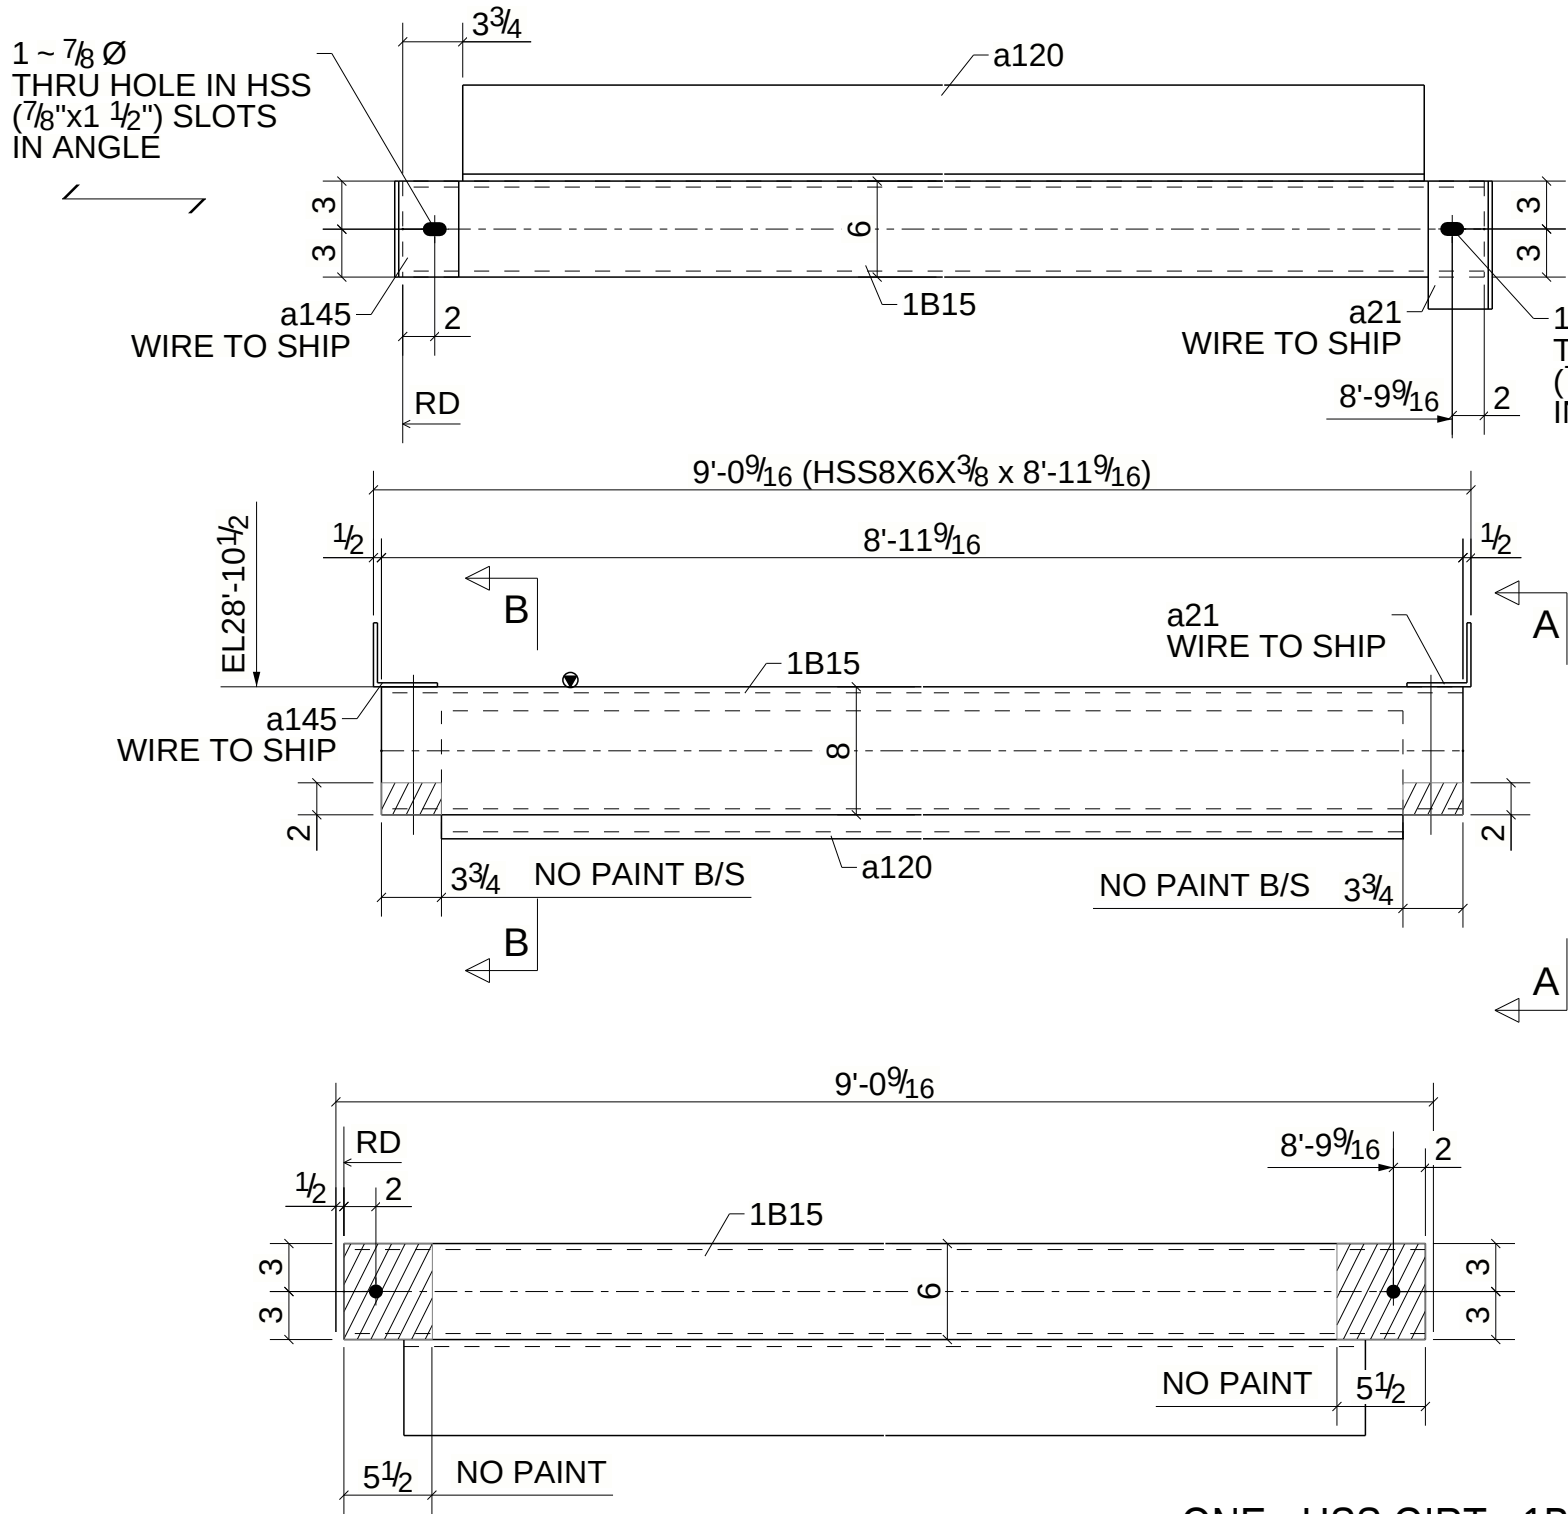


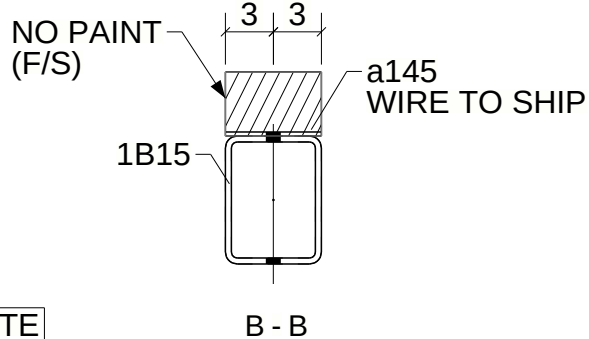

ONE - HSS GIRT - 1B15

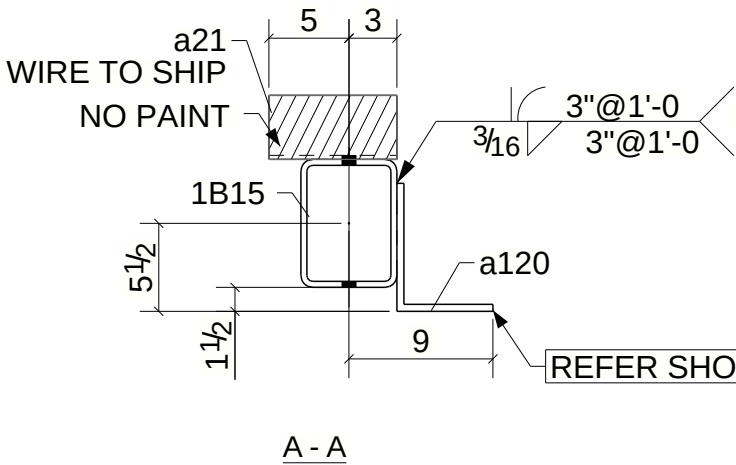

SHOP NOTE:
1. SHELF ANGLE SHOULD BE GALV. SEPERATELY BEFORE WELDING TO HSS.(SURFACE PREP : SSPC-SP3

BILL OF MATERIAL							
MARK	TOTAL QTY	SHAPE	LENGTH	TOTAL WEIGHT	REMARKS	ADV MILL #	STEEL GRADE
1B15	1	HSS8X6X3/8	8'-11 9/16"	274	SQ-2		A500-GR.B
a21	1	L4X4X1/4	0'-8"	4			A36
a120	1	L8X6X7/16	8'-4 1/16"	170	GALV.		A36
a145	1	L4X4X1/4	0'-6"	3			A36

0	04/11/2025	For Fabrication	PROJECT NAME GSC JUNIPER RBP PHASE-II			
A	10/16/2024	For Approval				
REV.	DATE	DESCRIPTION				
MATERIAL A36 UNO			LOCATION PARKWAY EVERETT, MA			
HOLES 13/16Ø UNO			CONTRACTOR BUILDING ENVELOPE SYSTEMS			
WELDS E70XX			DWG TITLE HSS GIRT			
SURFACE PREP. SSPC SP2			DRAWN BY ABJ	CHECKED BY HSR	DATE DRAWN 10/15/2024	PLOT DATE 10/15/2024
PAINT NOTE : SW SHOP PRIMER (U.N.O)			CONTRACT No. 24050		DWG No. 1B15	DGSTS No. --
						REV. 0



20 HIGH STREET
PLAINSVILLE, MA 02762
PHONE (508) 381-0429
www.teambes.com