

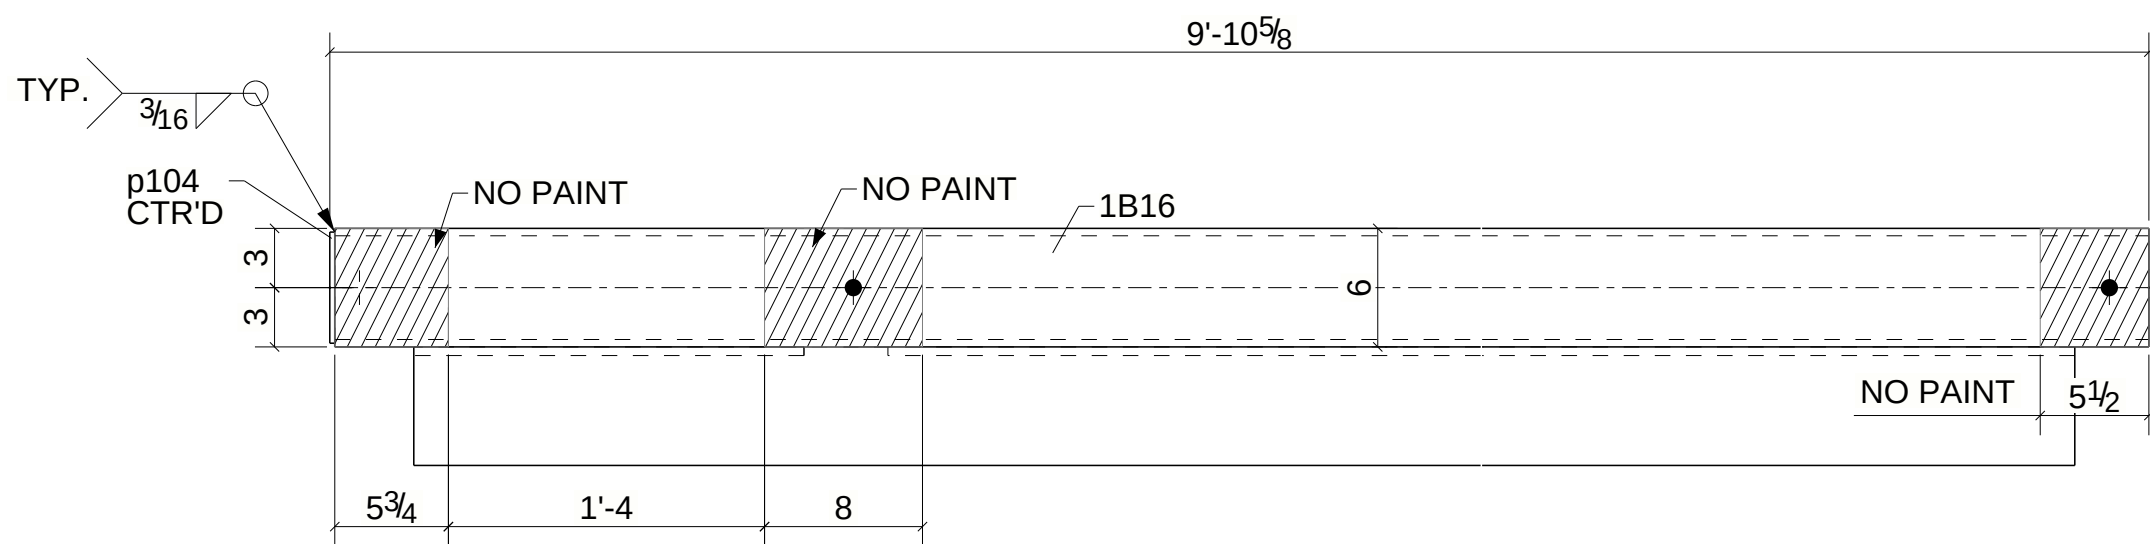
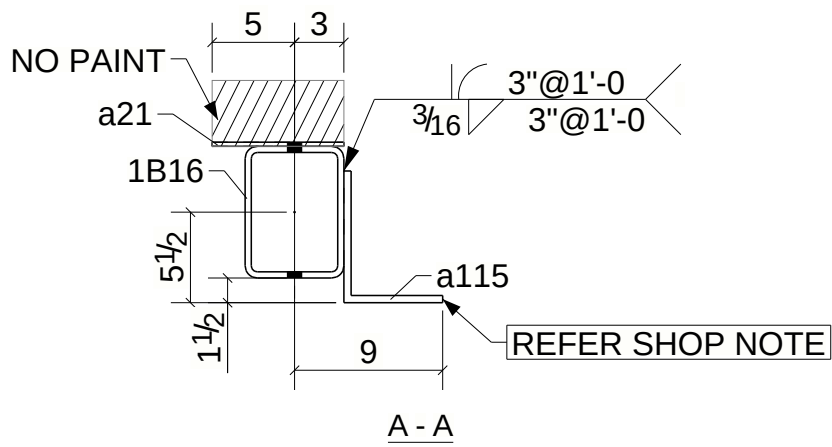


BILL OF MATERIAL							
MARK	TOTAL QTY	SHAPE	LENGTH	TOTAL WEIGHT	REMARKS	ADV MILL #	STEEL GRADE
1B16	2	HSS8X6X3/8	9'-10 3/8"	602	SQ-2		A500-GR B
a21	2	L4X4X1/4	0'-8"	9			A36
a115	2	L8X6X7/16	9'-2 5/8"	376	GALV.		A36
p104	2	PL1/4"x5 5/8"	0'-7 5/8"	6			A36

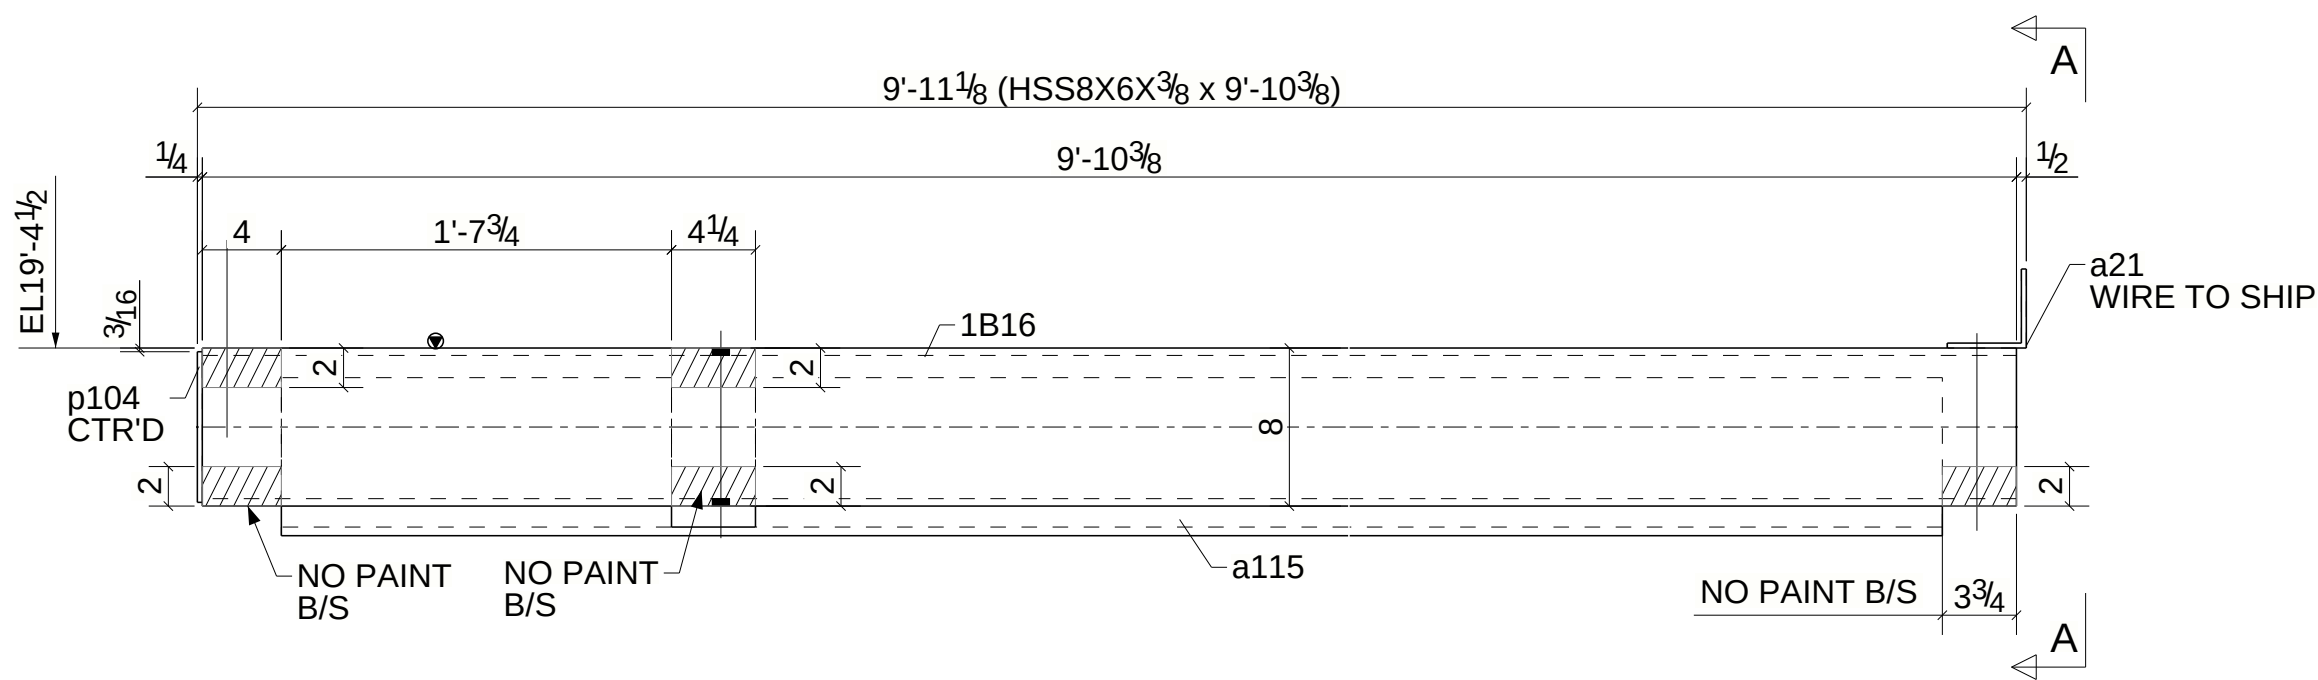

2 - HSS GIRTS - 1B16

SHOP NOTE:
1. SHELF ANGLE SHOULD BE GALV. SEPERATELY BEFORE WELDING TO HSS.(SURFACE PREP : SSPC-SP3

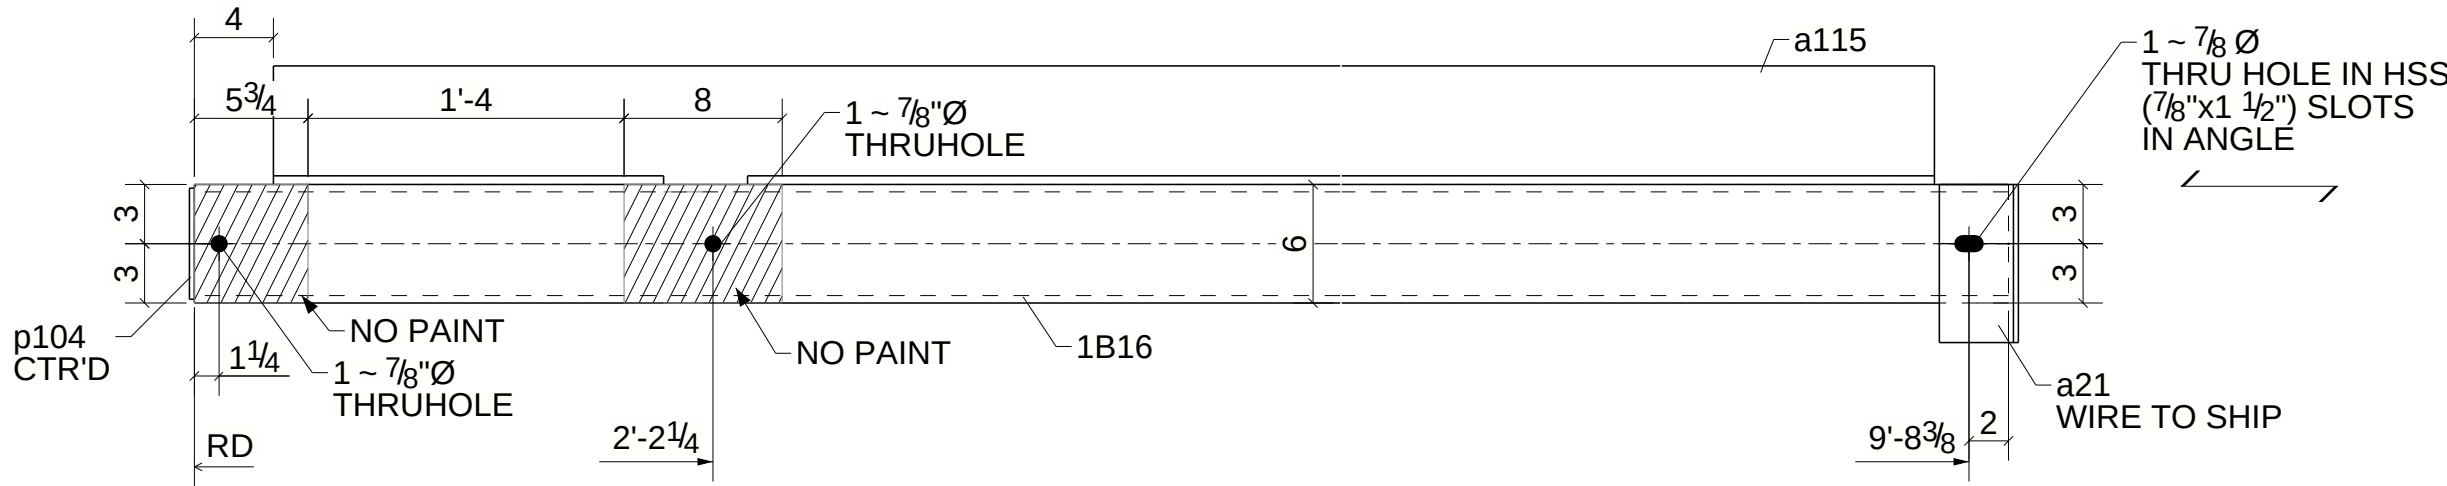

20 HIGH STREET
PLAINSVILLE, MA 02762
PHONE (508) 381-0429
www.teambes.com

0	04/11/2025	For Fabrication	PROJECT NAME			
A	10/16/2024	For Approval	GSC JUNIPER RBP PHASE-II			
REV.	DATE	DESCRIPTION	LOCATION			
MATERIAL A36 UNO			PARKWAY EVERETT, MA			
HOLES 13/16Ø UNO			CONTRACTOR			
WELDS E70XX			BUILDING ENVELOPE SYSTEMS			
SURFACE PREP. SSPC SP2			DWG TITLE			
PAINT NOTE: SW SHOP PRIMER			HSS GIRT			
DRAWN BY ABJ	CHECKED BY HSR	DATE DRAWN 10/15/2024	PLOT DATE 10/15/2024	DGSTS No. --		
CONTRACT No. 24050			DWG No. 1B16		REV.	0