


BILL OF MATERIAL							
MARK	TOTAL QTY	SHAPE	LENGTH	TOTAL WEIGHT	REMARKS	ADV MILL #	STEEL GRADE
1B20	2	HSS8X6X3/8	10'-1 1/8"	616	SQ-2		A500-GR B
a59	2	L4X4X1/4	0'-8"	9			A36
a113	2	L8X6X7/16	9'-5 3/8"	385	GALV.		A36
p104	2	PL1/4"X5 5/8"	0'-7 5/8"	6			A36

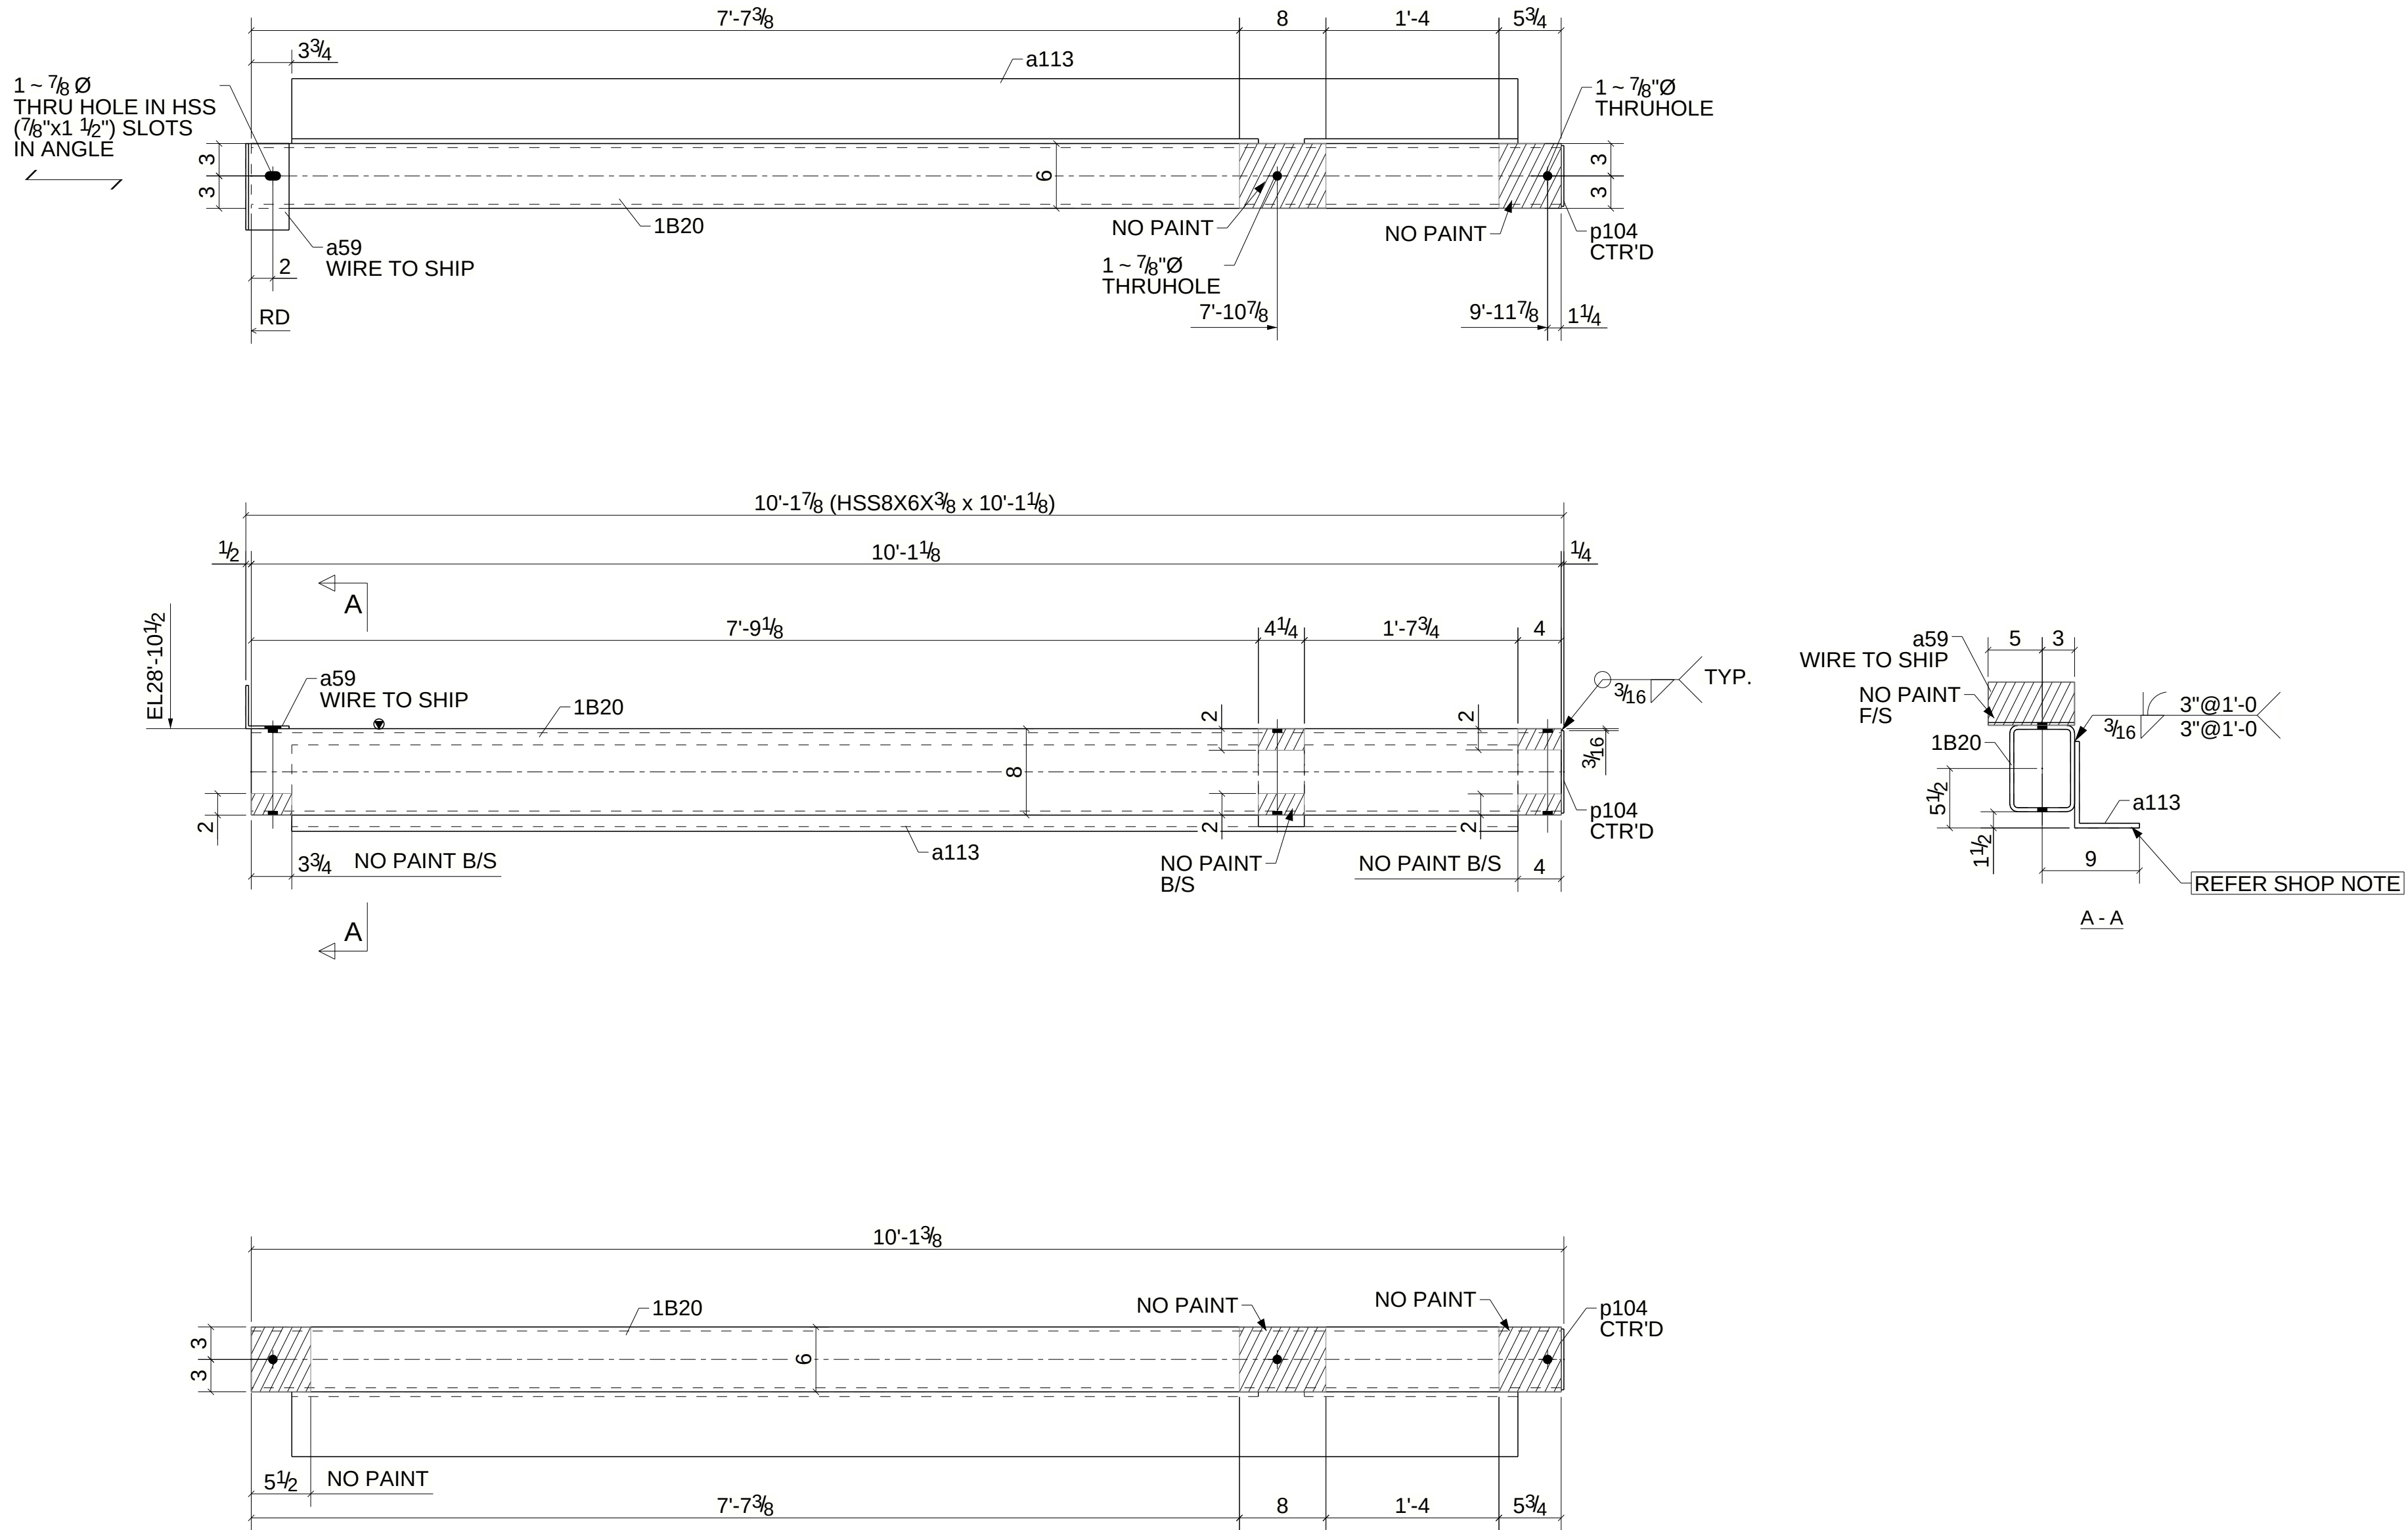

2 - HSS GIRTS - 1B20

SHOP NOTE:
1. SHELF ANGLE SHOULD BE GALV. SEPERATELY BEFORE WELDING TO HSS.(SURFACE PREP : SSPC-SP3

0	04/11/2025	For Fabrication	PROJECT NAME				
A	10/16/2024	For Approval	GSC JUNIPER RBP PHASE-II				
REV.	DATE	DESCRIPTION	LOCATION				
MATERIAL			PARKWAY EVERETT, MA				
HOLES			CONTRACTOR				
13/16Ø UNO			BUILDING ENVELOPE SYSTEMS				
WELDS			DWG TITLE				
E70XX			HSS GIRT				
SURFACE PREP.		DRAWN BY	CHECKED BY	DATE DRAWN	PLOT DATE	DGSTS No.	
SSPC SP2		ABJ	HSR	10/15/2024	10/15/2024	--	
PAINT NOTE:		CONTRACT No.		DWG No.		REV.	
SW SHOP PRIMER (U.N.O)		24050		1B20			0

Building Envelope Systems

20 HIGH STREET
PLAINSVILLE, MA 02762
PHONE (508) 381-0429
www.teambes.com