


BILL OF MATERIAL							
MARK	TOTAL QTY	SHAPE	LENGTH	TOTAL WEIGHT	REMARKS	ADV MILL #	STEEL GRADE
1B21	1	HSS8X6X3/8	10'-1 1/8"	308	SQ-2		A500-GR B
a59	1	L4X4X1/4	0'-8"	4			A36
p104	1	PL1/4"X5 5/8"	0'-7 5/8"	3			A36

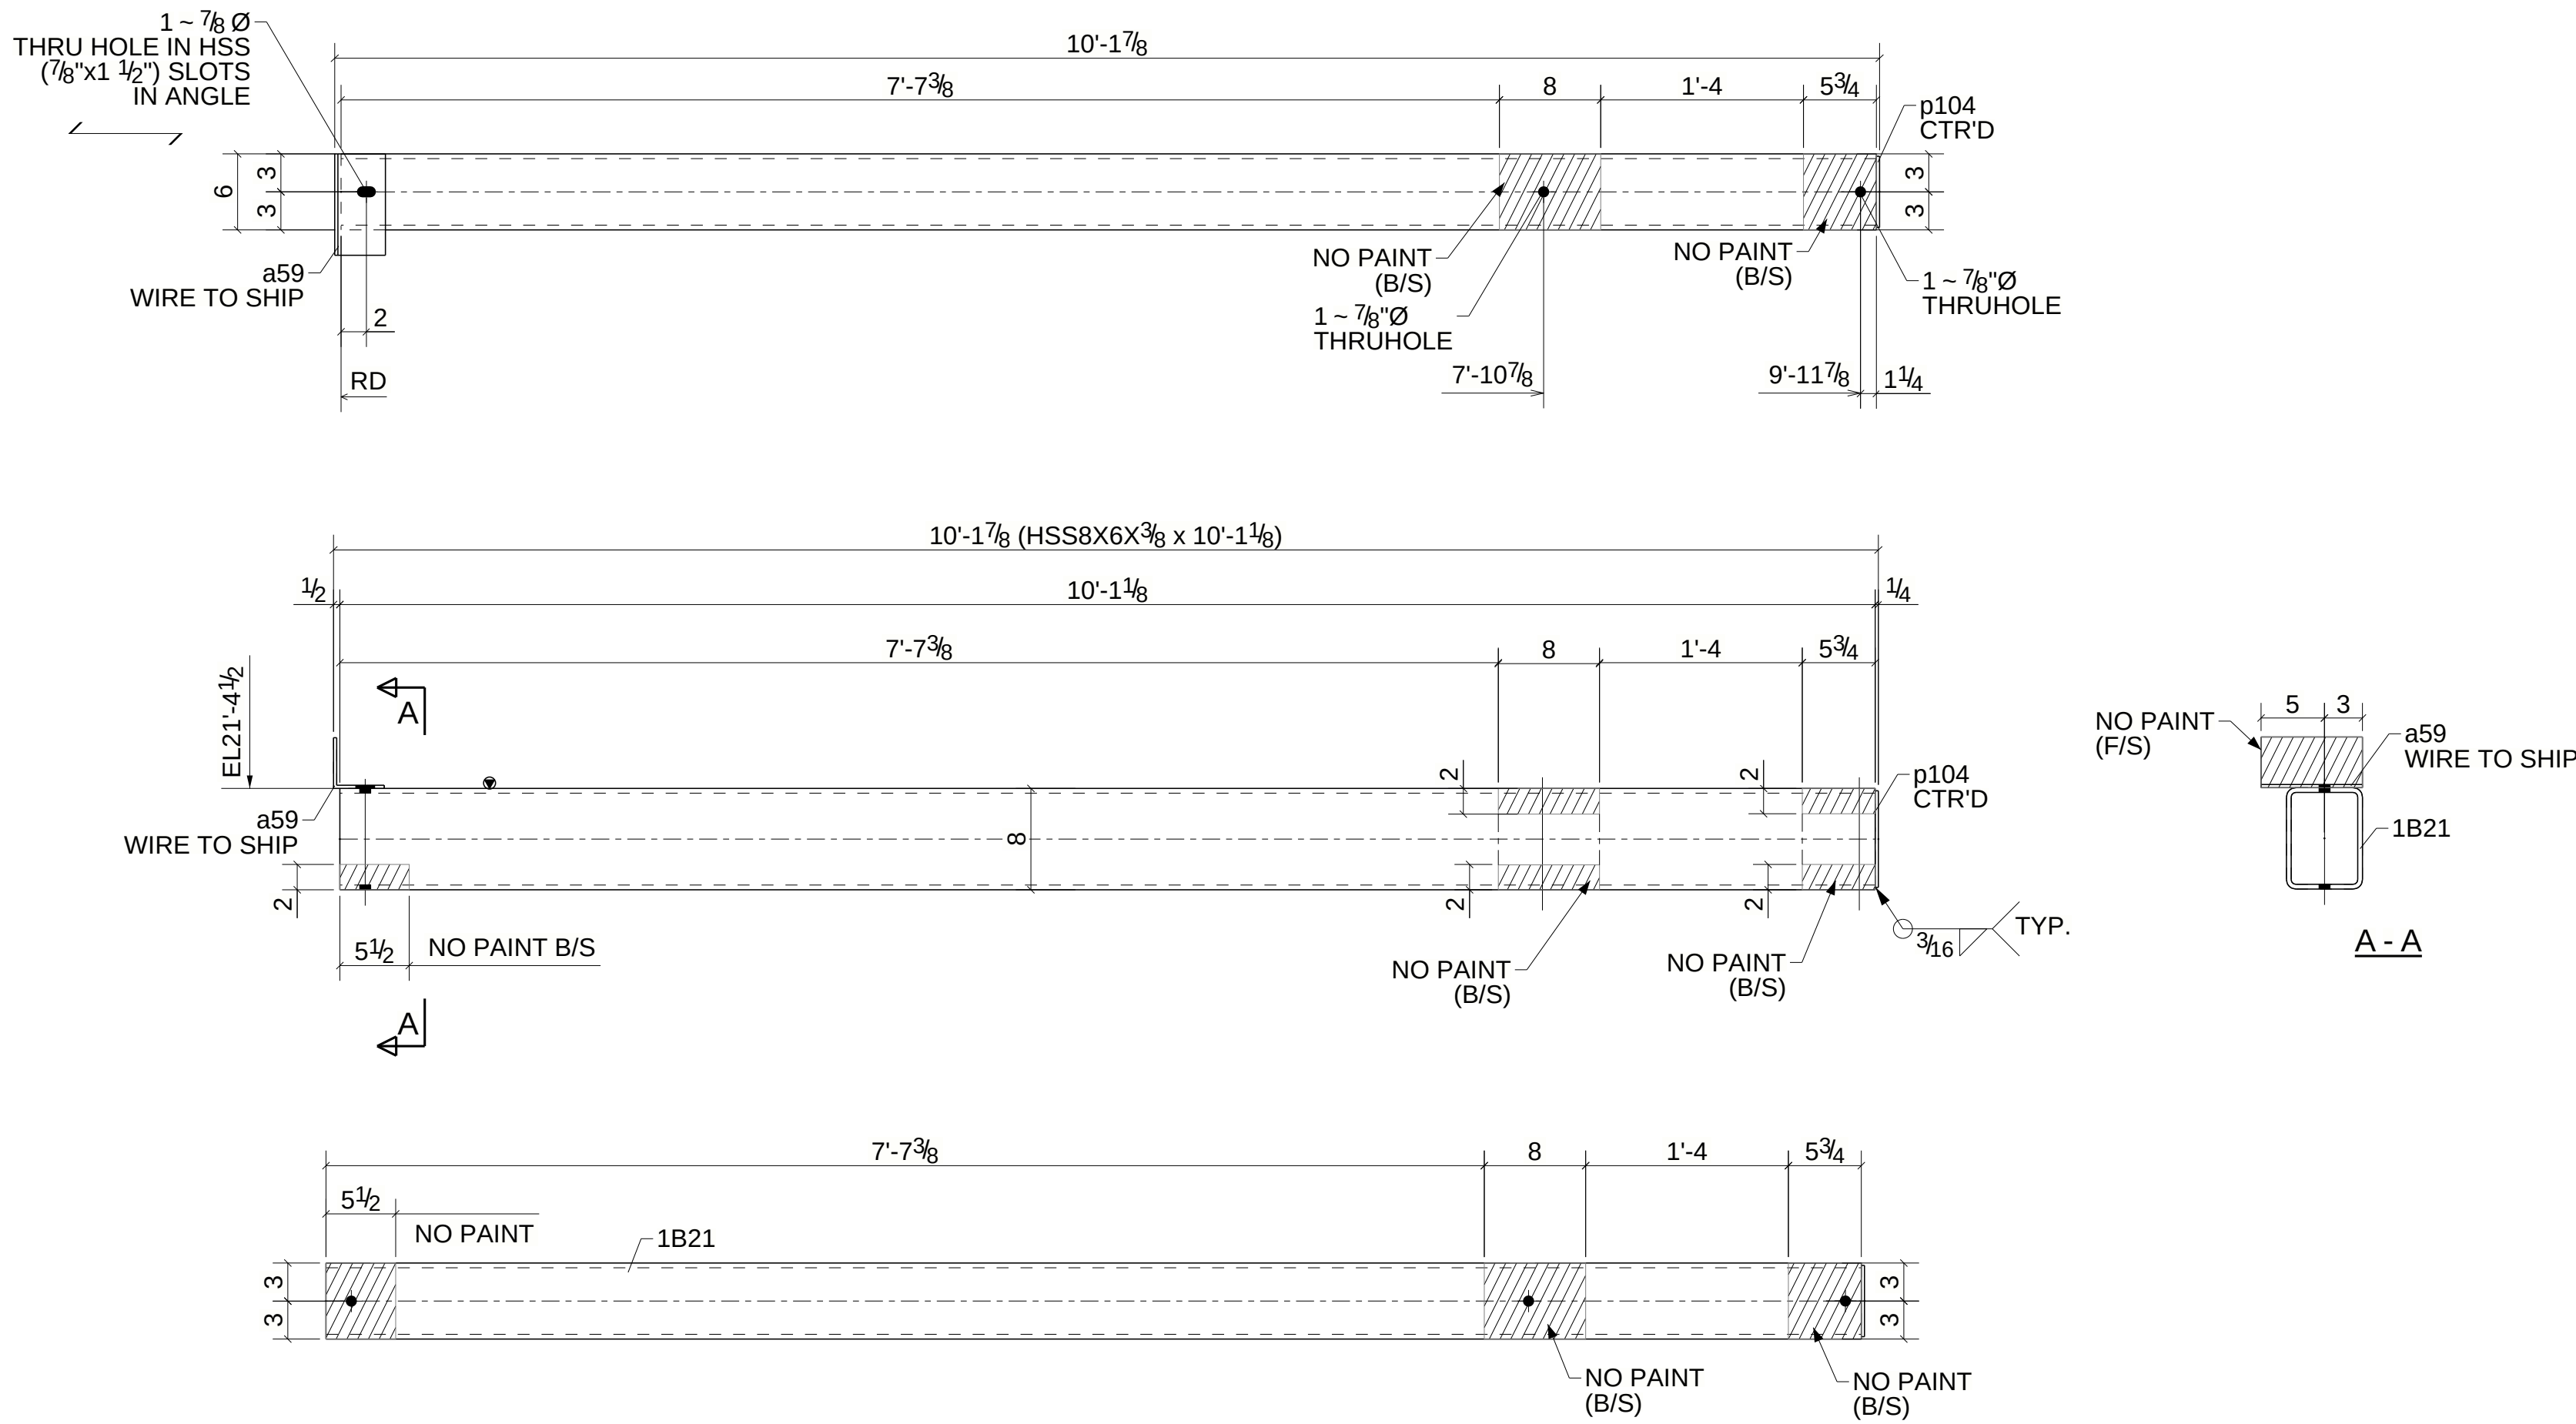

ONE - HSS GIRT - 1B21

0	04/11/2025	For Fabrication
A	10/15/2024	For Approval
REV.	DATE	DESCRIPTION
MATERIAL	A36 UNO	
HOLES	13/16 Ø UNO	
WELDS	E70XX	
SURFACE PREP.	SSPC SP2	
PAINT NOTE:	SW SHOP PRIMER	

Building Envelope Systems

20 HIGH STREET
PLAINSVILLE, MA 02762
PHONE (508) 381-0429
www.teambes.com

PROJECT NAME
GSC JUNIPER RBP PHASE-II

LOCATION
PARKWAY EVERETT, MA

CONTRACTOR
BUILDING ENVELOPE SYSTEMS

DWG TITLE
HSS GIRT

DRAWN BY
ABJ

CHECKED BY
HSR

DATE DRAWN
10/15/2024

PLOT DATE
10/15/2024

DGSTS No.
--

CONTRACT No. 24050

DWG No. 1B21

REV.
0