

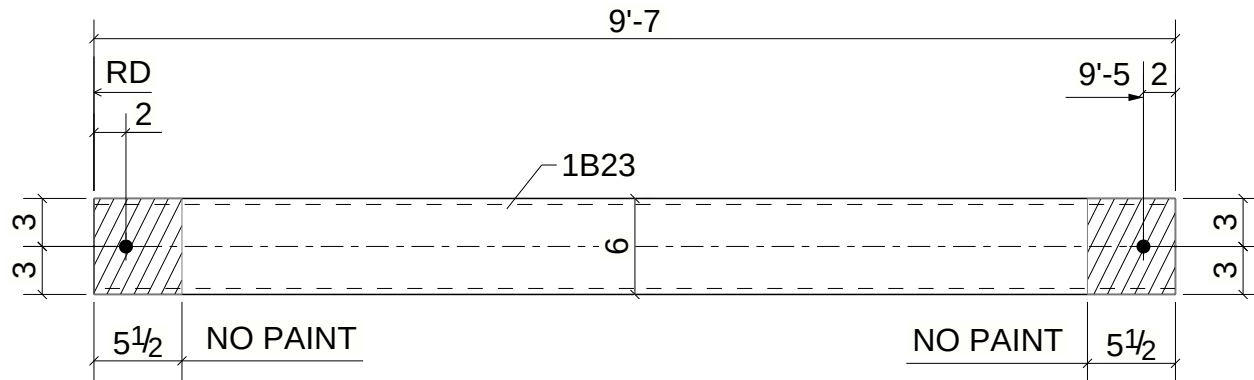
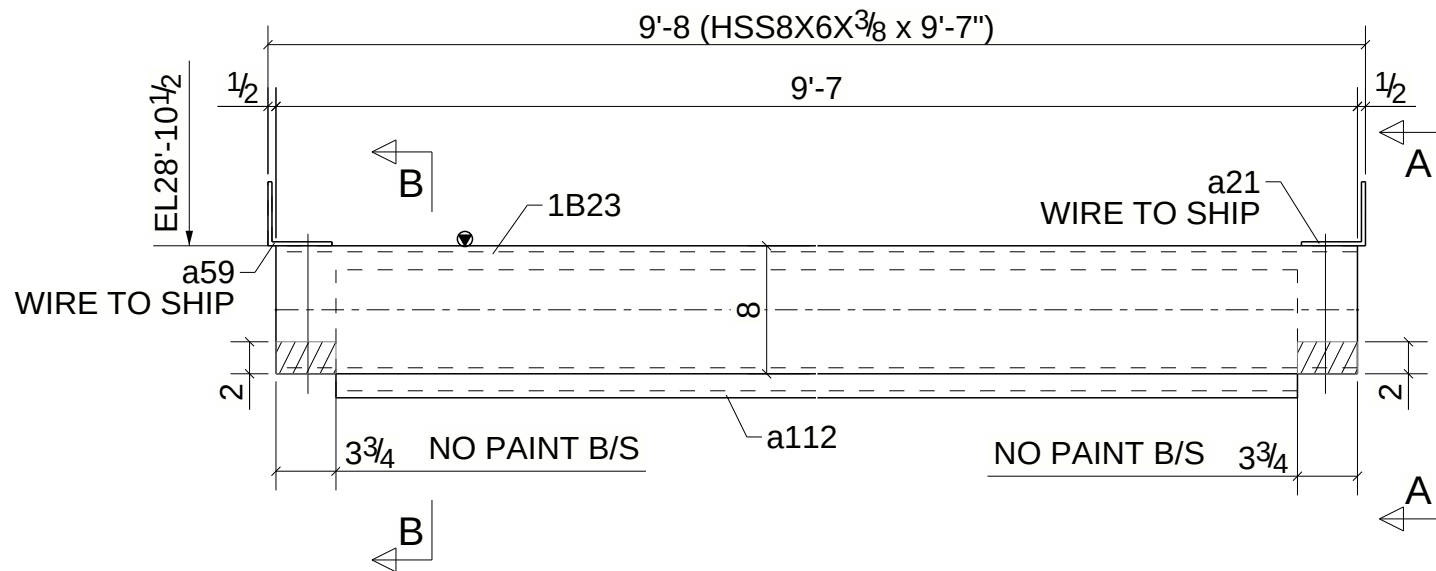
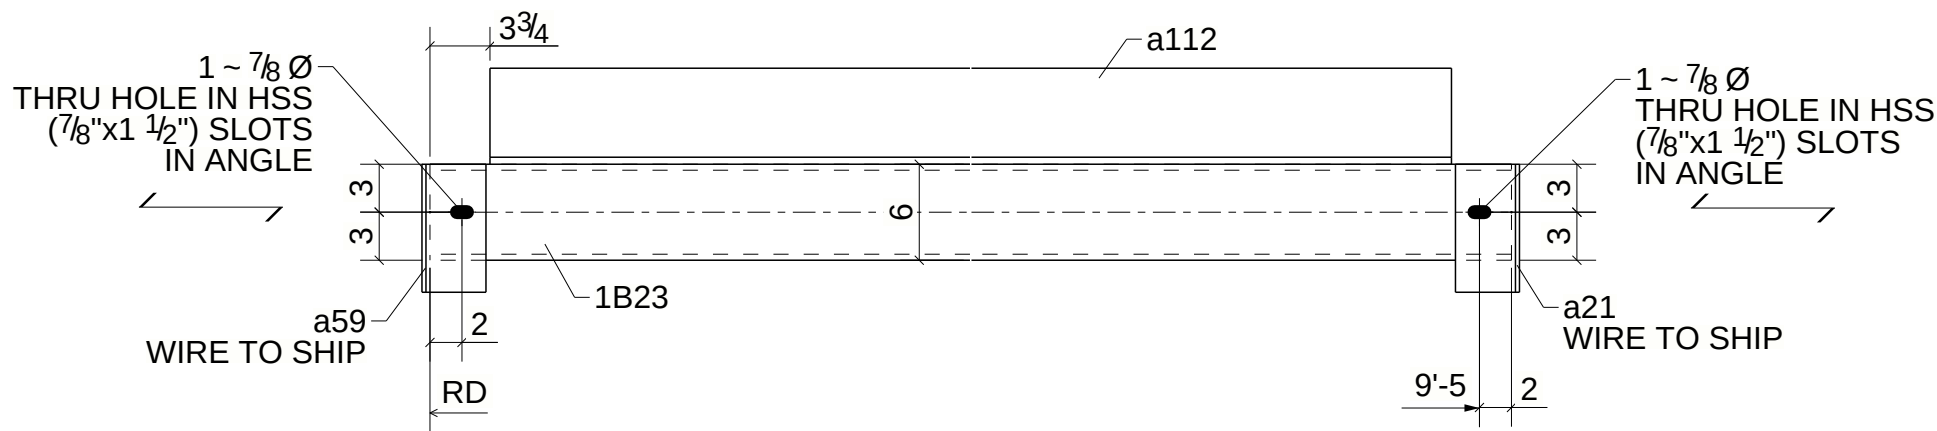


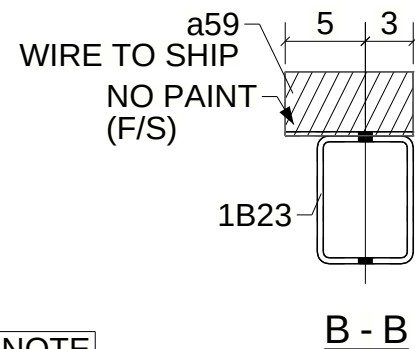

2 - HSS GIRTS - 1B23

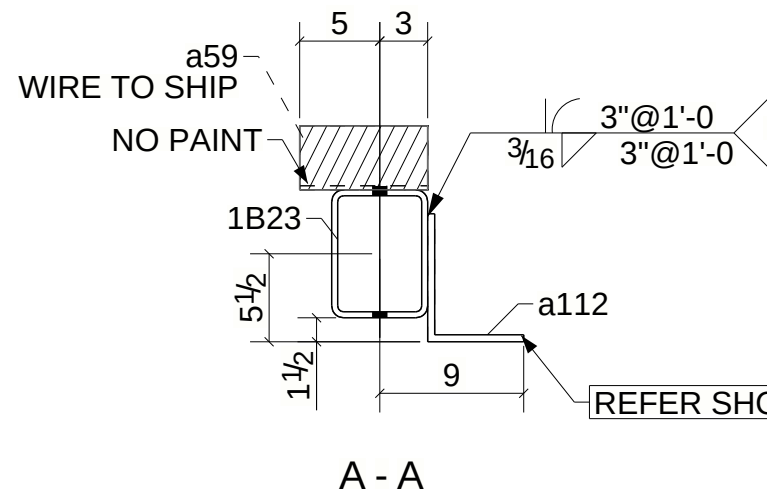

SHOP NOTE:

1. SHELF ANGLE SHOULD BE GALV. SEPERATELY BEFORE WELDING TO HSS.(SURFACE PREP : SSPC-SP3

BILL OF MATERIAL							
MARK	TOTAL QTY	SHAPE	LENGTH	TOTAL WEIGHT	REMARKS	ADV MILL #	STEEL GRADE
1B23	2	HSS8X6X3/8	9'-7"	585	SQ-2		A500-GR.B
a21	2	L4X4X1/4	0'-8"	9			A36
a59	2	L4X4X1/4	0'-8"	9			A36
a112	2	L8X6X7/16	8'-11 1/2"	365	GALV.		A36

0	04/11/2025	For Fabrication	PROJECT NAME GSC JUNIPER RBP PHASE-II				
A	10/16/2024	For Approval					
REV.	DATE	DESCRIPTION	LOCATION PARKWAY EVERETT, MA				
MATERIAL A36 UNO			CONTRACTOR BUILDING ENVELOPE SYSTEMS				
HOLES 13/16Ø UNO			DWG TITLE HSS GIRT				
WELDS E70XX			DRAWN BY ABJ	CHECKED BY HSR	DATE DRAWN 10/15/2024	PLOT DATE 10/15/2024	DGSTS No. --
SURFACE PREP. SSPC SP2			CONTRACT No. 24050		DWG No. 1B23		REV.
PAINT NOTE : SW SHOP PRIMER (U.N.O)							0

Building Envelope Systems



20 HIGH STREET
PLAINSVILLE, MA 02762
PHONE (508) 381-0429
www.teambes.com