


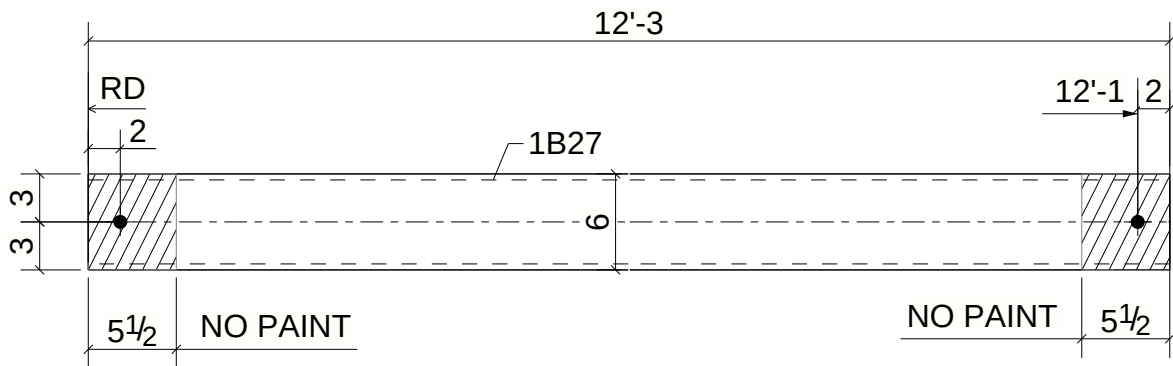


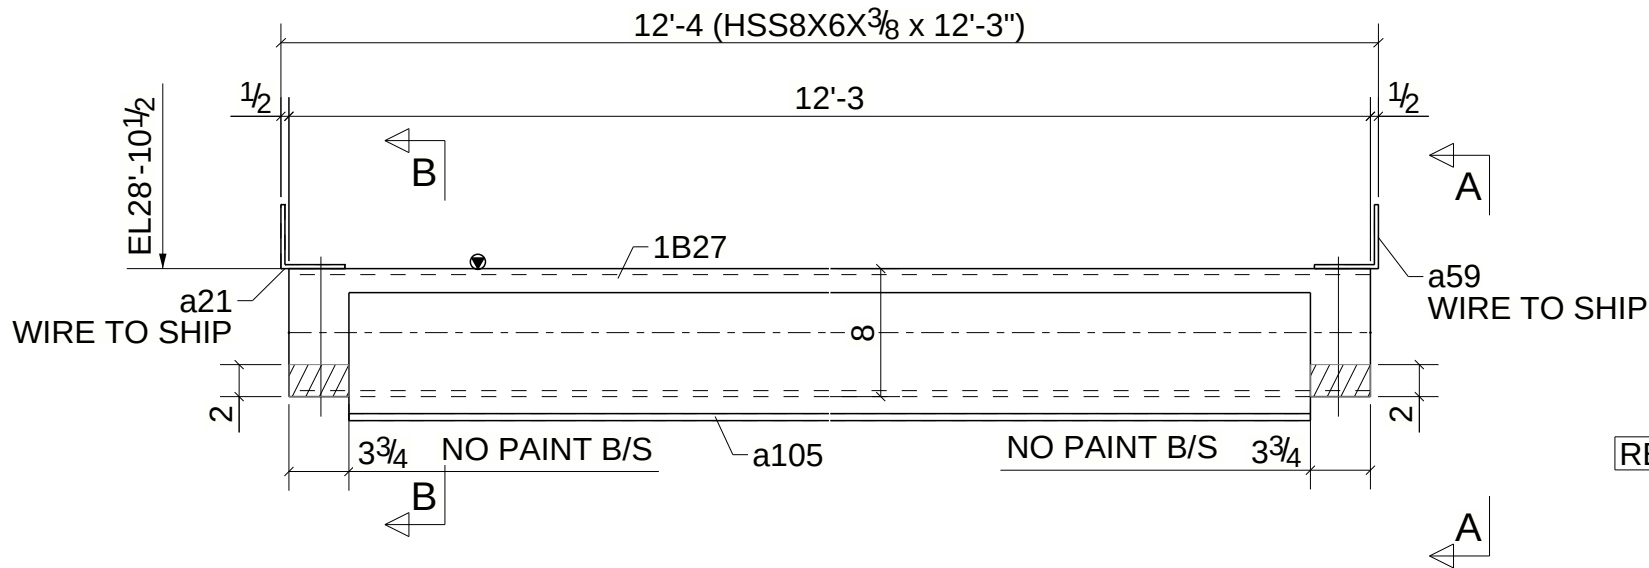

2 - HSS GIRTS - 1B27

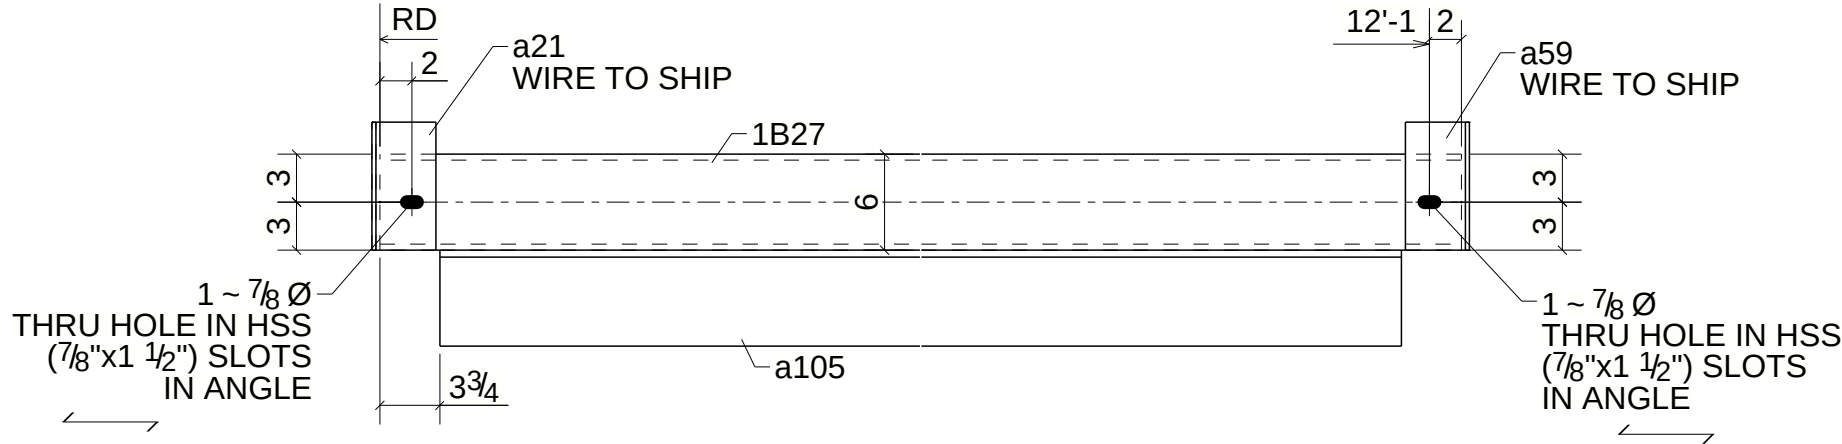

SHOP NOTE:  
1. SHELF ANGLE SHOULD BE GALV. SEPERATELY BEFORE WELDING TO HSS.(SURFACE PREP : SSPC-SP3)

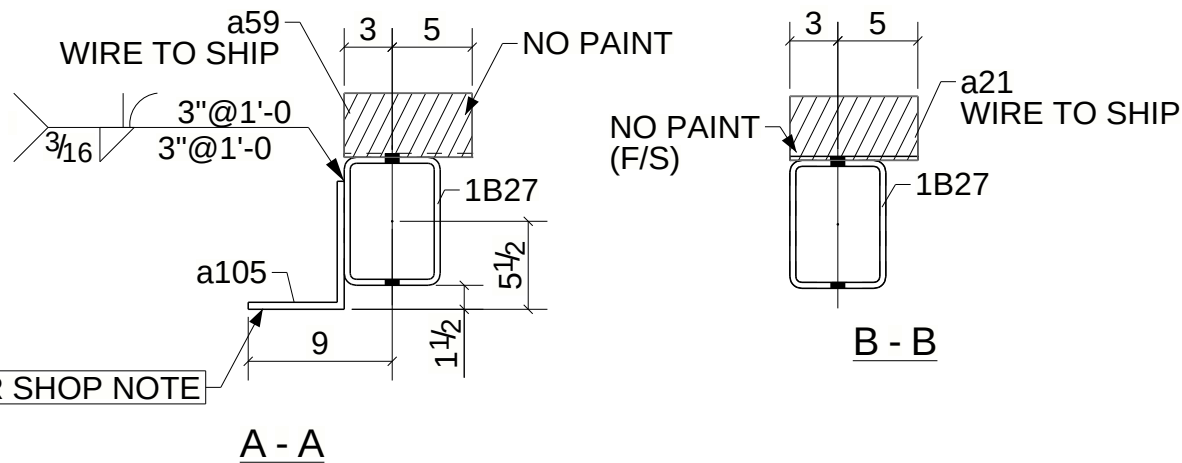

20 HIGH STREET  
PLAINSVILLE, MA 02762  
PHONE (508) 381-0429  
www.teambes.com

|                                        |            |                 |                           |                   |                          |                         |
|----------------------------------------|------------|-----------------|---------------------------|-------------------|--------------------------|-------------------------|
| 0                                      | 04/11/2025 | For Fabrication | PROJECT NAME              |                   |                          |                         |
| A                                      | 10/16/2024 | For Approval    | GSC JUNIPER RBP PHASE-II  |                   |                          |                         |
| REV.                                   | DATE       | DESCRIPTION     | LOCATION                  |                   |                          |                         |
| MATERIAL<br>A36 UNO                    |            |                 | PARKWAY EVERETT, MA       |                   |                          |                         |
| HOLES<br>13/16Ø UNO                    |            |                 | CONTRACTOR                |                   |                          |                         |
| WELDS<br>E70XX                         |            |                 | BUILDING ENVELOPE SYSTEMS |                   |                          |                         |
| SURFACE PREP.<br>SSPC SP2              |            |                 | DWG TITLE                 |                   |                          |                         |
| PAINT NOTE :<br>SW SHOP PRIMER (U.N.O) |            |                 | HSS GIRT                  |                   |                          |                         |
|                                        |            |                 | DRAWN BY<br>ABJ           | CHECKED BY<br>HSR | DATE DRAWN<br>10/15/2024 | PLOT DATE<br>10/15/2024 |
|                                        |            |                 | CONTRACT No. 24050        |                   | DWG No. 1B27             | DGSTS No.<br>--         |
|                                        |            |                 |                           |                   |                          | REV.<br>0               |

| BILL OF MATERIAL |           |            |            |              |         |            |             |
|------------------|-----------|------------|------------|--------------|---------|------------|-------------|
| MARK             | TOTAL QTY | SHAPE      | LENGTH     | TOTAL WEIGHT | REMARKS | ADV MILL # | STEEL GRADE |
| 1B27             | 2         | HSS8X6X3/8 | 12'-3"     | 748          | SQ-2    |            | A500-GR.B   |
| a21              | 2         | L4X4X1/4   | 0'-8"      | 9            |         |            | A36         |
| a59              | 2         | L4X4X1/4   | 0'-8"      | 9            |         |            | A36         |
| a105             | 2         | L8X6X7/16  | 11'-7 1/2" | 474          | GALV.   |            | A36         |