
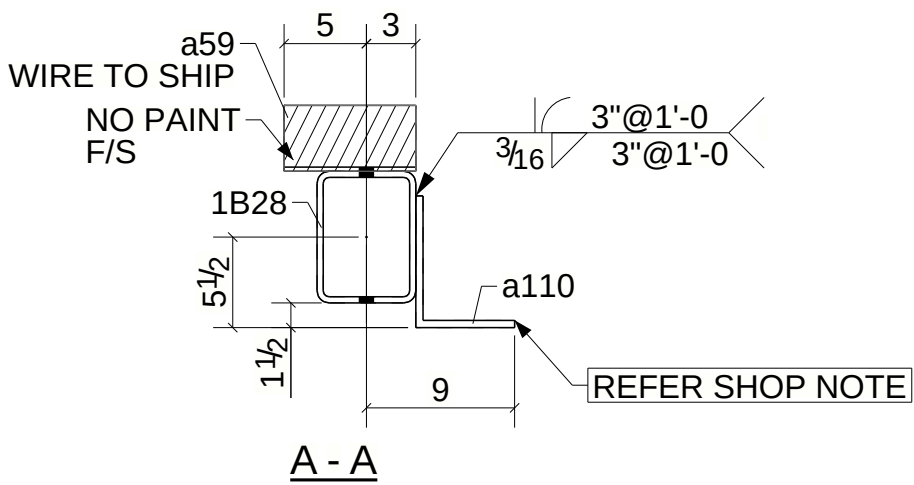


| BILL OF MATERIAL |           |               |           |              |         |            |             |
|------------------|-----------|---------------|-----------|--------------|---------|------------|-------------|
| MARK             | TOTAL QTY | SHAPE         | LENGTH    | TOTAL WEIGHT | REMARKS | ADV MILL # | STEEL GRADE |
| 1B28             | 2         | HSS8X6X3/8    | 8'-2"     | 499          | SQ-2    |            | A500-GR B   |
| a59              | 2         | L4X4X1/4      | 0'-8"     | 9            |         |            | A36         |
| a110             | 2         | L8X6X7/16     | 7'-6 1/4" | 307          | GALV.   |            | A36         |
| p104             | 2         | PL1/4"X5 5/8" | 0'-7 5/8" | 6            |         |            | A36         |

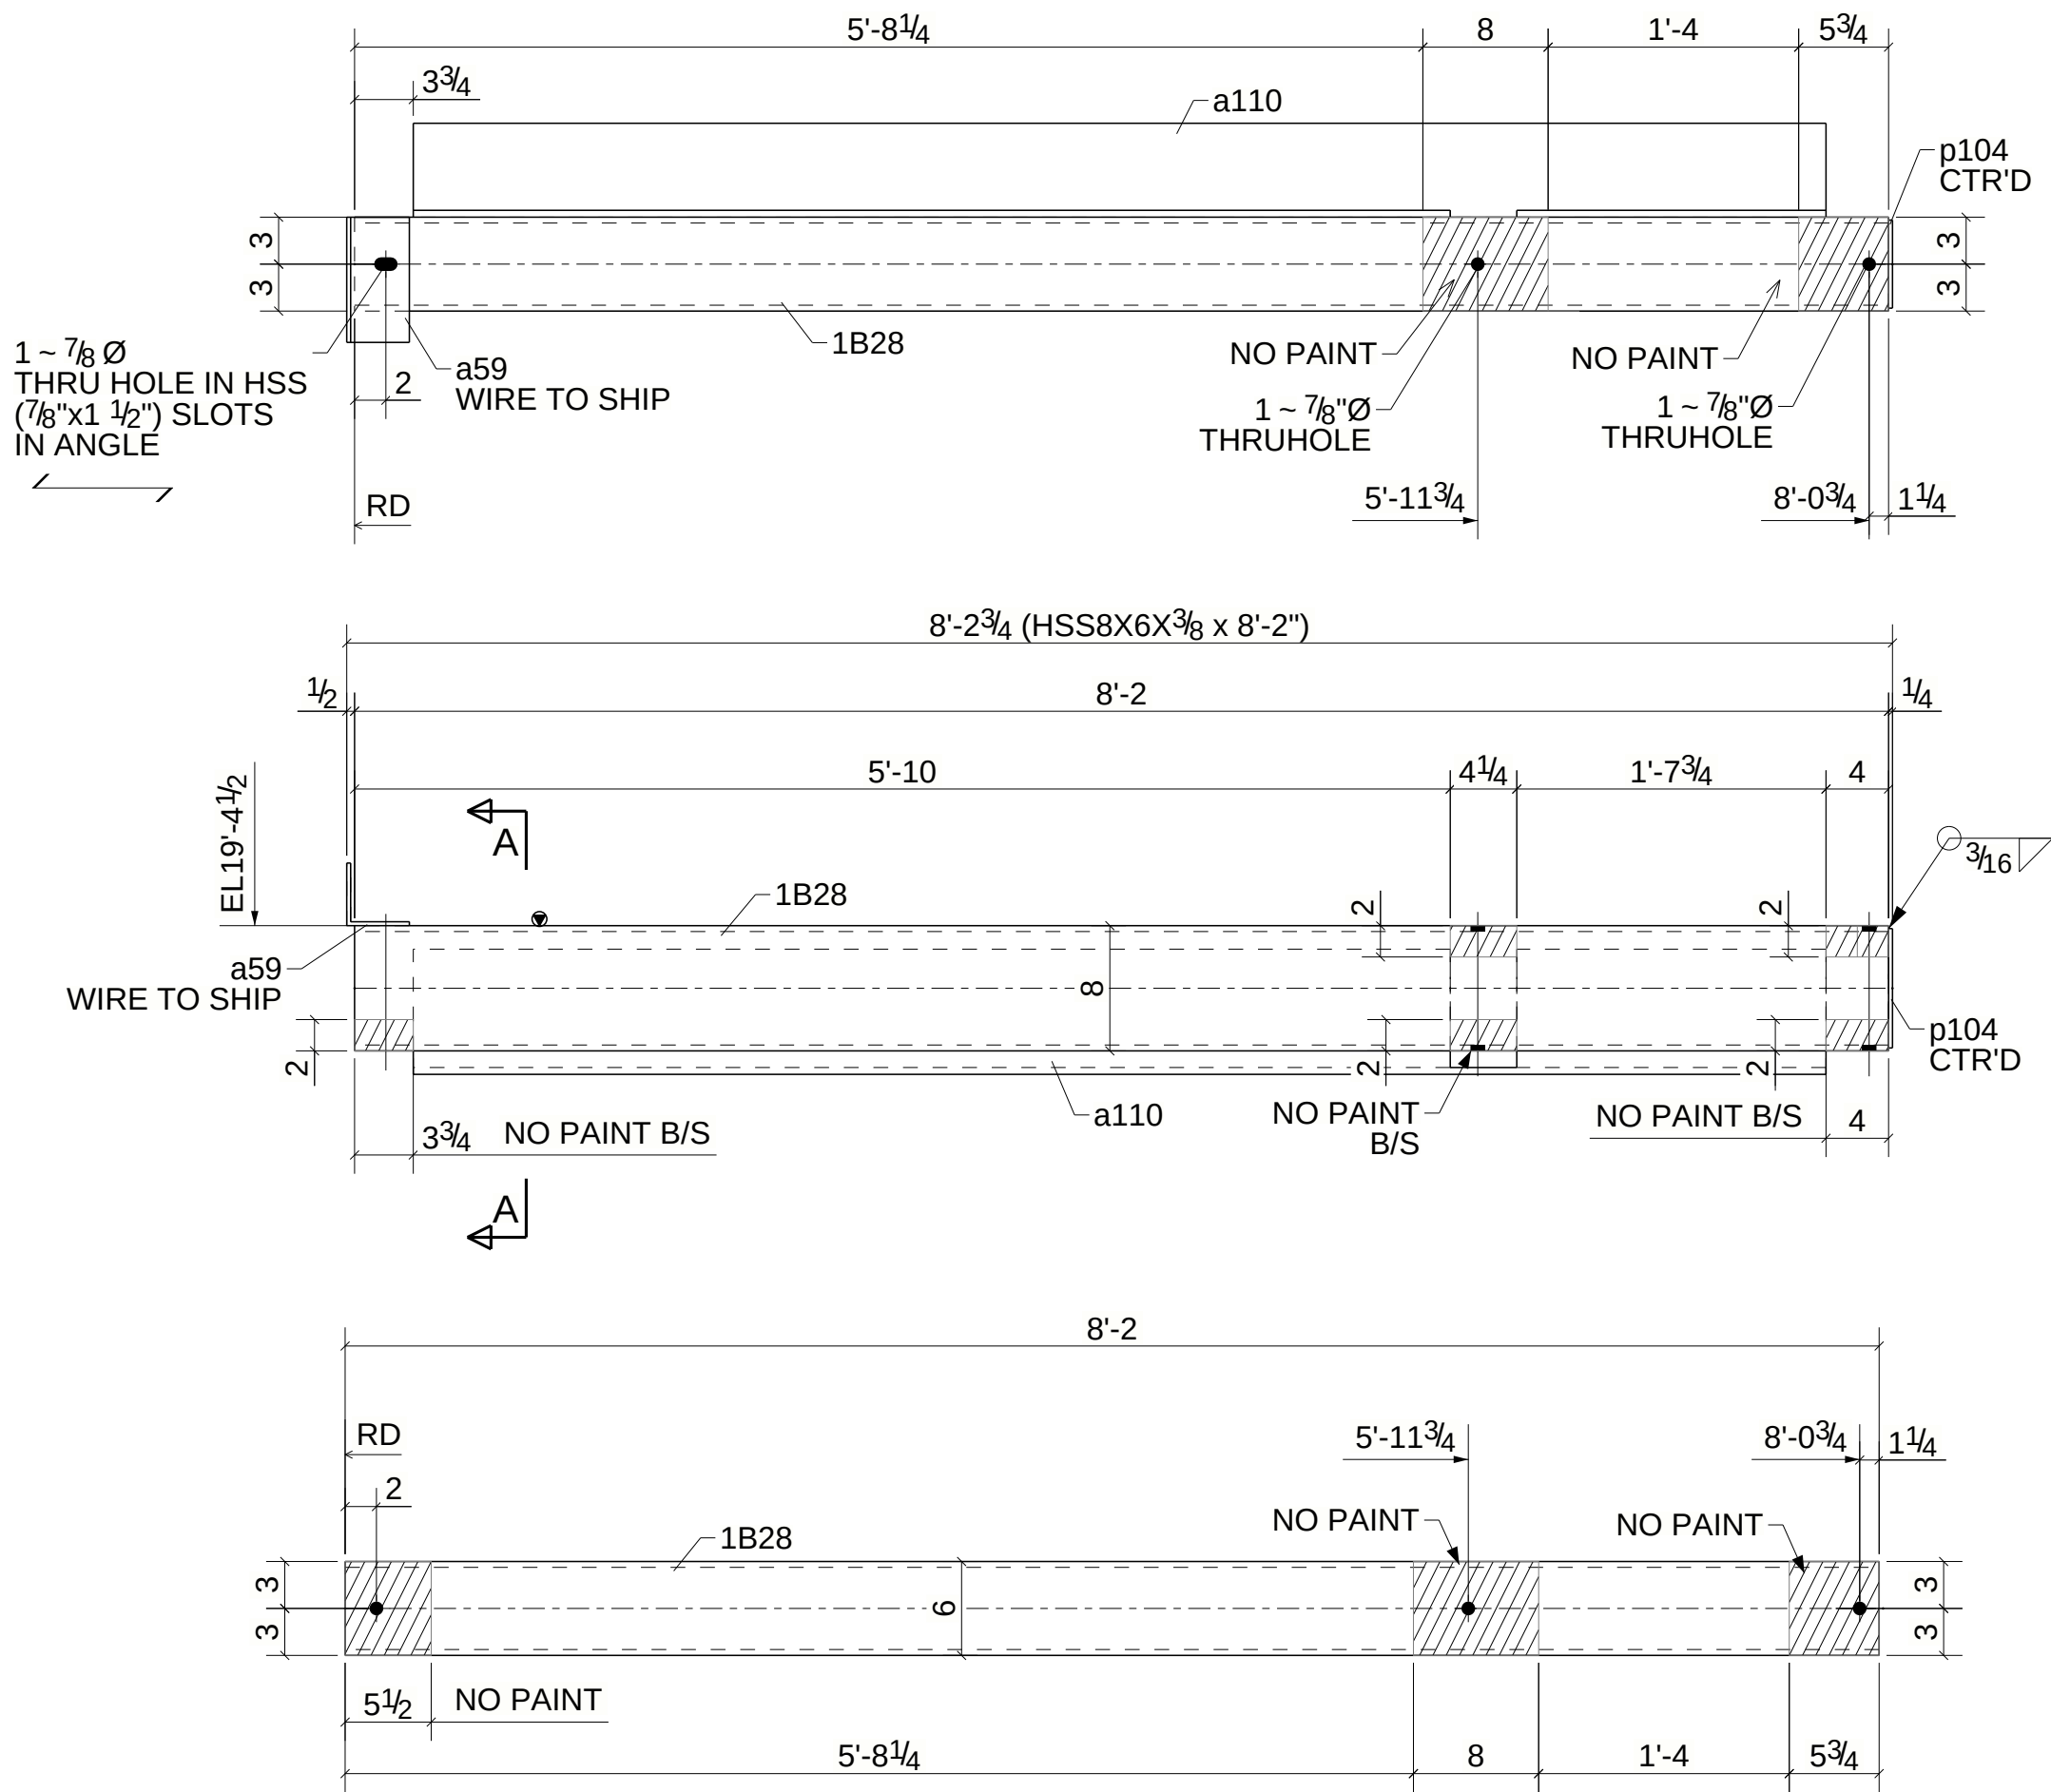

SHOP NOTE:  
1. SHELF ANGLE SHOULD BE GALV. SEPERATELY BEFORE WELDING TO HSS.(SURFACE PREP : SSPC-SP3)

**Building Envelope Systems**

20 HIGH STREET  
PLAINSVILLE, MA 02762  
PHONE (508) 381-0429  
www.teambes.com

|                           |            |                 |                           |                   |                          |                         |      |
|---------------------------|------------|-----------------|---------------------------|-------------------|--------------------------|-------------------------|------|
| 0                         | 04/11/2025 | For Fabrication | PROJECT NAME              |                   |                          |                         |      |
| A                         | 10/16/2024 | For Approval    | GSC JUNIPER RBP PHASE-II  |                   |                          |                         |      |
| REV.                      | DATE       | DESCRIPTION     | LOCATION                  |                   |                          |                         |      |
| MATERIAL<br>A36 UNO       |            |                 | PARKWAY EVERETT, MA       |                   |                          | CONTRACTOR              |      |
|                           |            |                 | BUILDING ENVELOPE SYSTEMS |                   |                          |                         |      |
| HOLES<br>13/16Ø UNO       |            |                 | DWG TITLE                 |                   |                          | DWGSTS No.              |      |
|                           |            |                 | HSS GIRT                  |                   |                          | --                      |      |
| WELDS<br>E70XX            |            |                 | DRAWN BY<br>ABJ           | CHECKED BY<br>HSR | DATE DRAWN<br>10/15/2024 | PLOT DATE<br>10/15/2024 | REV. |
|                           |            |                 | CONTRACT NO. 24050        |                   | DWG NO. 1B28             |                         | 0    |
| SURFACE PREP.<br>SSPC SP2 |            |                 | PAINT NOTE :              |                   |                          |                         |      |
| SW SHOP PRIMER (U.N.O)    |            |                 |                           |                   |                          |                         |      |

2 - HSS GIRTS - 1B28