


BILL OF MATERIAL							
MARK	TOTAL QTY	SHAPE	LENGTH	TOTAL WEIGHT	REMARKS	ADV MILL #	STEEL GRADE
1B29	1	HSS8X6X3/8	8'-2"	249	SQ-2		A500-GR B
a59	1	L4X4X1/4	0'-8"	4			A36
p104	1	PL1/4"X5 5/8"	0'-7 5/8"	3			A36

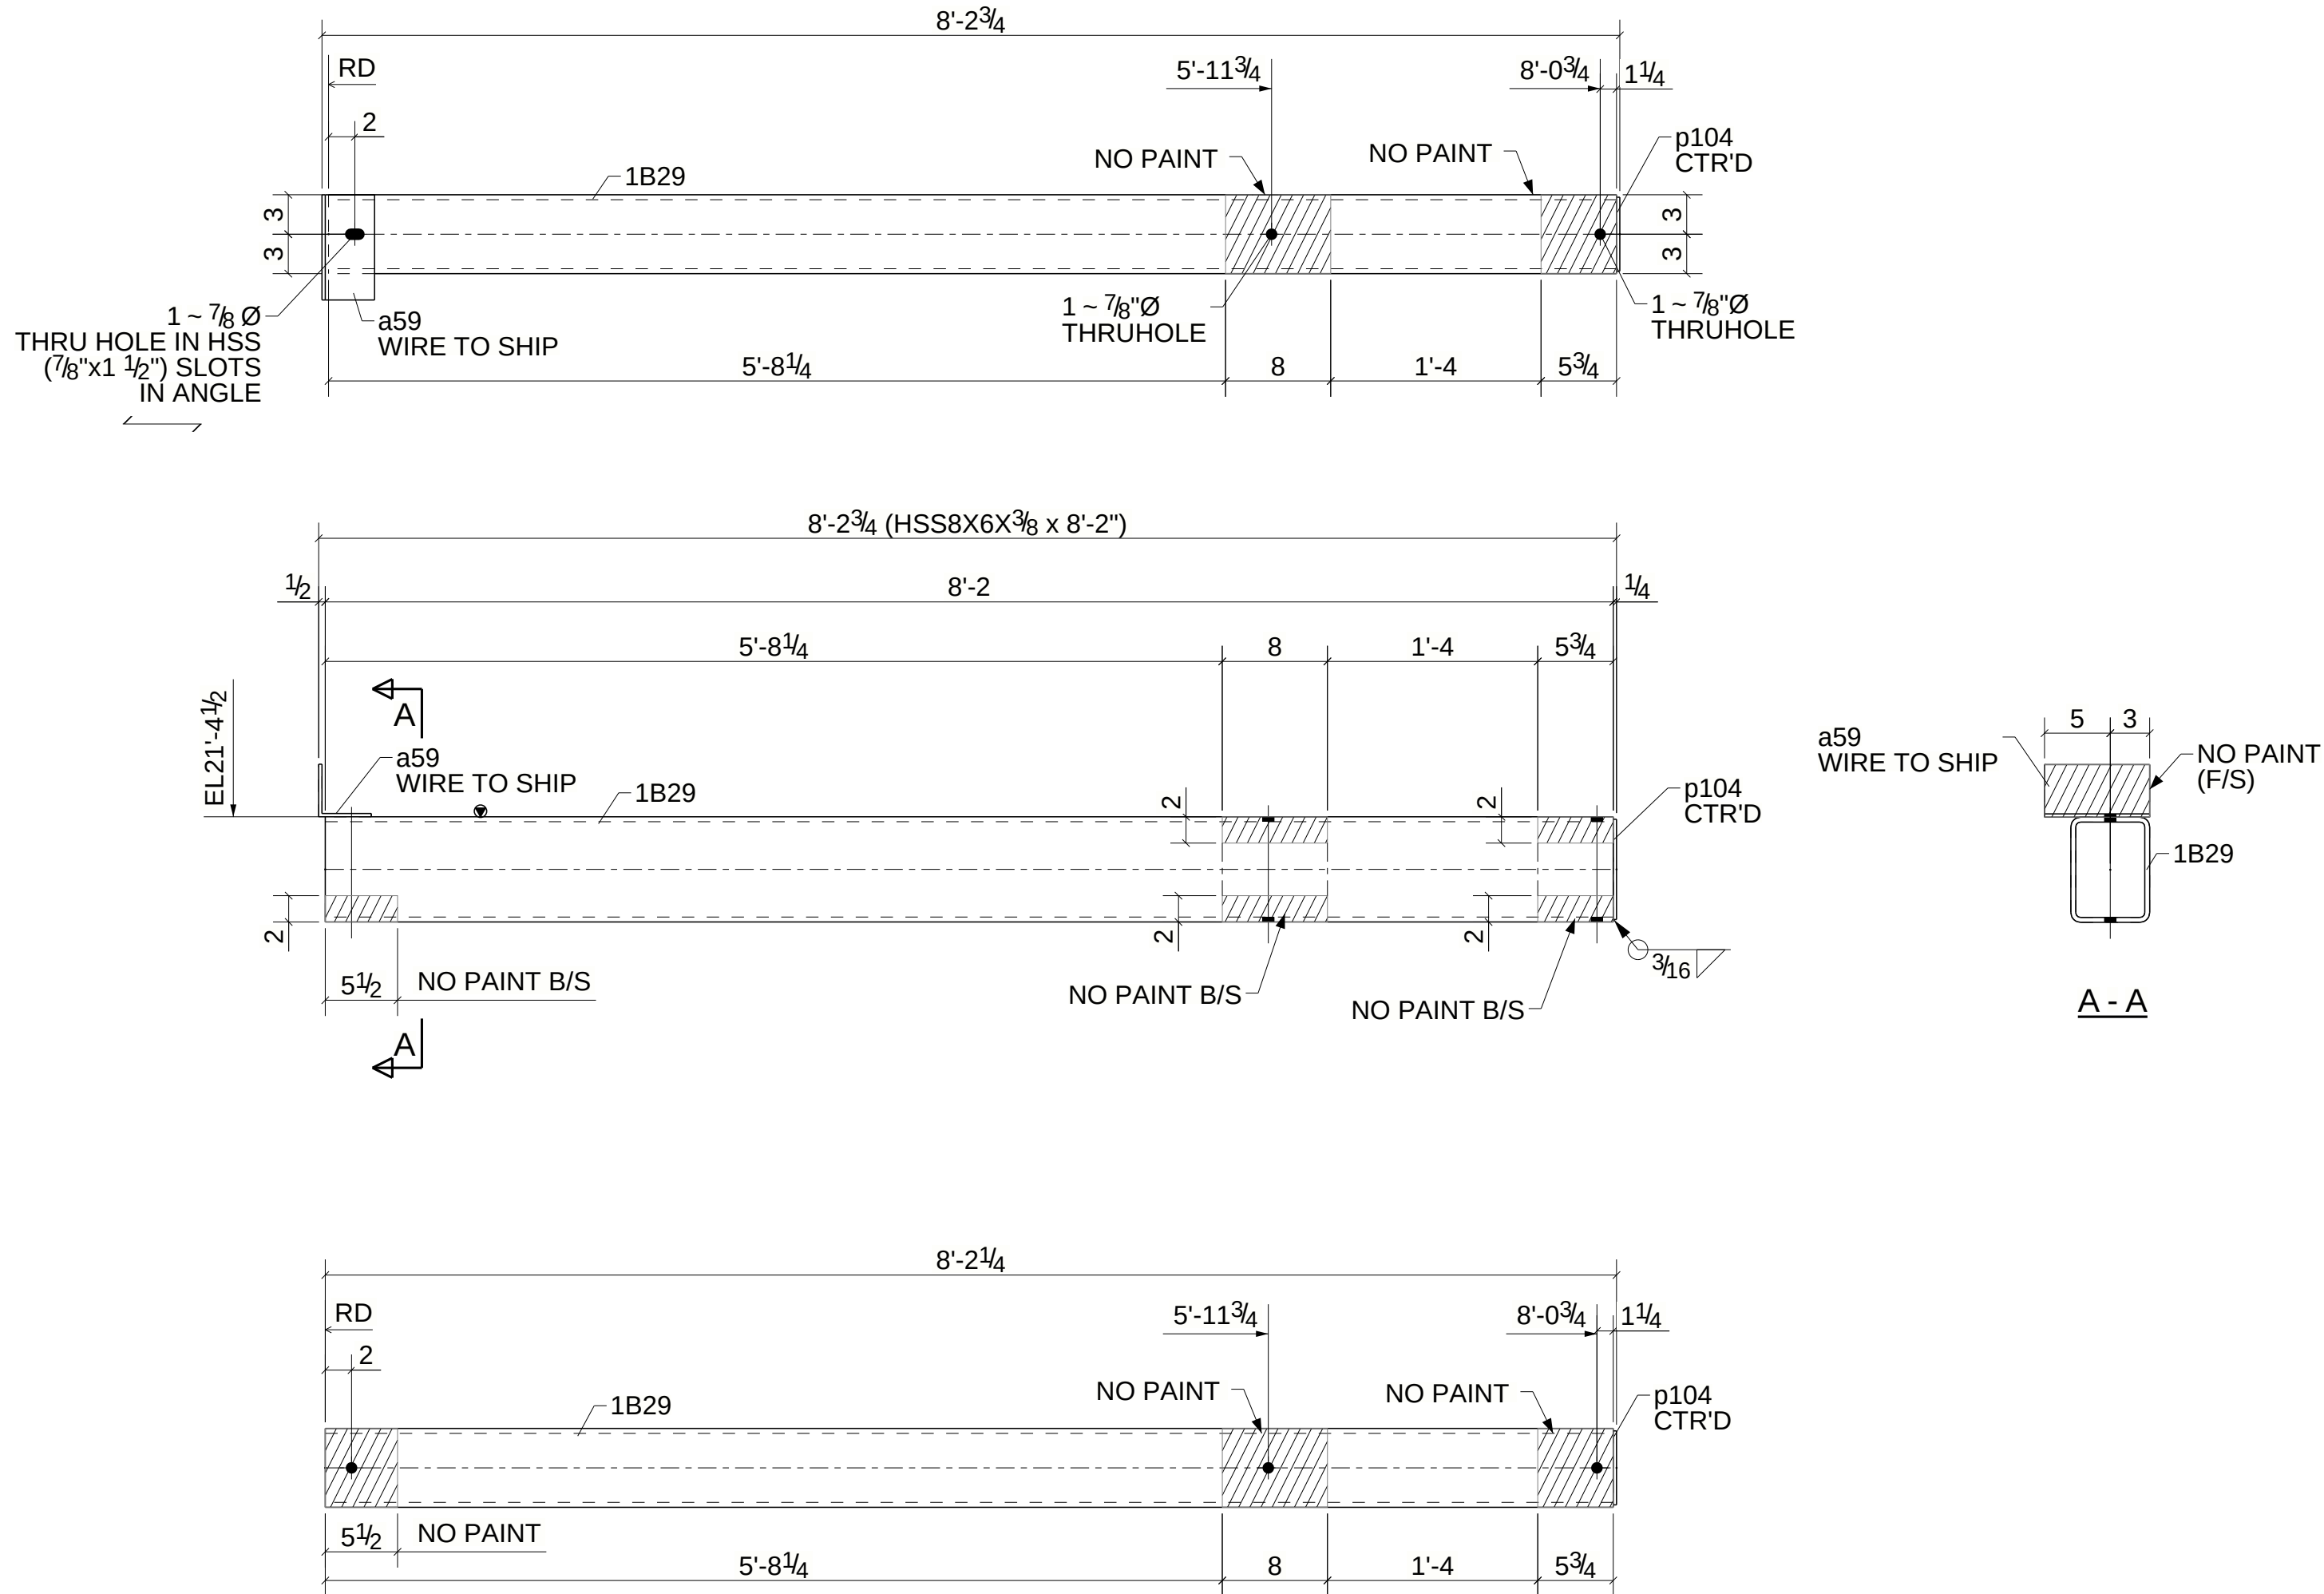

ONE - HSS GIRT - 1B29

0	04/11/2025	For Fabrication
A	10/16/2024	For Approval
REV.	DATE	DESCRIPTION
MATERIAL	A36 UNO	
HOLES	13/16Ø UNO	
WELDS	E70XX	
SURFACE PREP.	SSPC SP2	
PAINT NOTE:	SW SHOP PRIMER	

<