
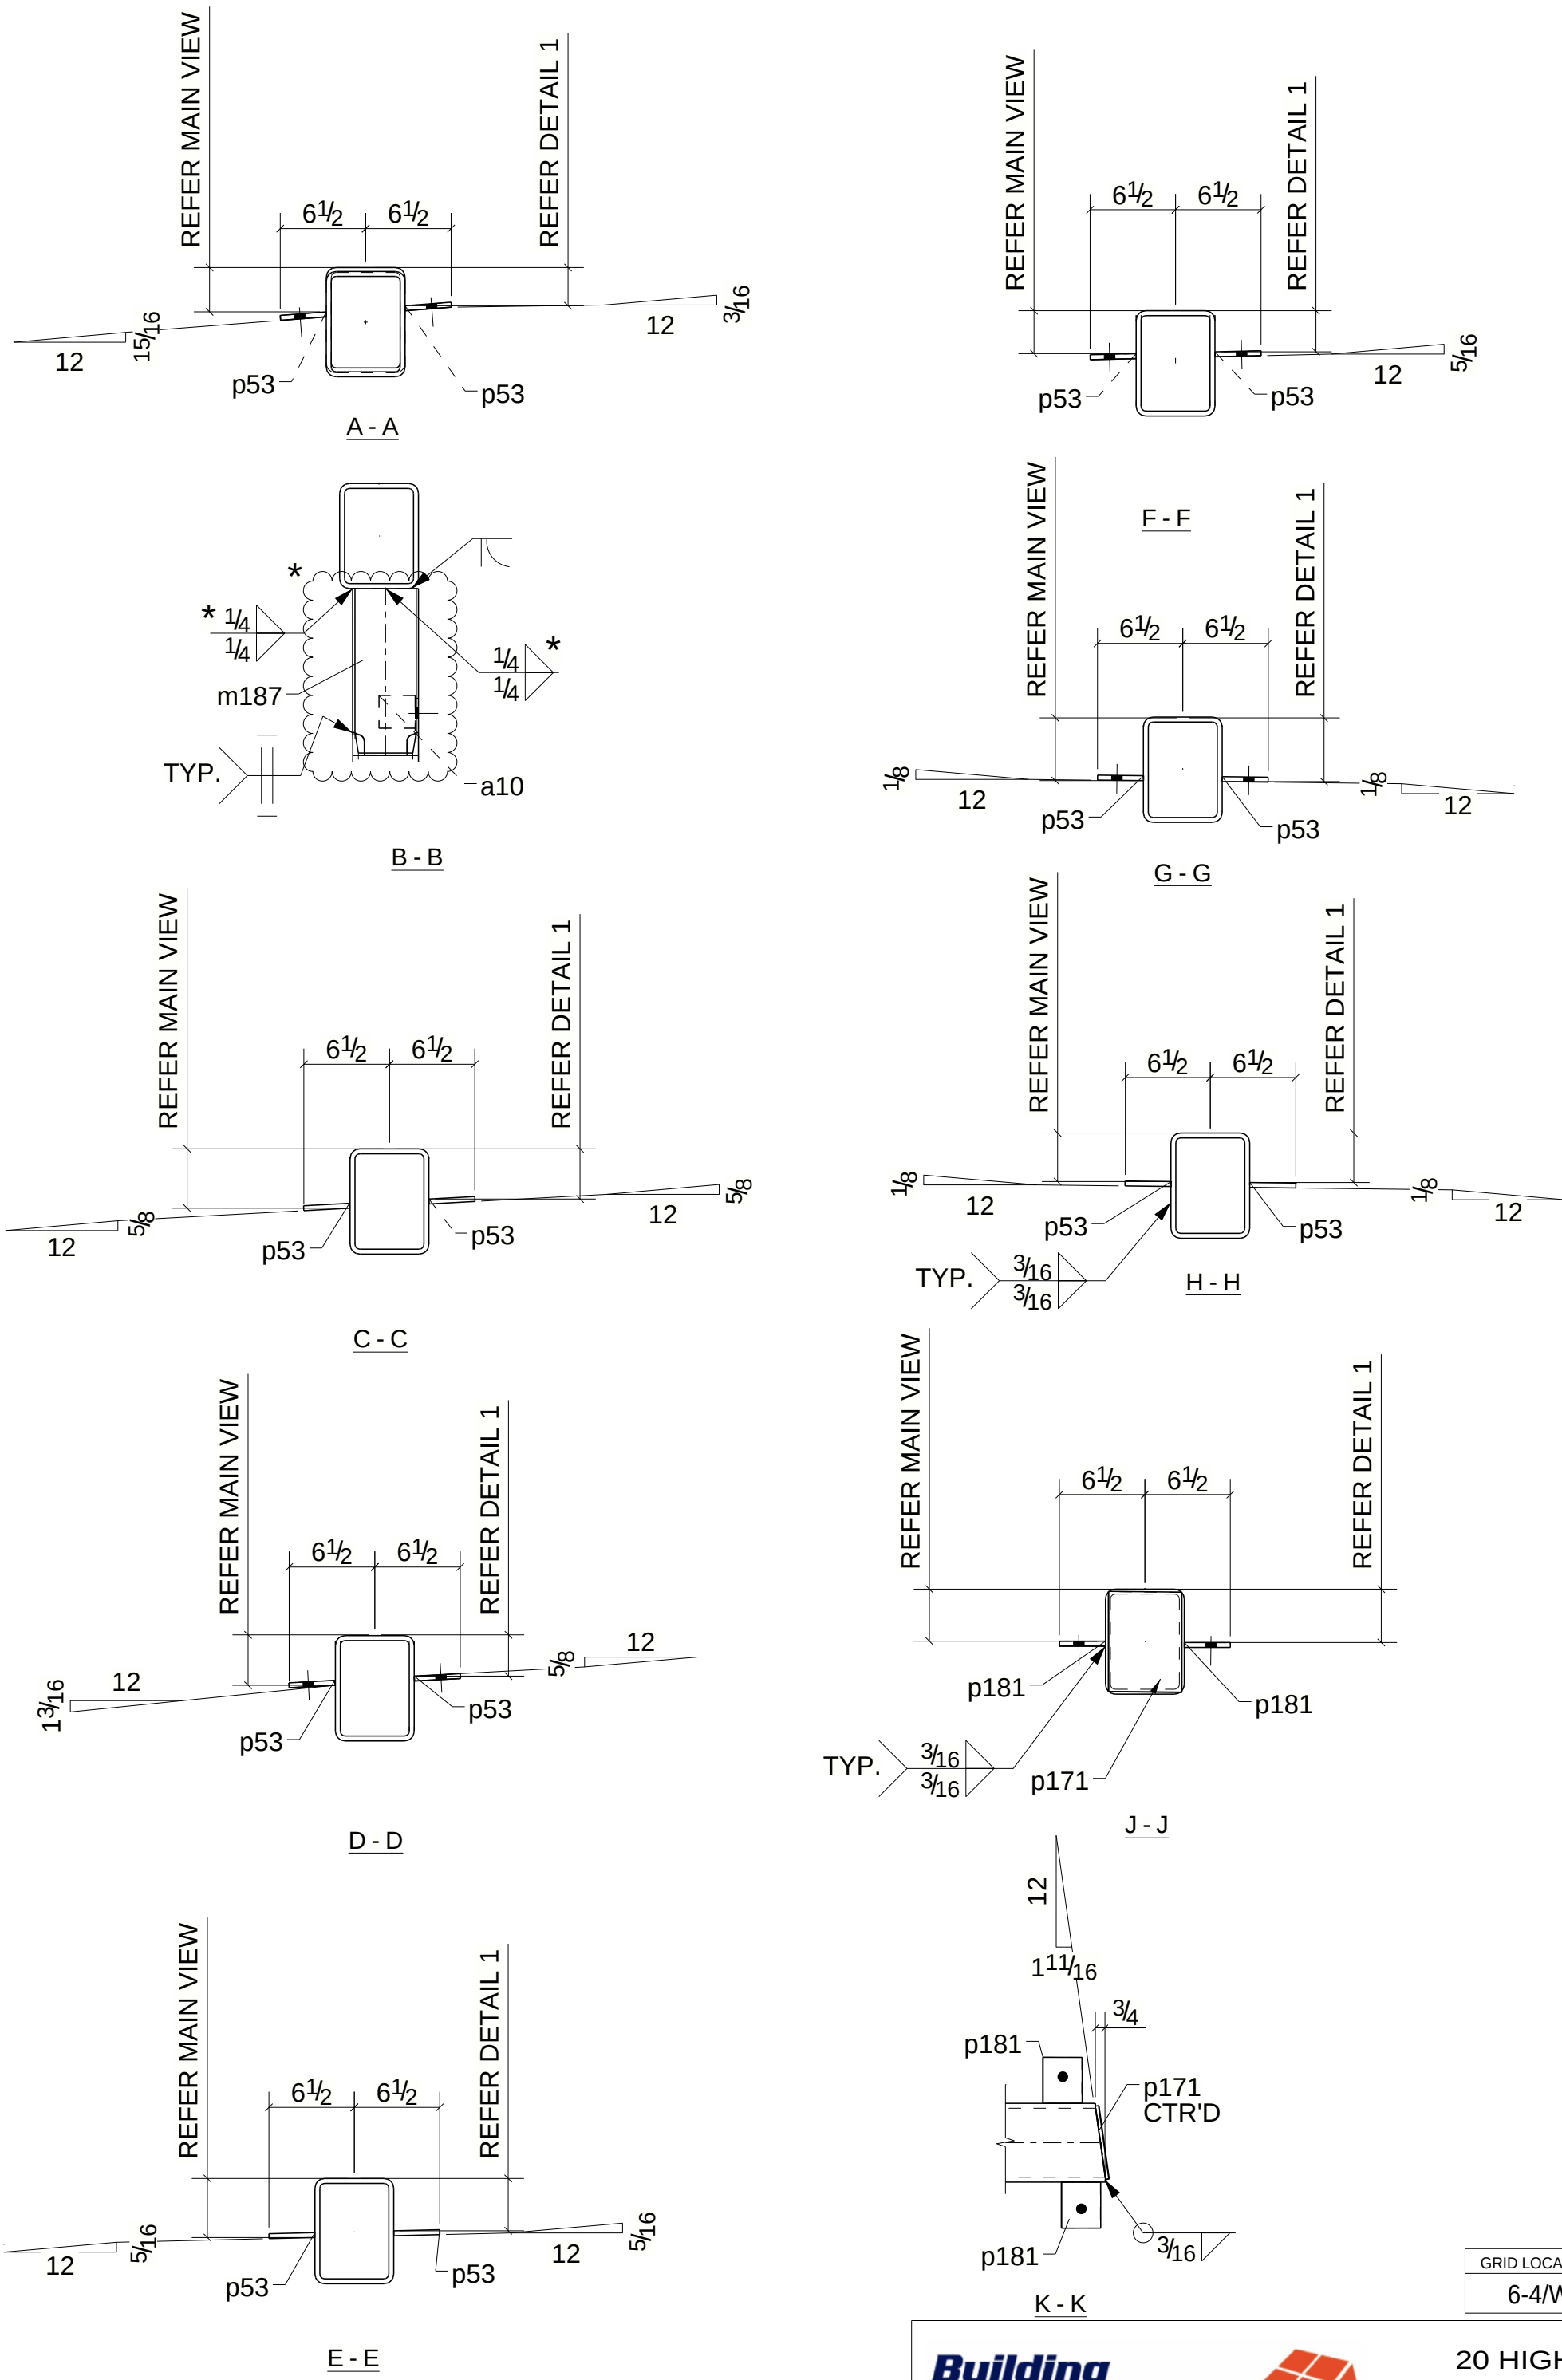


BILL OF MATERIAL							
MARK	TOTAL QTY	SHAPE	LENGTH	TOTAL WEIGHT	REMARKS	ADV MILL #	STEEL GRADE
1B3	1	HSS8X6X3/8	16'-11 11/16"	518	BEV-2 GALV		A500-GR B
a10	2	L3X3X1/4	0'-2 1/2"	2			A36
m187	1	C5X6.7	1'-0 11/16"	7			A36
m188	1	C5X6.7	0'-9 3/4"	5			A36
m189	1	C5X6.7	0'-6 3/4"	4			A36
m190	1	C5X6.7	0'-3 3/4"	2			A36
m191	1	C5X6.7	11'-0"	74			A36
p53	14	PL3/8"X3"	0'-3 1/2"	16			A36
p171	1	PL1/4"X5 5/8"	0'-7 5/8"	3			A36
p181	2	PL3/8"X3"	0'-3 1/2"	2			A36

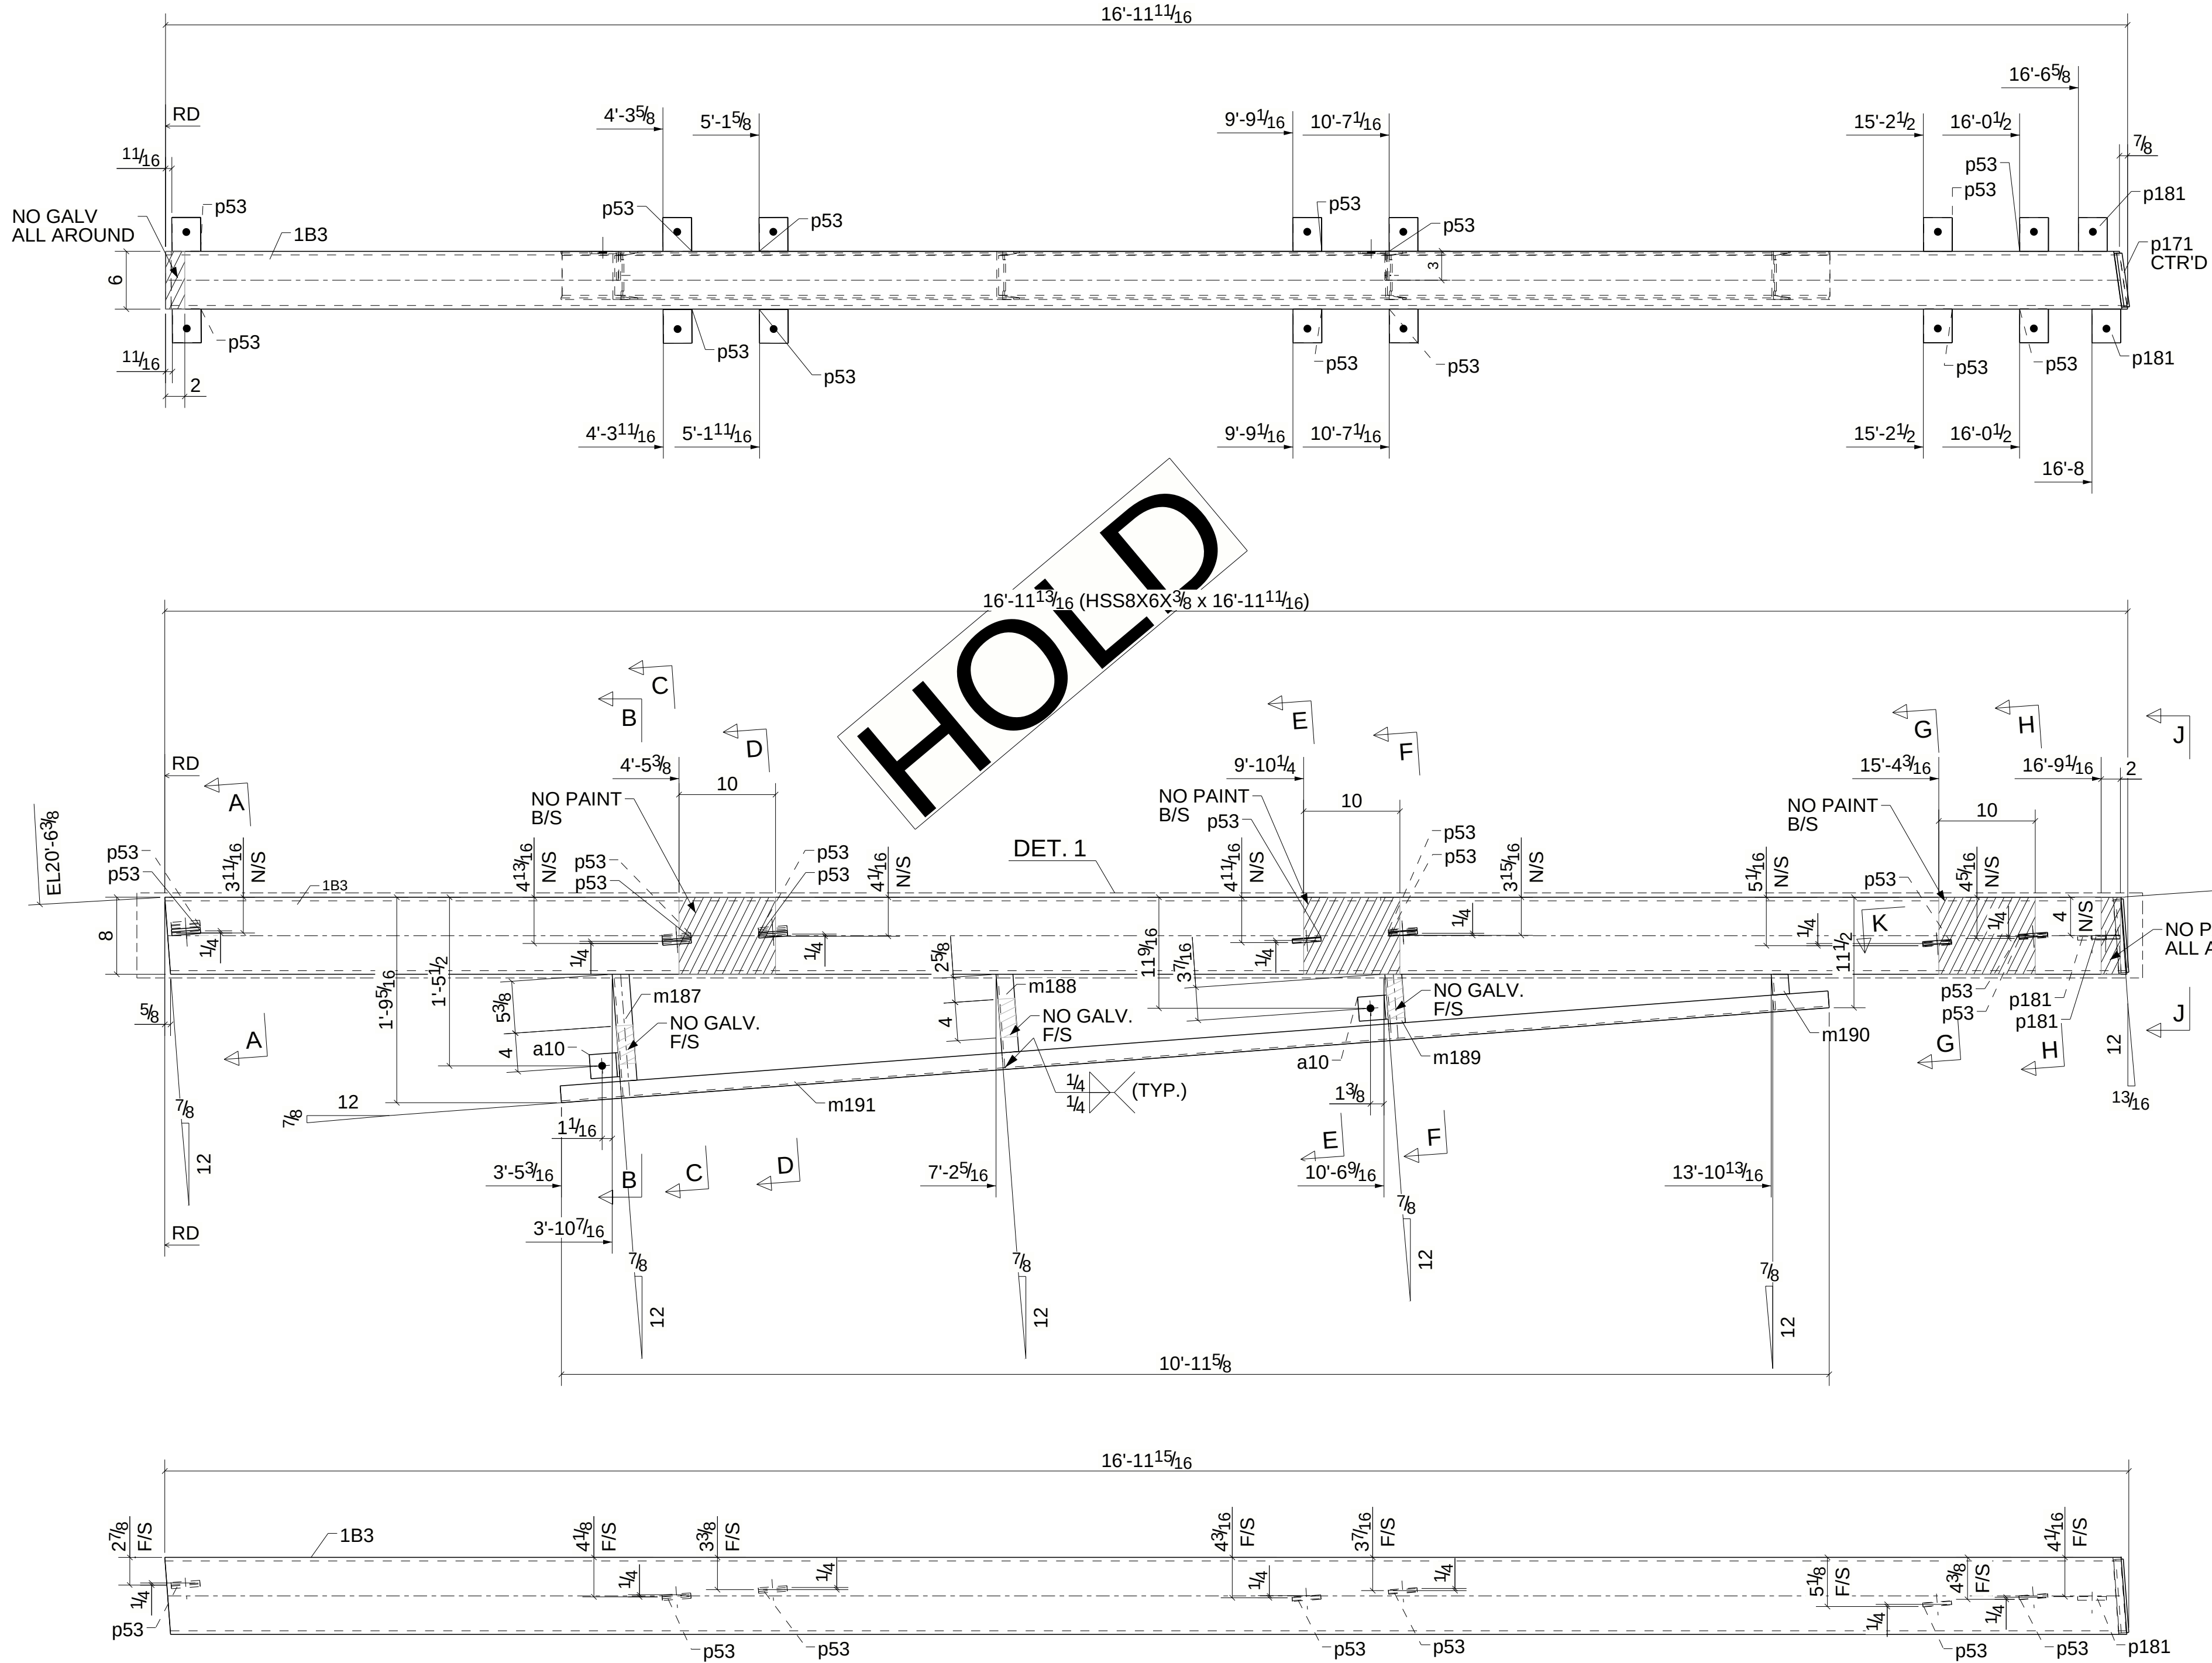

SHOP NOTE:
* CLOUDED PORTION OF STEELS NEED TO BE GALV. SEPARATELY BEFORE WELDING WITH THE HSS BEAM.

FABRICATOR NOTE:
NO GALV. & MASK HATCHED PORTION WITH TWO PART OF EPOXY BEFORE GALVANIZATION.

DETAIL-1
OTHER PARTS NOT SHOWN FOR CLARITY

ONE - BEAM - 1B3

0	04/11/2025	For Fabrication
B	03/24/2025	For Re Approval
A	10/16/2024	For Approval
REV.	DATE	DESCRIPTION
MATERIAL A36 UNO		
HOLES 13/160 UNO		
WELDS E70XX		
SURFACE PREP. SSPC SP2		
PAINT NOTE: SW SHOP PRIMER (U.N.O)		

p181

261

<