


BILL OF MATERIAL							
MARK	TOTAL QTY	SHAPE	LENGTH	TOTAL WEIGHT	REMARKS	ADV MILL #	STEEL GRADE
1B30	1	HSS8X4X1/4	27'-0 7/8"	483	SQ-2		A500-GR B
p137	1	PL1/4"X3 5/8"	0'-7 5/8"	2			A36

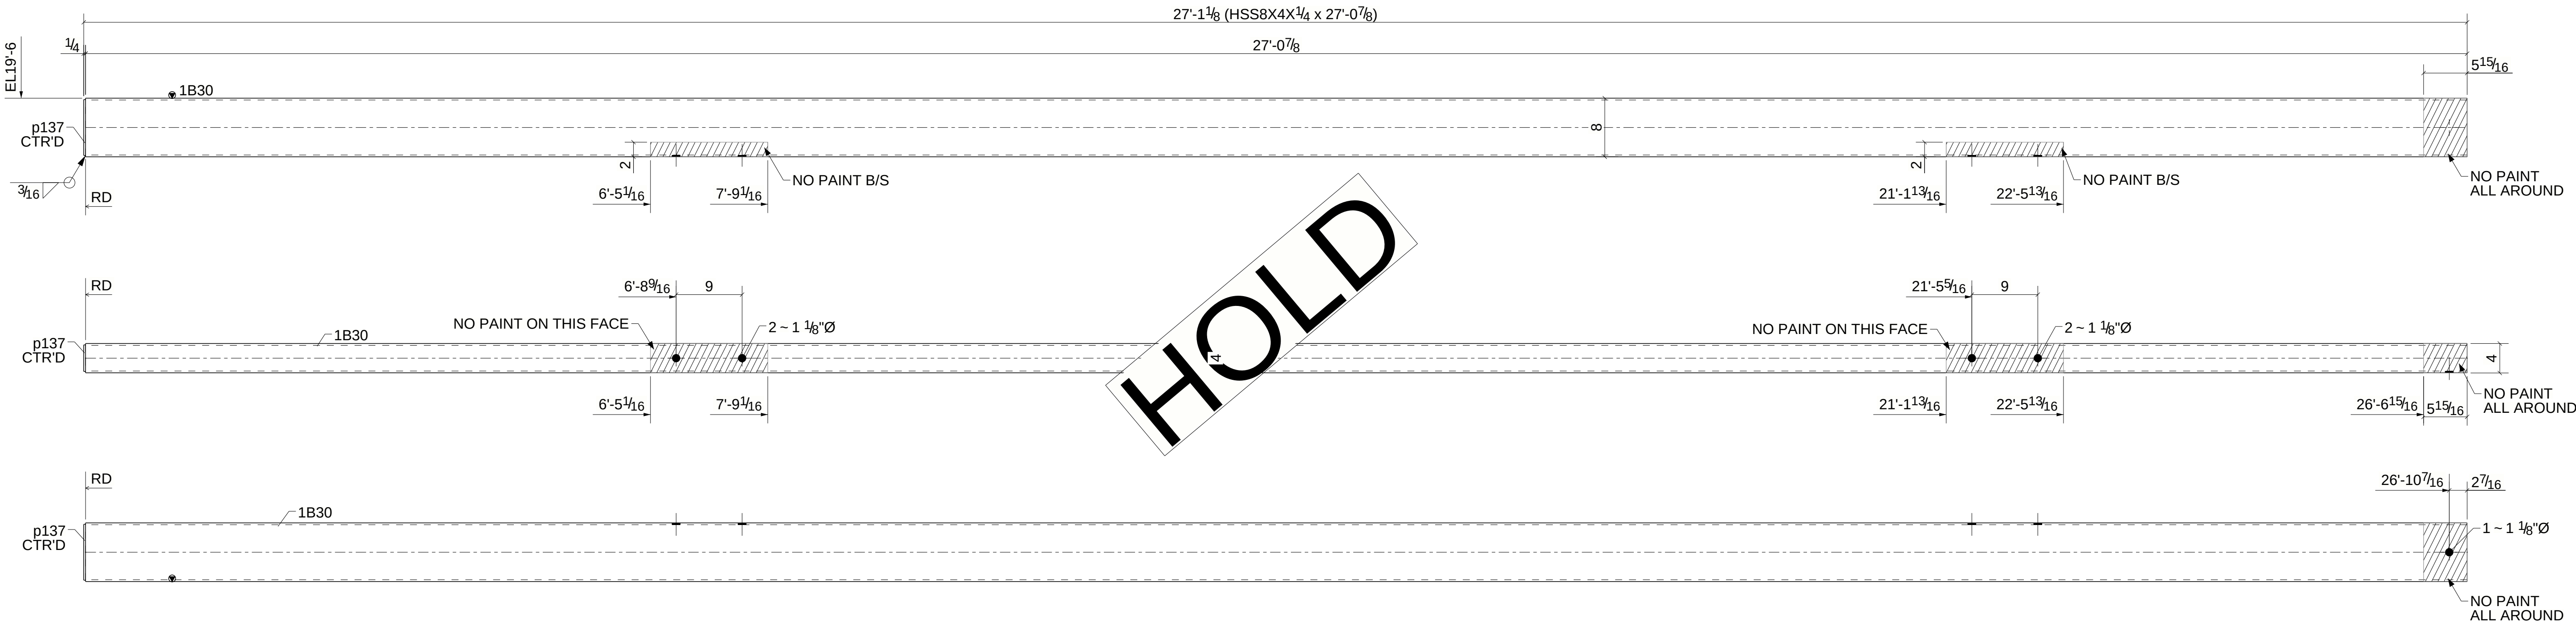

ONE - HSS GIRT - 1B30

0	04/11/2025	For Fabrication
A	10/16/2024	For Approval
REV.	DATE	DESCRIPTION
MATERIAL A36 UNO		
HOLES 13/16Ø UNO		
WELDS E70XX		
SURFACE PREP. SSPC SP2		
PAINT NOTE: SW SHOP PRIMER		