

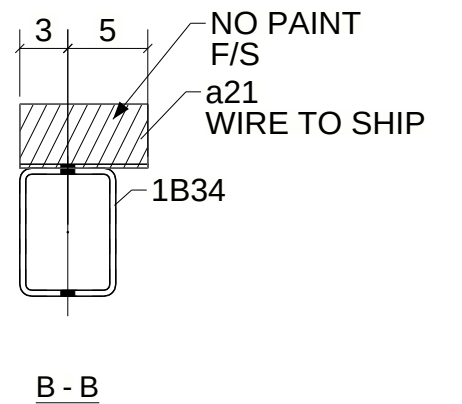
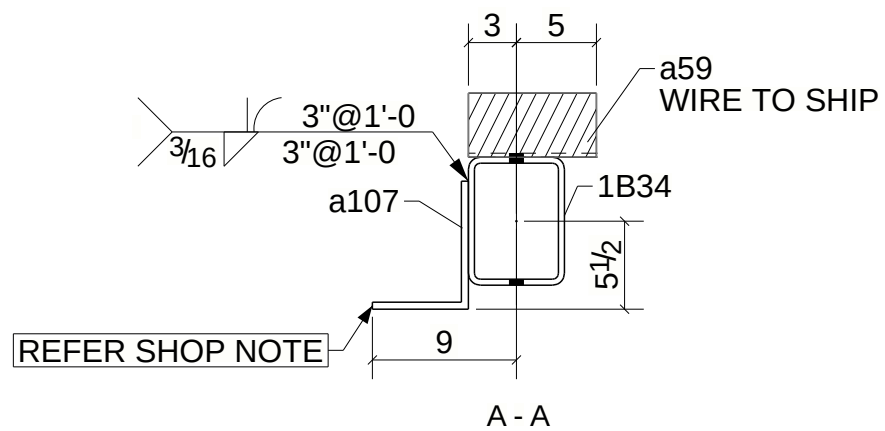
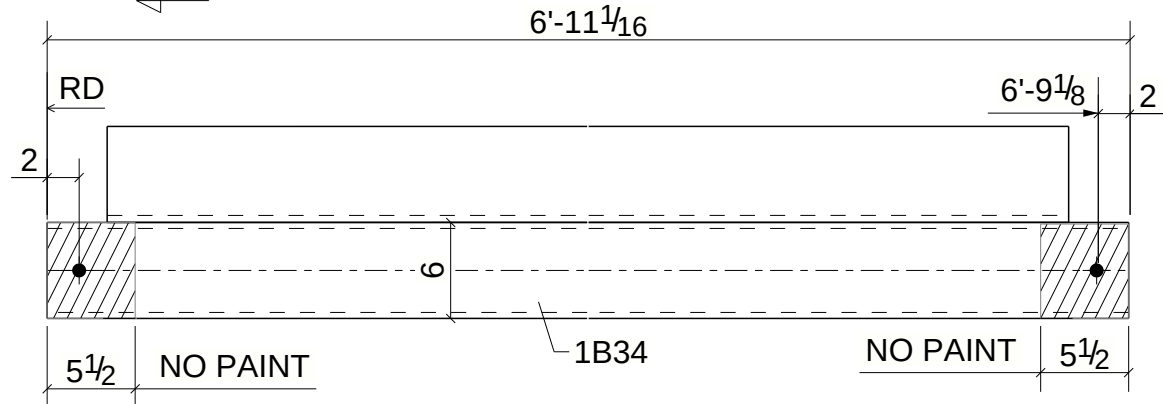


Tekla Structures

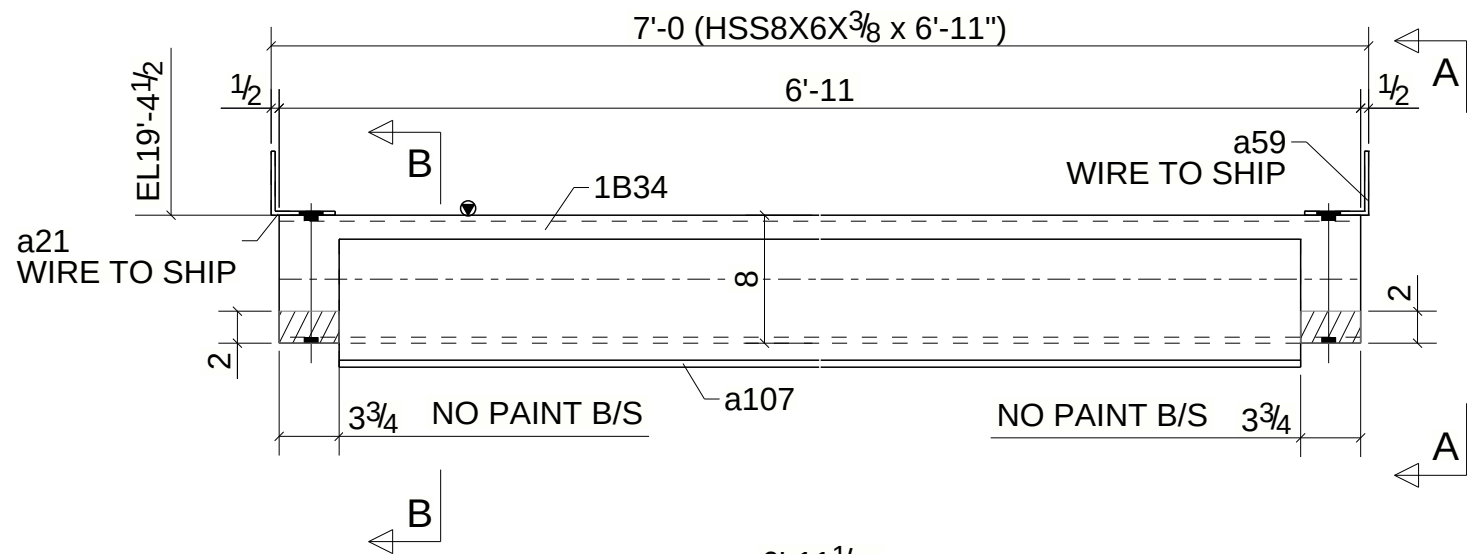

SHOP NOTE:
1. SHELF ANGLE SHOULD BE GALV. SEPERATELY BEFORE WELDING TO HSS.(SURFACE PREP : SSPC-SP3

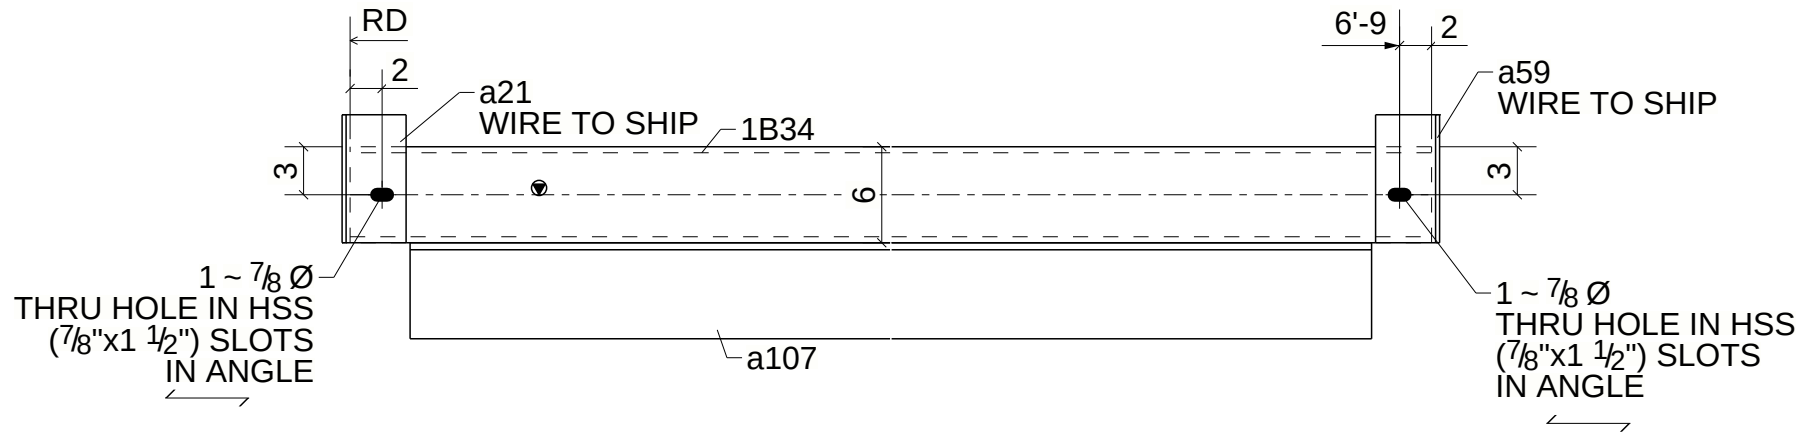

20 HIGH STREET
PLAINSVILLE, MA 02762
PHONE (508) 381-0429
www.teambes.com

0	04/11/2025	For Fabrication	PROJECT NAME			
A	10/16/2024	For Approval	GSC JUNIPER RBP PHASE-II			
REV.	DATE	DESCRIPTION	LOCATION			
MATERIAL A36 UNO			PARKWAY EVERETT, MA			
HOLES 13/16 Ø UNO			CONTRACTOR			
WELDS E70XX			BUILDING ENVELOPE SYSTEMS			
SURFACE PREP. SSPC SP2			DWG TITLE			
PAINT NOTE : SW SHOP PRIMER			HSS GIRT			
			DRAWN BY ABJ	CHECKED BY HSR	DATE DRAWN 10/15/2024	PLOT DATE 10/15/2024
			CONTRACT No. 24050		DWG No. 1B34	DGSTS No. --
						REV. 0

BILL OF MATERIAL

MARK	TOTAL QTY	SHAPE	LENGTH	TOTAL WEIGHT	REMARKS	ADV MILL #	STEEL GRADE
1B34	1	HSS8X6X3/8	6'-11"	211	SQ-2		A500-GR.B
a21	1	L4X4X1/4	0'-8"	4			A36
a59	1	L4X4X1/4	0'-8"	4			A36
a107	1	L8X6X7/16	6'-3 1/2"	128	GALV.		A36

ONE - HSS GIRT - 1B34