

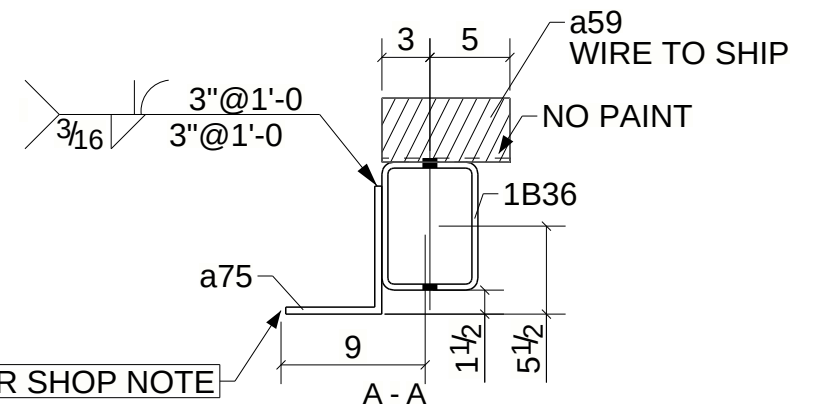
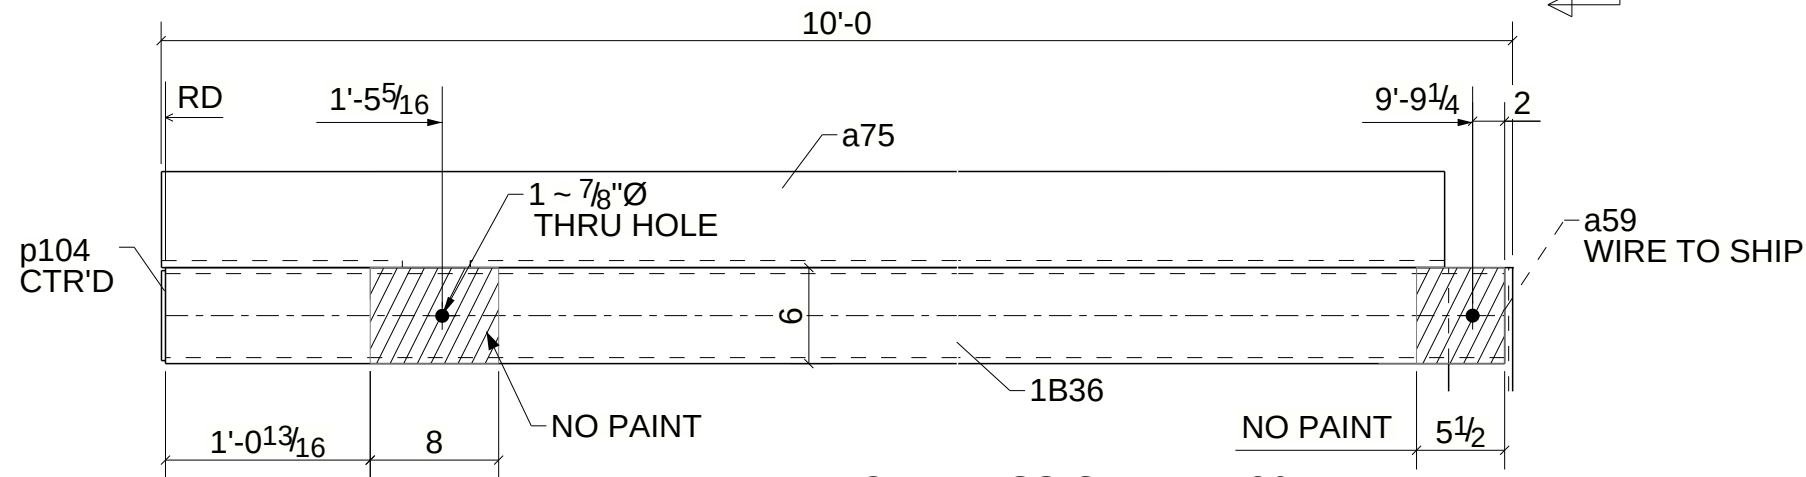


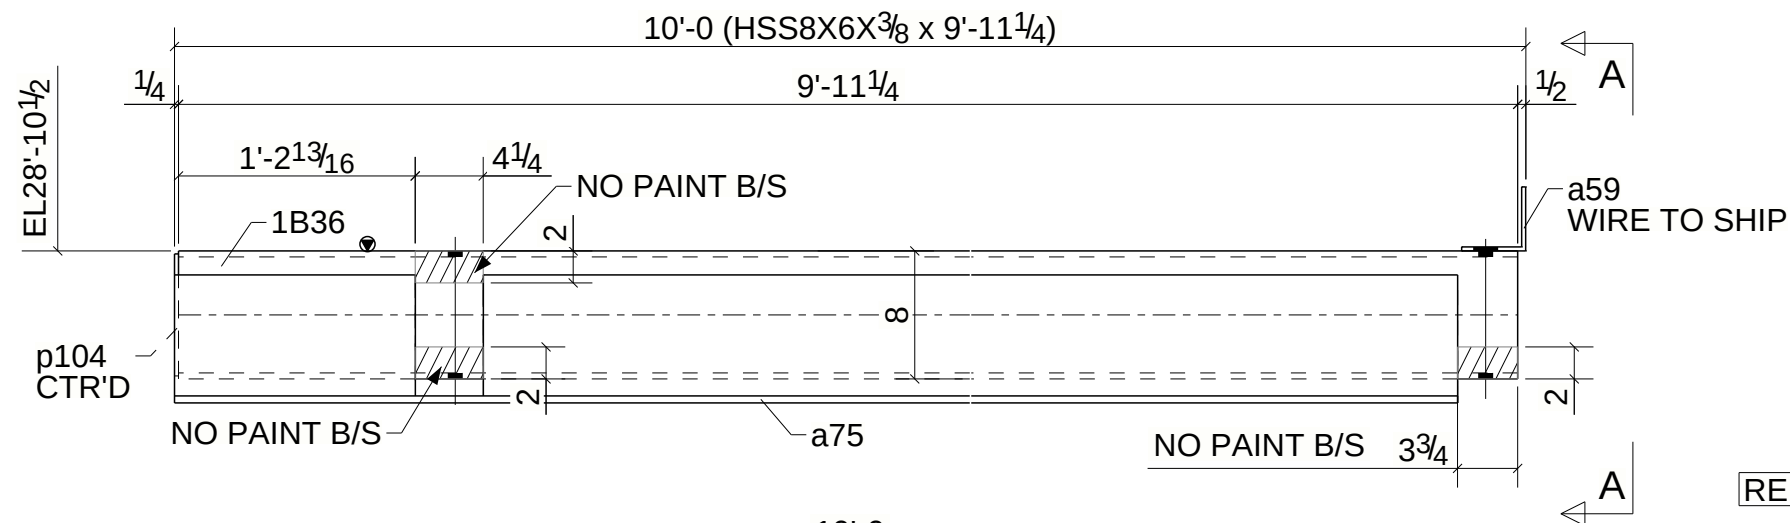

REFER SHOP NOTE

SHOP NOTE:
1. SHELF ANGLE SHOULD BE GALV. SEPERATELY BEFORE WELDING TO HSS.(SURFACE PREP : SSPC-SP3

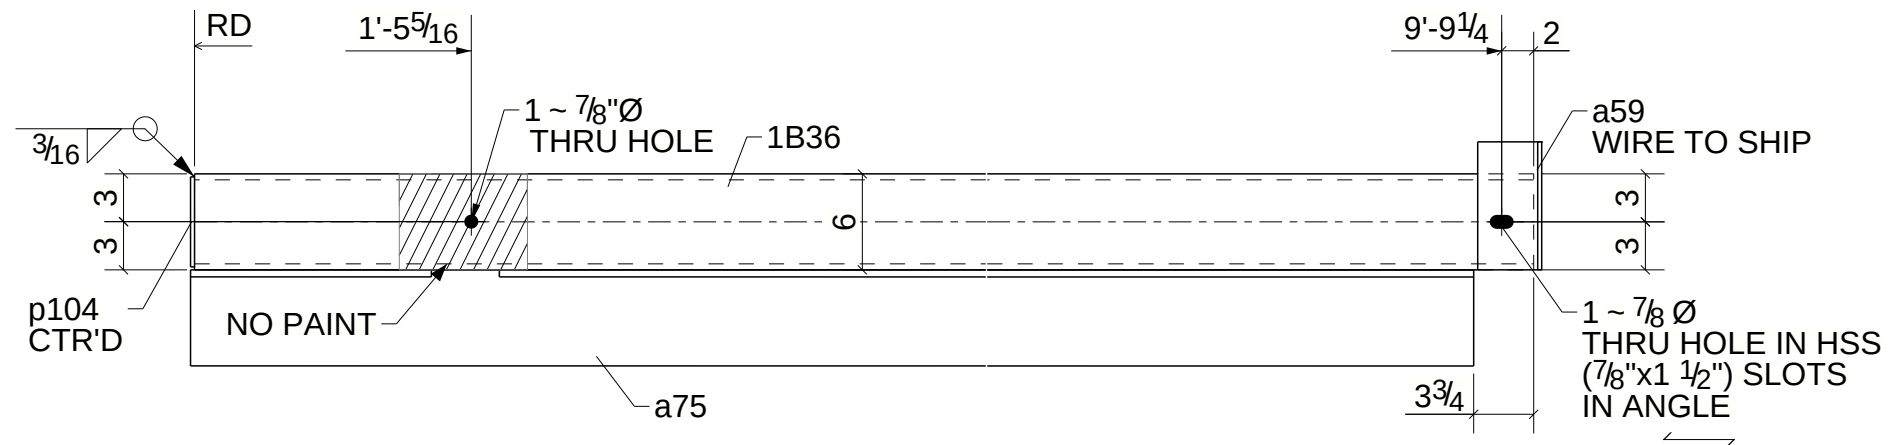

20 HIGH STREET
PLAINSVILLE, MA 02762
PHONE (508) 381-0429
www.teambes.com

BILL OF MATERIAL

MARK	TOTAL QTY	SHAPE	LENGTH	TOTAL WEIGHT	REMARKS	ADV MILL #	STEEL GRADE
1B36	1	HSS8X6X3/8	9'-11 1/4"	303	SQ-2		A500-GR.B
a59	1	L4X4X1/4	0'-8"	4			A36
a75	1	L8X6X7/16	9'-7 3/4"	197	GALV.		A36
p104	1	PL1/4"X5 5/8"	0'-7 5/8"	3			A36

0	04/11/2025	For Fabrication	PROJECT NAME			
A	10/15/2024	For Approval	GSC JUNIPER RBP PHASE-II			
REV.	DATE	DESCRIPTION	LOCATION			
MATERIAL A36 UNO			PARKWAY EVERETT, MA			
HOLES 13/16 Ø UNO			CONTRACTOR			
WELDS E70XX			BUILDING ENVELOPE SYSTEMS			
SURFACE PREP. SSPC SP2			DWG TITLE			
PAINT NOTE : SW SHOP PRIMER (U.N.O)			HSS GIRT			
			DRAWN BY ABJ	CHECKED BY HSR	DATE DRAWN 10/15/2024	PLOT DATE 10/15/2024
			CONTRACT No. 24050		DWG No. 1B36	DGSTS No. --
						REV. 0