


Tekla Structures

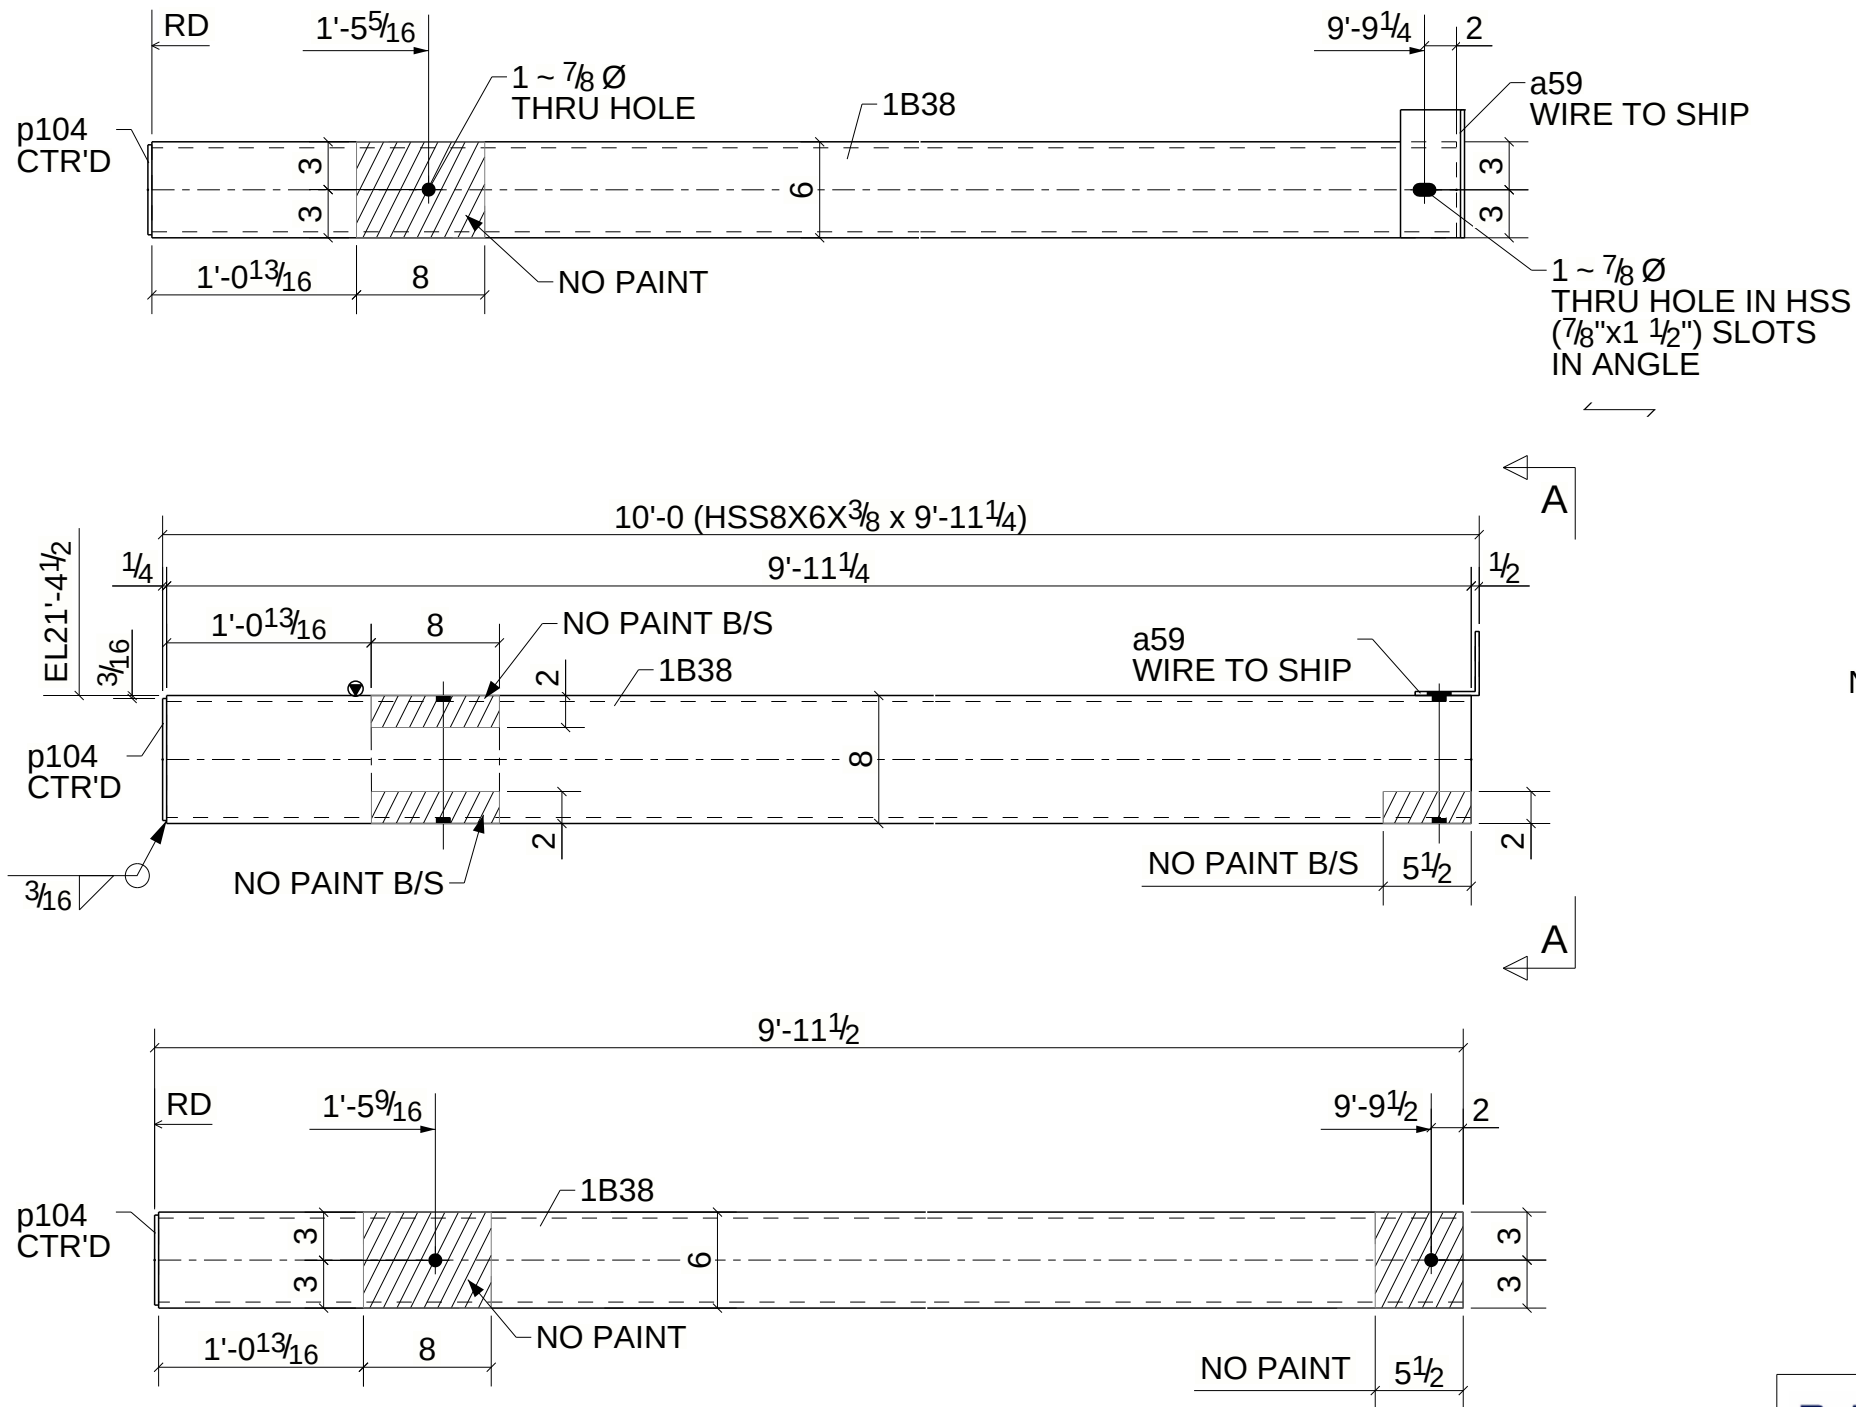

ONE - HSS GIRT - 1B38

BILL OF MATERIAL

MARK	TOTAL QTY	SHAPE	LENGTH	TOTAL WEIGHT	REMARKS	ADV MILL #	STEEL GRADE
1B38	1	HSS8X6X3/8	9'-11 1/4"	303	SQ-2		A500-GR.B
a59	1	L4X4X1/4	0'-8"	4			A36
p104	1	PL1/4"X5 5/8"	0'-7 5/8"	3			A36

0	04/11/2025	For Fabrication
A	10/15/2024	For Approval
REV.	DATE	DESCRIPTION
MATERIAL A36 UNO		
HOLES 13/16 Ø UNO		
WELDS E70XX		
SURFACE PREP. SSPC SP2		
PAINT NOTE : SW SHOP PRIMER		

Building Envelope Systems 		20 HIGH STREET PLAINSVILLE, MA 02762 PHONE (508) 381-0429 www.teambes.com			
PROJECT NAME GSC JUNIPER RBP PHASE-II					
LOCATION PARKWAY EVERETT, MA					
CONTRACTOR BUILDING ENVELOPE SYSTEMS					
DWG TITLE HSS GIRT					
DRAWN BY ABJ		CHECKED BY HSR	DATE DRAWN 10/15/2024	PLOT DATE 10/15/2024	DGSTS No. --
CONTRACT No. 24050			DWG No. 1B38		REV. 0