
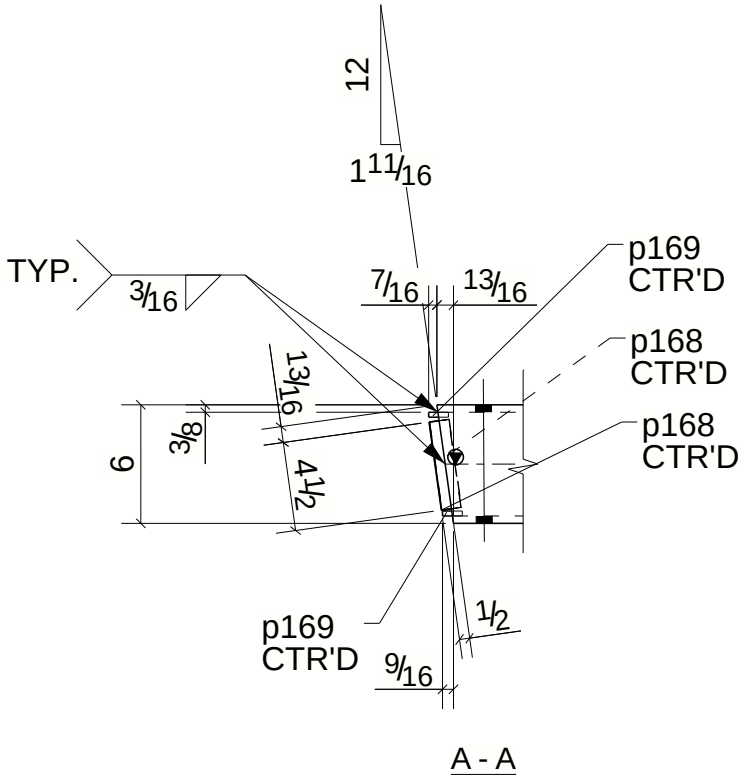


BILL OF MATERIAL							
MARK	TOTAL QTY	SHAPE	LENGTH	TOTAL WEIGHT	REMARKS	ADV MILL #	STEEL GRADE
1B4	1	HSS8X6X3/8	11'-11 15/16"	366	BEV-2 GALV		A500-GR.B
p53	2	PL3/8"X3"	0'-3 1/2"	2			A36
p168	2	PL1/4"X1"	0'-4 1/2"	1			A36
p169	2	PL1/4"X1"	0'-6 1/2"	1			A36
p171	1	PL1/4"X5 5/8"	0'-7 5/8"	3			A36

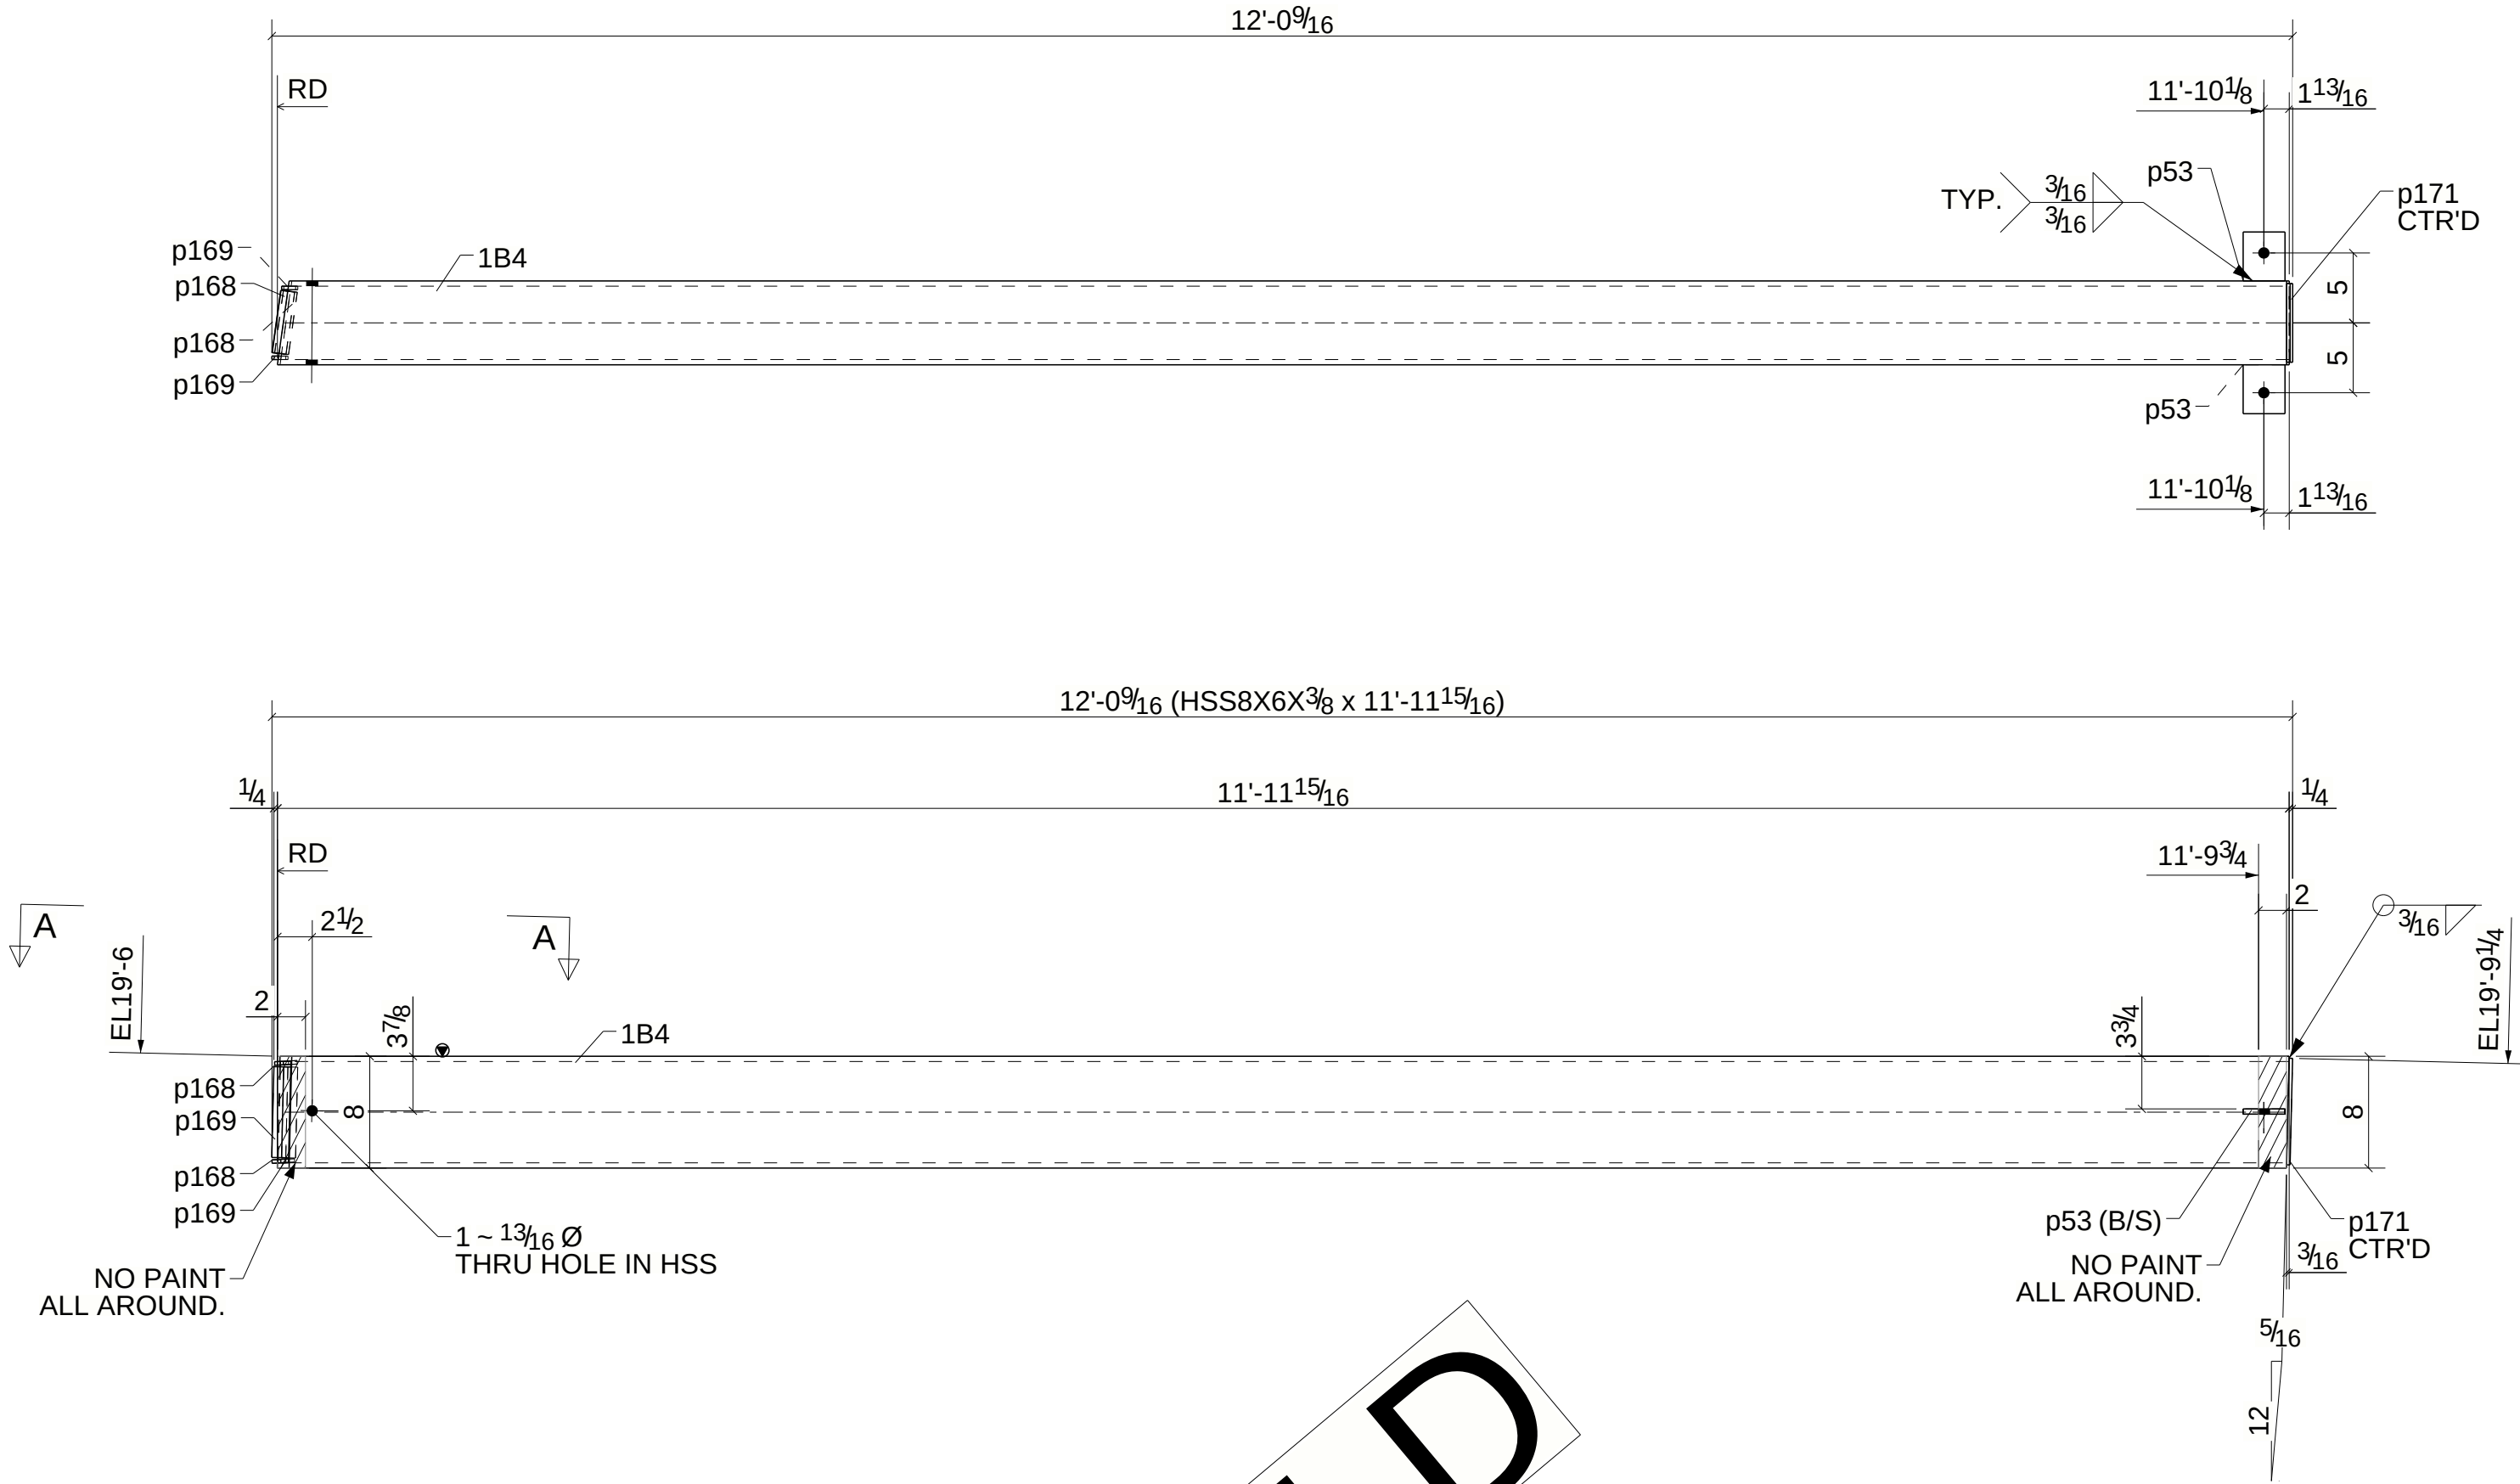

HOLD

ONE - BEAM - 1B4

GRID LOCATION	BOTTOM ELEVATION
6-5/U.5-W	18'-10"

0	04/11/2025	For Fabrication
B	03/24/2025	For Re-Approval
A	10/16/2024	For Approval
REV.	DATE	DESCRIPTION
MATERIAL A36 UNO		
HOLES 13/16 Ø UNO		
WELDS E70XX		
SURFACE PREP. SSPC SP2		
PAINT NOTE SW SHOP PRIMER		

<