
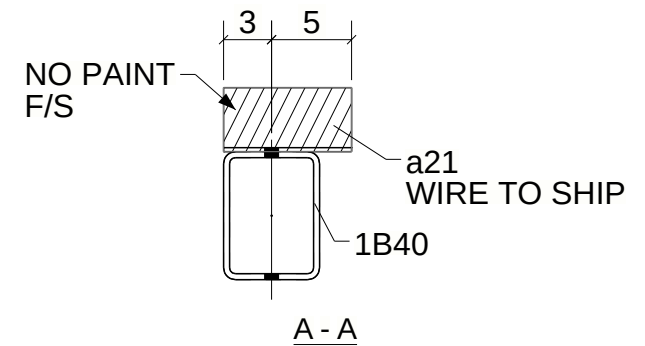


Tekla Structures

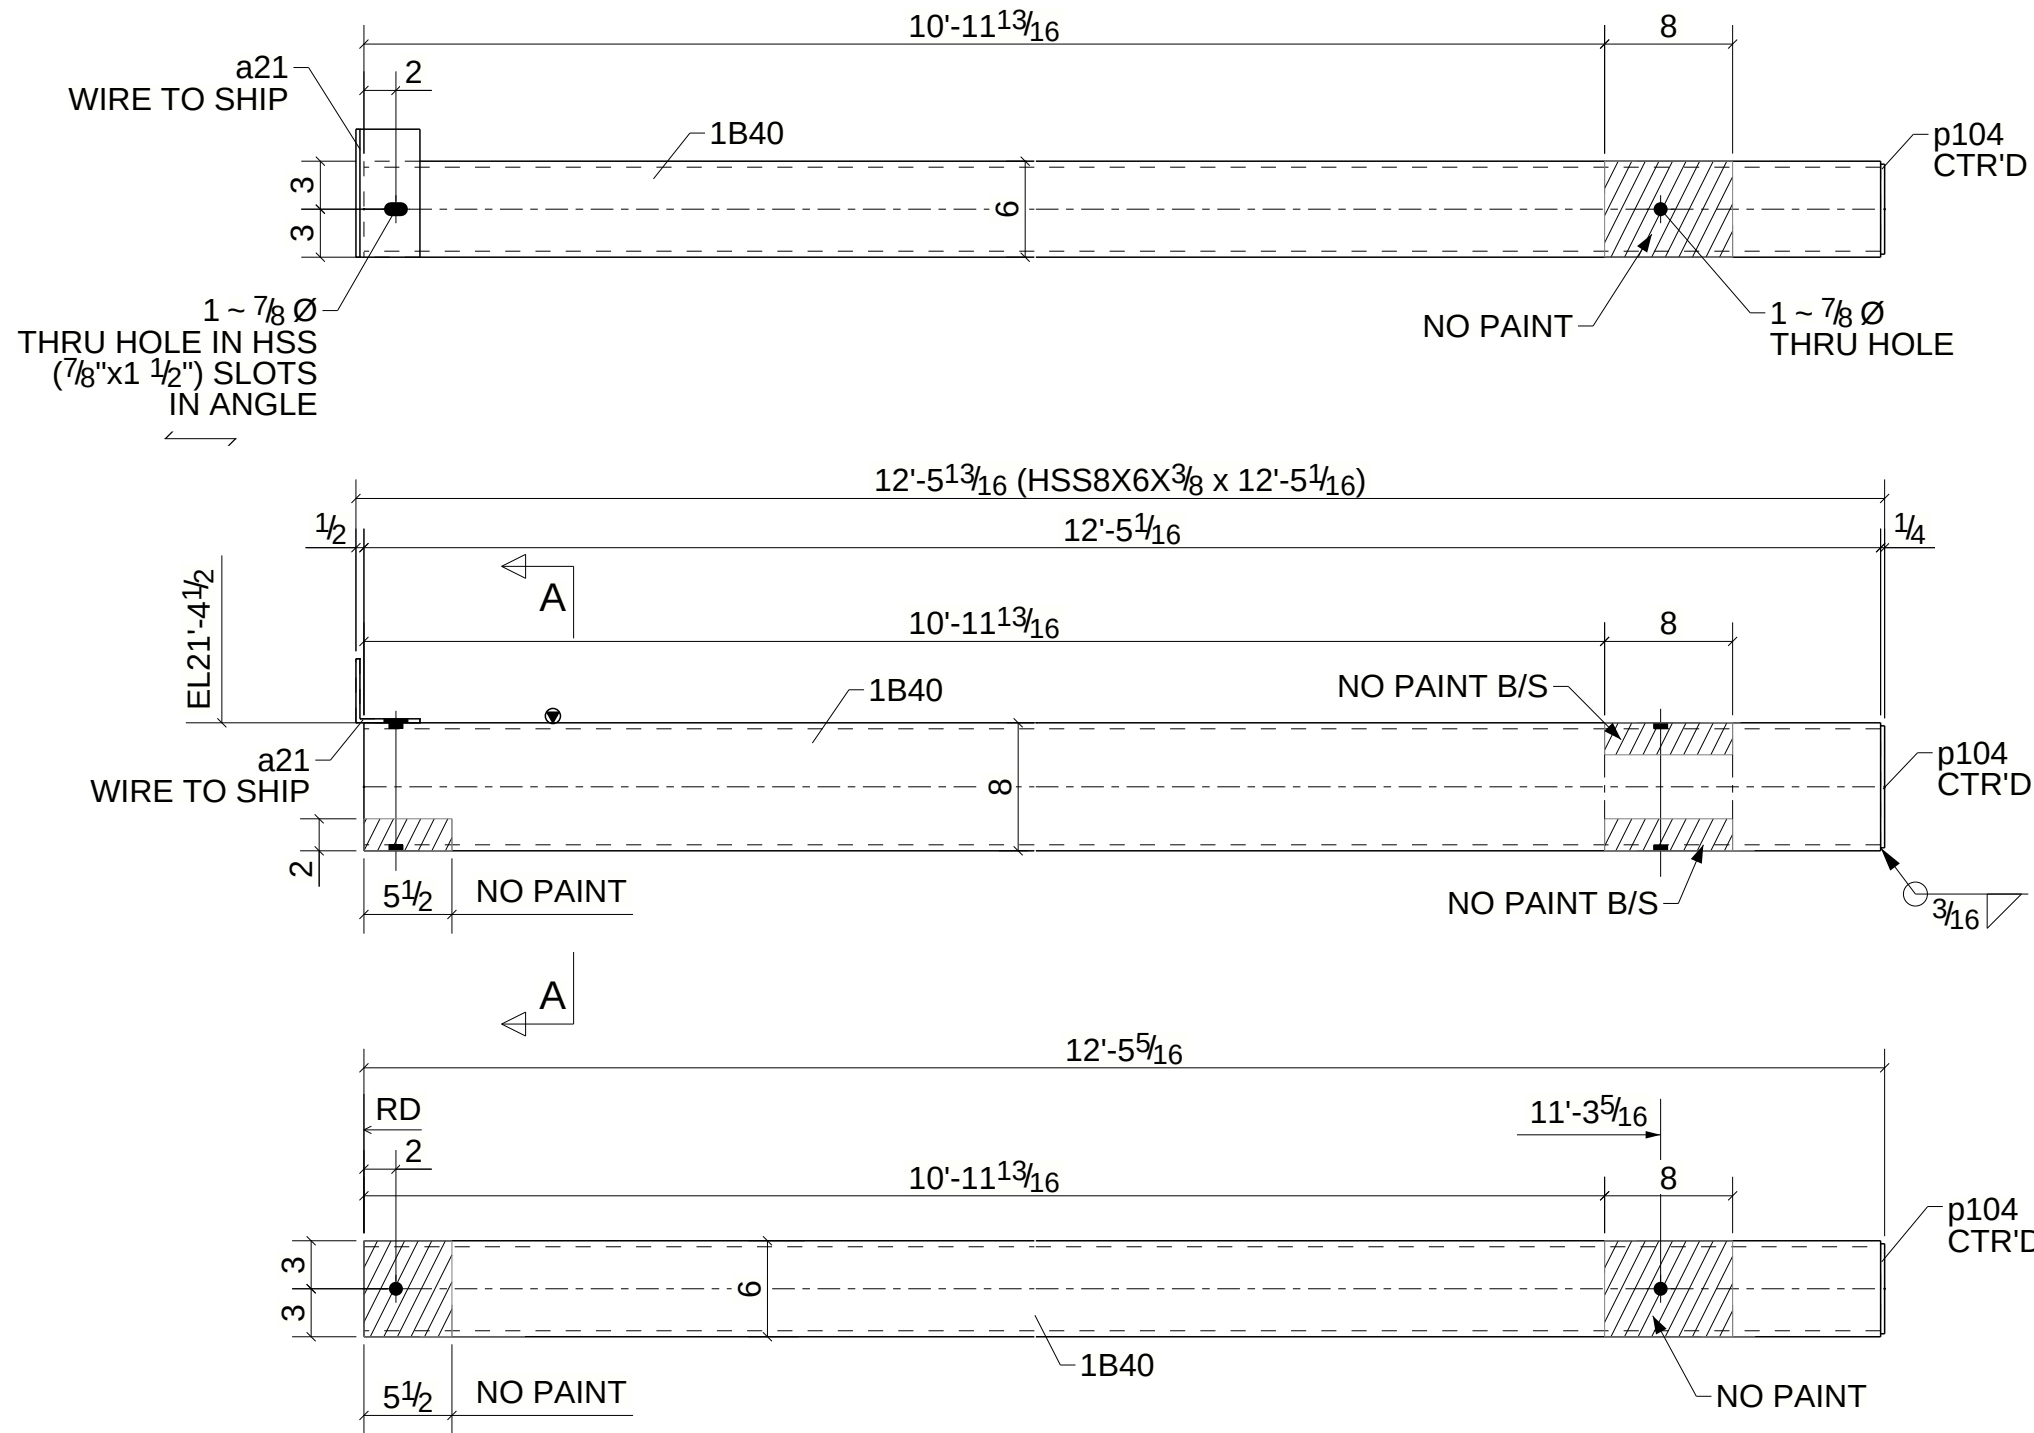

ONE - HSS GIRT - 1B40

BILL OF MATERIAL

MARK	TOTAL QTY	SHAPE	LENGTH	TOTAL WEIGHT	REMARKS	ADV MILL #	STEEL GRADE
1B40	1	HSS8X6X3/8	12'-5 1/16"	379	SQ-2		A500-GR.B
a21	1	L4X4X1/4	0'-8"	4			A36
p104	1	PL1/4"X5 5/8"	0'-7 5/8"	3			A36

0	04/11/2025	For Fabrication
A	10/15/2024	For Approval
REV.	DATE	DESCRIPTION
MATERIAL A36 UNO		
HOLES 13/16Ø UNO		
WELDS E70XX		
SURFACE PREP. SSPC SP2		
PAINT NOTE : SW SHOP PRIMER		
PROJECT NAME GSC JUNIPER RBP PHASE-II		
LOCATION PARKWAY EVERETT, MA		
CONTRACTOR BUILDING ENVELOPE SYSTEMS		
DWG TITLE HSS GIRT		
DRAWN BY ABJ	CHECKED BY HSR	DATE DRAWN 10/15/2024
PLOT DATE 10/15/2024	DGSTS No. --	REV. 0
CONTRACT No. 24050		DWG No. 1B40



20 HIGH STREET
PLAINSVILLE, MA 02762
PHONE (508) 381-0429
www.teambes.com