



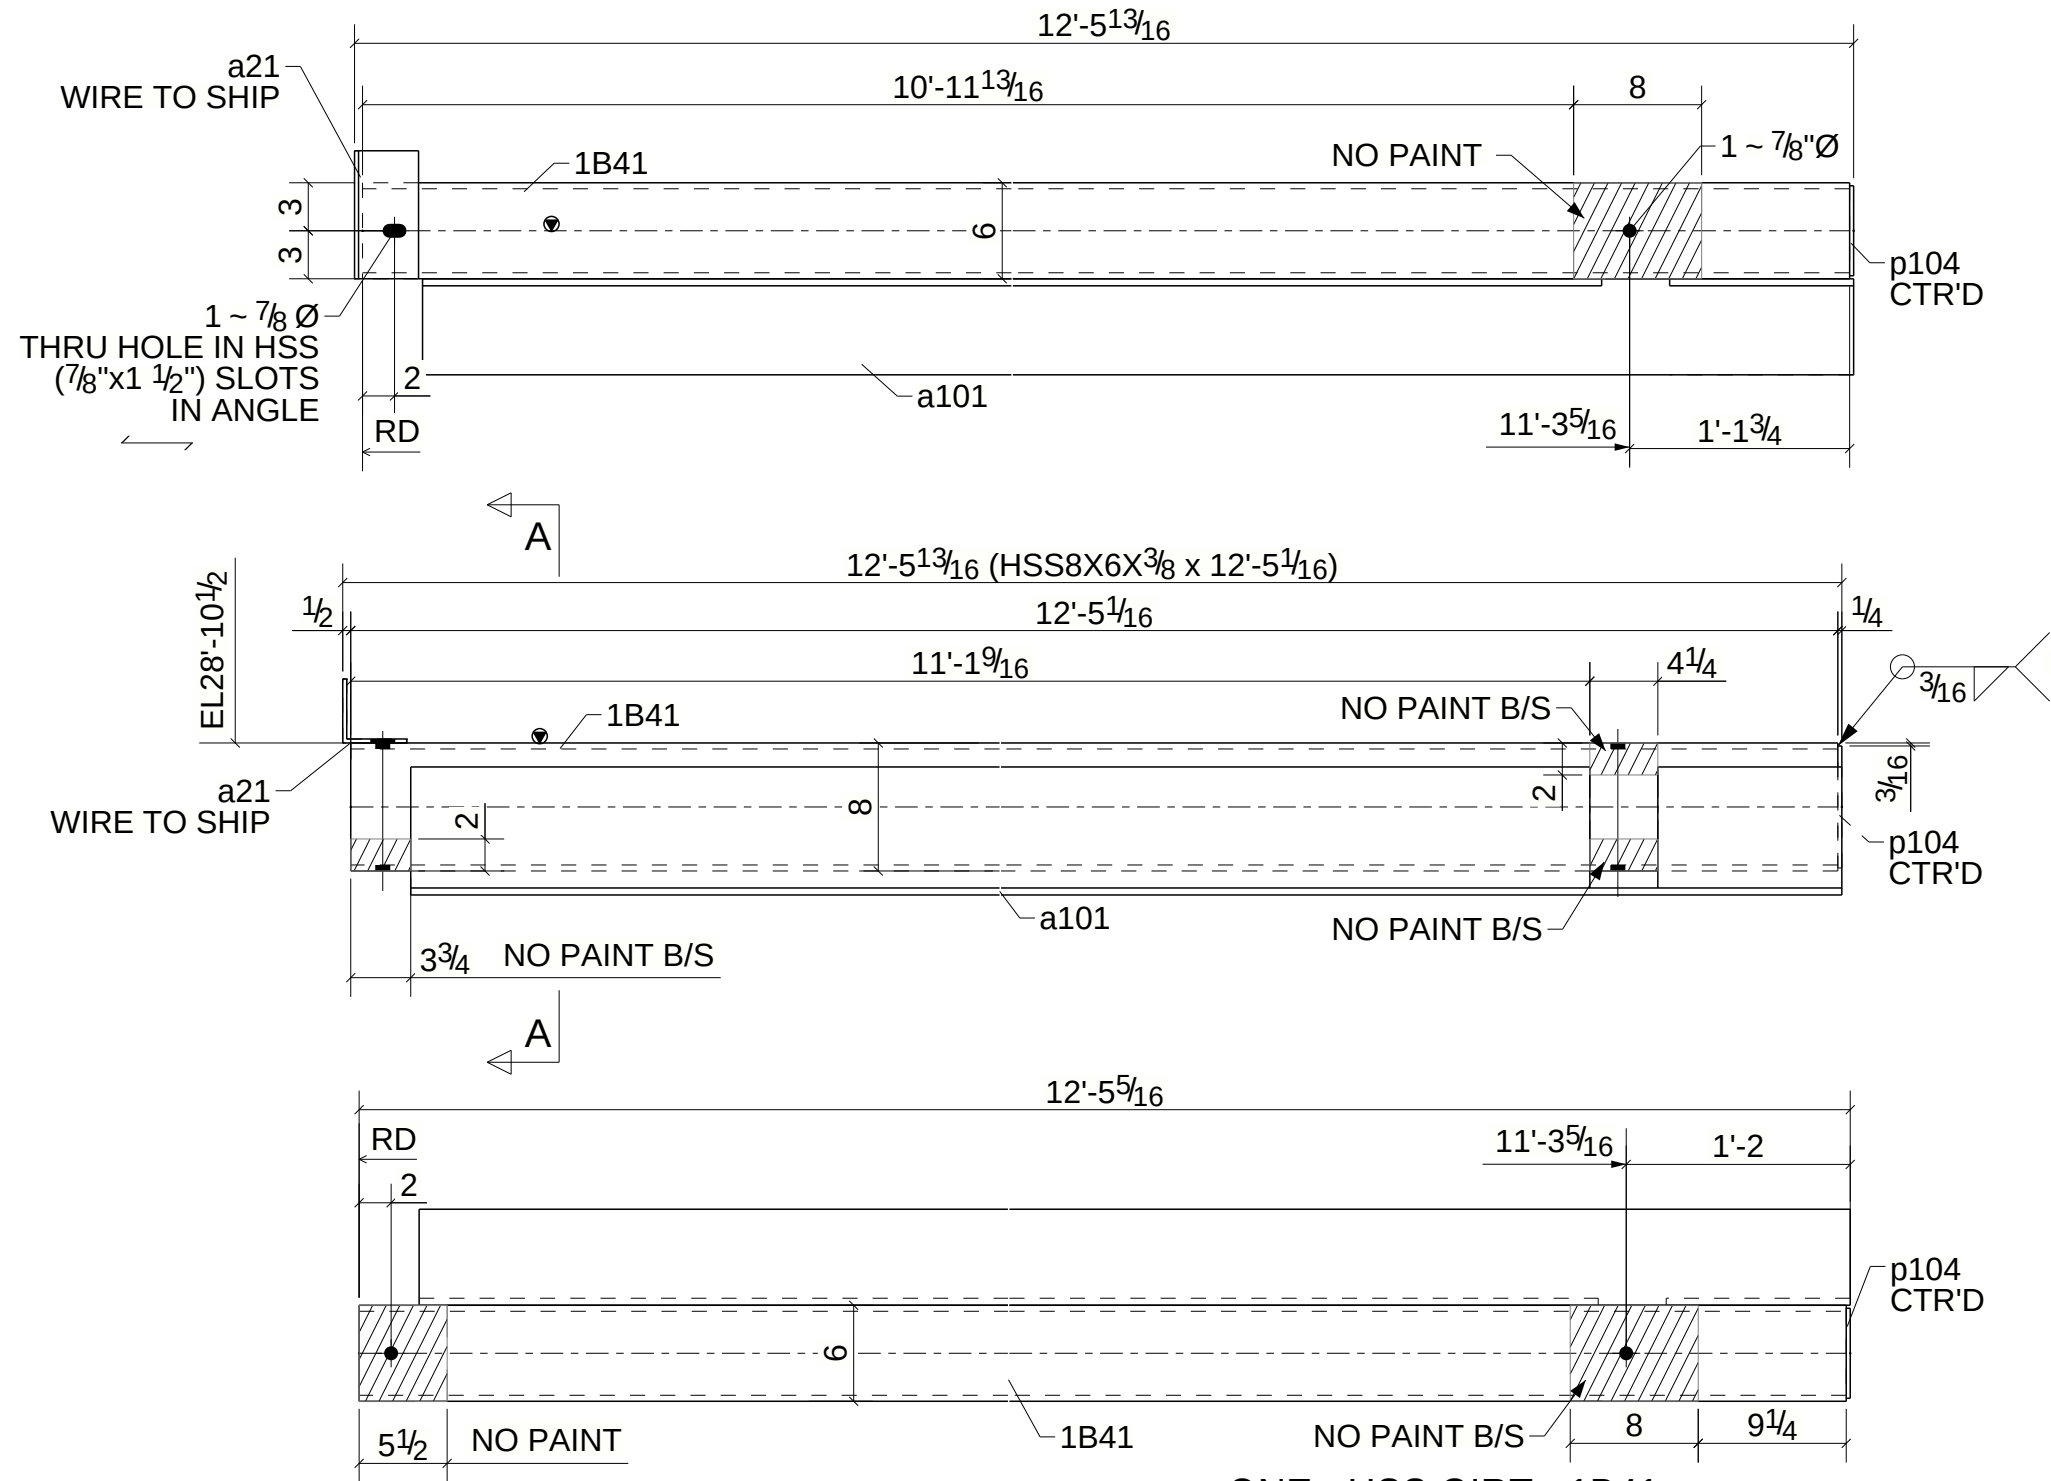

ONE - HSS GIRT - 1B41

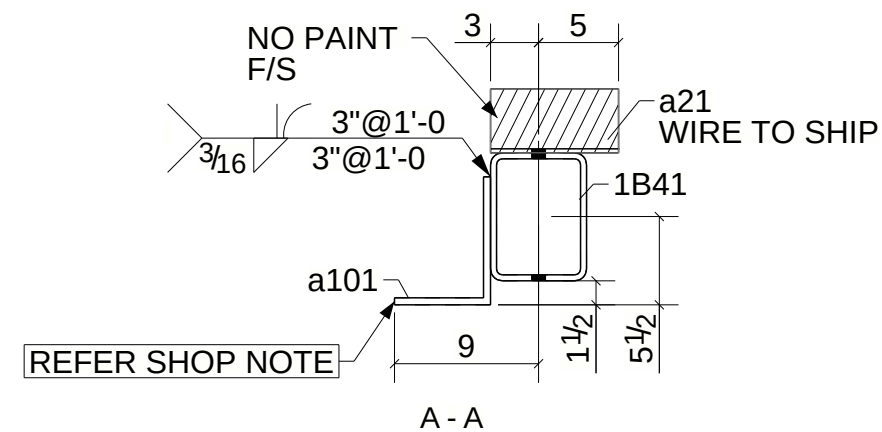

SHOP NOTE:
1. SHELF ANGLE SHOULD BE GALV. SEPERATELY BEFORE WELDING TO HSS.(SURFACE PREP : SSPC-SP3



20 HIGH STREET
PLAINSVILLE, MA 02762
PHONE (508) 381-0429
www.teambes.com

BILL OF MATERIAL							
MARK	TOTAL QTY	SHAPE	LENGTH	TOTAL WEIGHT	REMARKS	ADV MILL #	STEEL GRADE
1B41	1	HSS8X6X3/8	12'-5 1/16"	379	SQ-2		A500-GR.B
a21	1	L4X4X1/4	0'-8"	4			A36
a101	1	L8X6X7/16	12'-1 9/16"	247	GALV.		A36
p104	1	PL1/4"X5 5/8"	0'-7 5/8"	3			A36

0	04/11/2025	For Fabrication	PROJECT NAME GSC JUNIPER RBP PHASE-II				
A	10/15/2024	For Approval					
REV.	DATE	DESCRIPTION					
MATERIAL A36 UNO			LOCATION PARKWAY EVERETT, MA				
HOLES 13/16 Ø UNO			CONTRACTOR BUILDING ENVELOPE SYSTEMS				
WELDS E70XX			DWG TITLE HSS GIRT				
SURFACE PREP. SSPC SP2			DRAWN BY ABJ	CHECKED BY HSR	DATE DRAWN 10/15/2024	PLOT DATE 10/15/2024	DGSTS No. --
PAINT NOTE : SW SHOP PRIMER (U.N.O)			CONTRACT No. 24050			DWG No. 1B41	REV. 0