
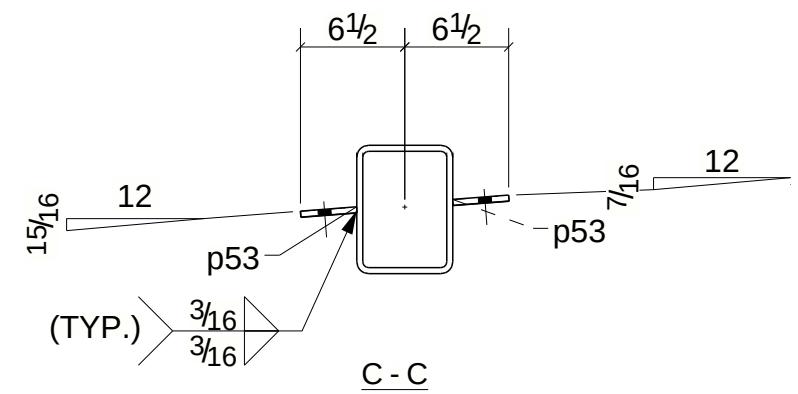
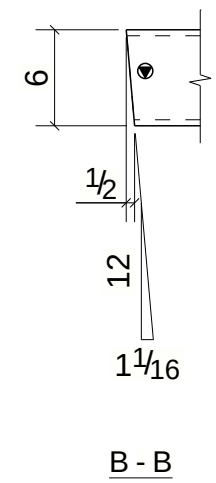
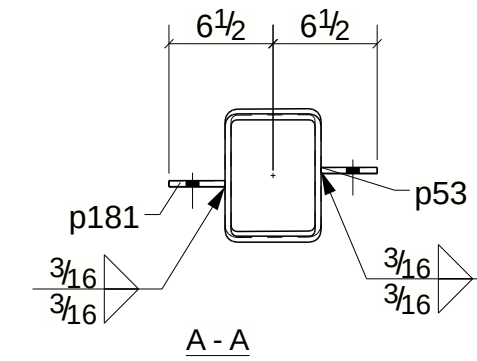


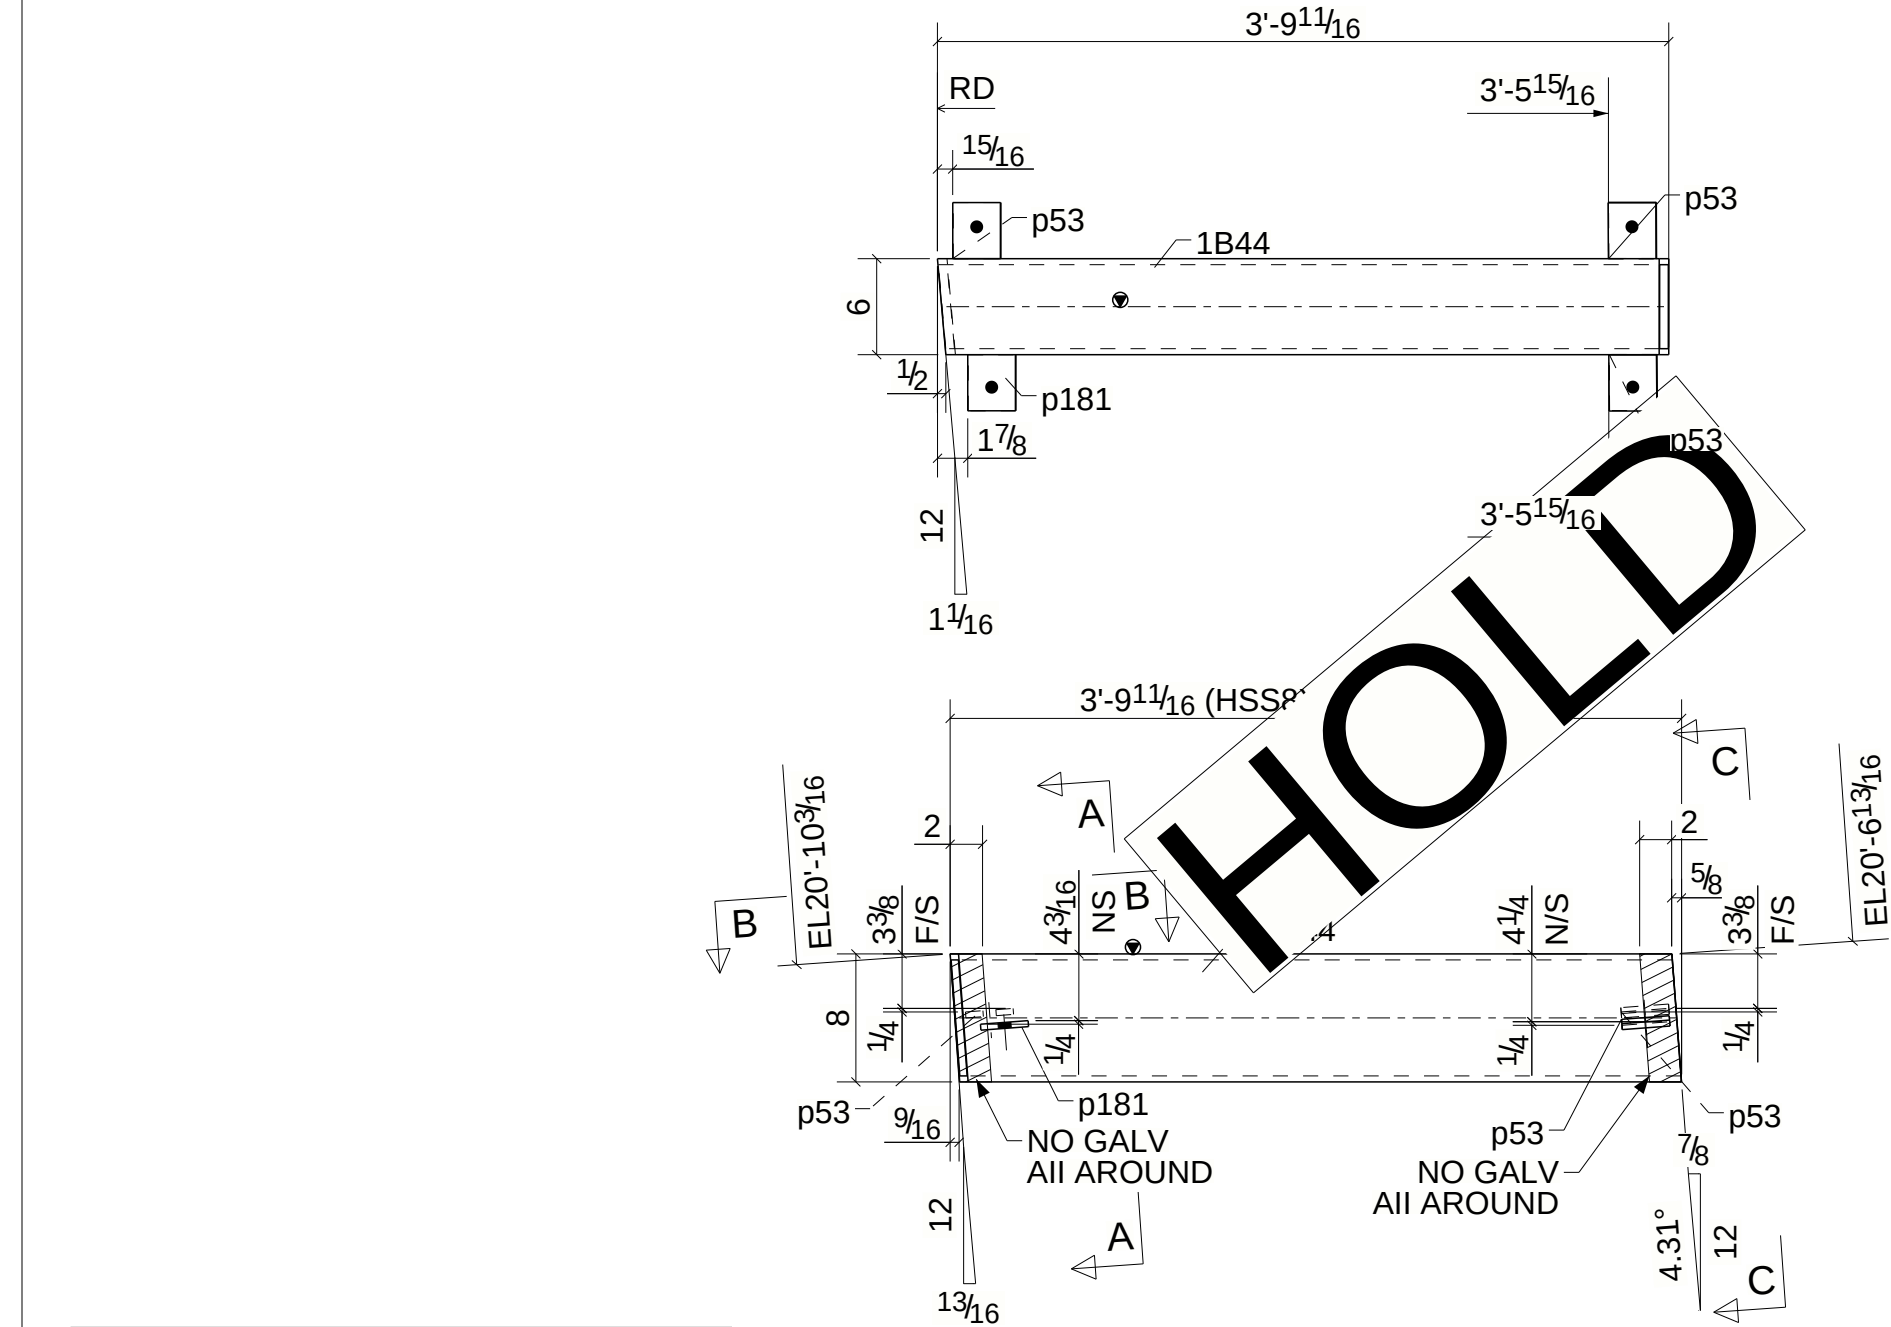

SHOP NOTE:
PROVIDE VENT AND DRAIN AS REQUIRED

FABRICATOR NOTE:
NO GALV. & MASK HATCHED PORTION WITH TWO
PART OF EPOXY BEFORE GALVANIZATION.

ONE - BEAM - 1B44

BILL OF MATERIAL

MARK	TOTAL QTY	SHAPE	LENGTH	TOTAL WEIGHT	REMARKS	ADV MILL #	STEEL GRADE
1B44	1	HSS8X6X3/8	3'-9 11/16"	116	BEV-2 GALV		A500-GR.B
p53	3	PL3/8"X3"	0'-3 1/2"	3			A36
p181	1	PL3/8"X3"	0'-3 1/2"	1			A36

GRID LOCATION	BOTTOM ELEVATION
6-5/W-W.6	19'-10"13/16

Building Envelope Systems

20 HIGH STREET
PLAINSVILLE, MA 02762
PHONE (508) 381-0429
www.teambes.com

PROJECT NAME GSC JUNIPER RBP PHASE-II				
LOCATION PARKWAY EVERETT, MA				
CONTRACTOR BUILDING ENVELOPE SYSTEMS				
DWG TITLE BEAM				
DRAWN BY ABJ	CHECKED BY HSR	DATE DRAWN 03/24/2025	PLOT DATE 03/24/2025	DGSTS No. --
CONTRACT No. 24050		DWG No. 1B44		REV. 0

0	04/11/2025	For Fabrication
A	03/24/2025	For Approval
REV.	DATE	DESCRIPTION
MATERIAL A36 UNO		
HOLES 13/16Ø UNO		
WELDS E70XX		
SURFACE PREP. SSPC SP3		
PAINT NOTE : GALVANIZED		