
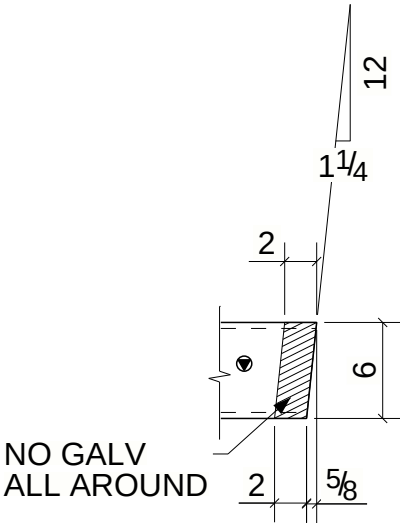


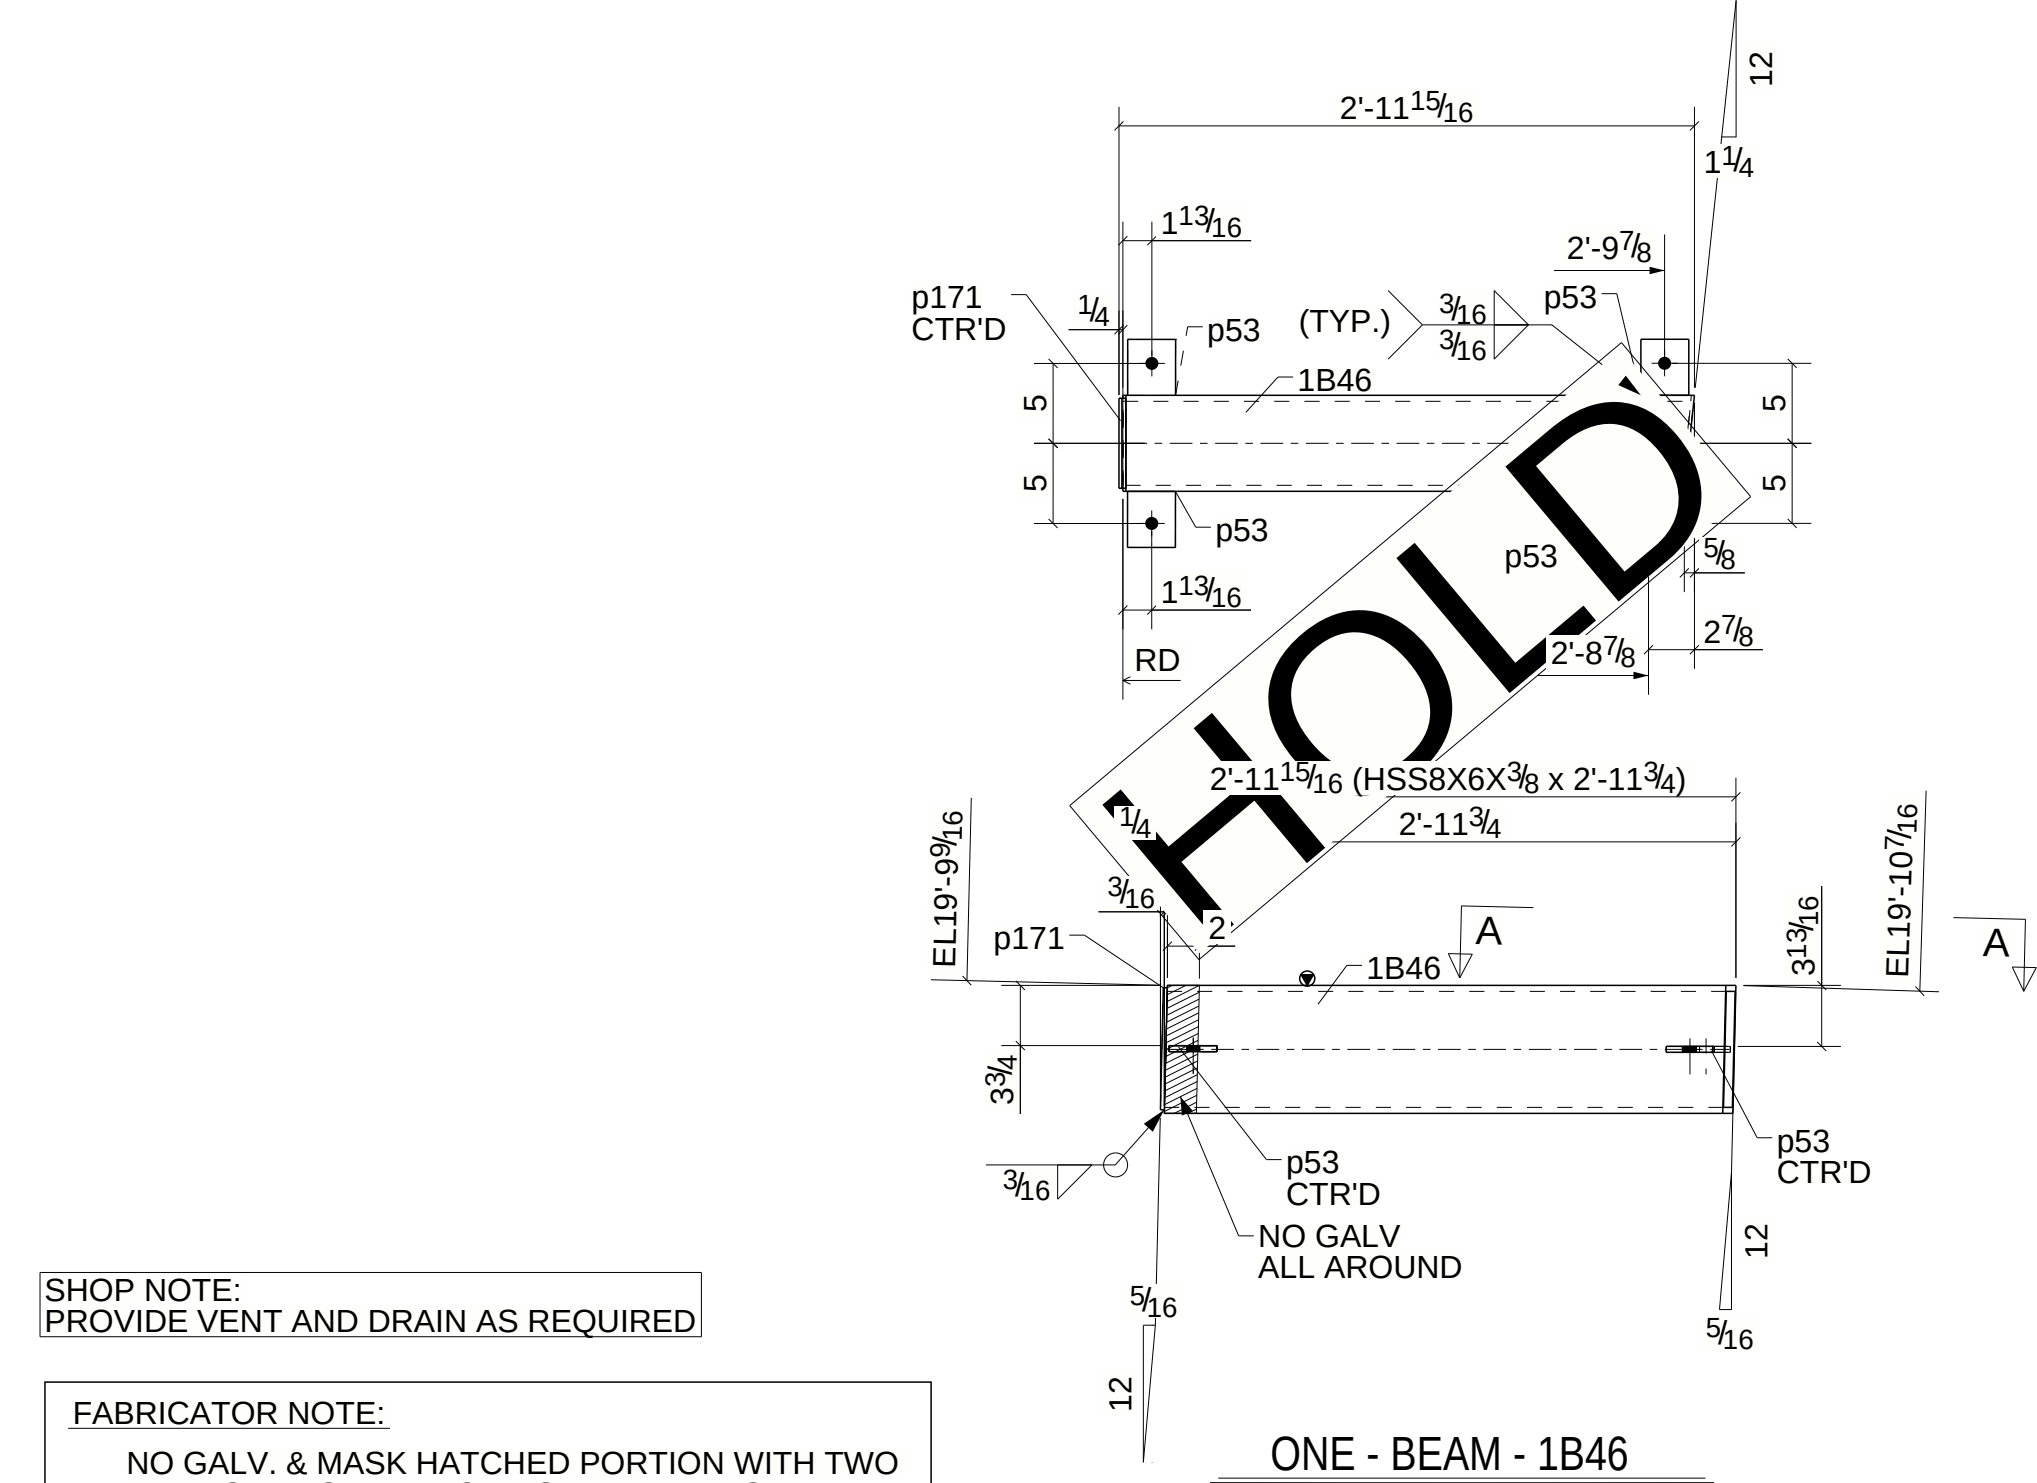

SHOP NOTE:
PROVIDE VENT AND DRAIN AS REQUIRED

FABRICATOR NOTE:
NO GALV. & MASK HATCHED PORTION WITH TWO
PART OF EPOXY BEFORE GALVANIZATION.

BILL OF MATERIAL

MARK	TOTAL QTY	SHAPE	LENGTH	TOTAL WEIGHT	REMARKS	ADV MILL #	STEEL GRADE
1B46	1	HSS8X6X3/8	2'-11 3/4"	91	BEV-2 GALV		A500-GR.B
p53	4	PL3/8"X3"	0'-3 1/2"	4			A36
p171	1	PL1/4"X5 5/8"	0'-7 5/8"	3			A36

0	04/11/2025	For Fabrication
A	03/24/2025	For Approval
REV.	DATE	DESCRIPTION
MATERIAL A36 UNO		
HOLES 13/16Ø UNO		
WELDS E70XX		
SURFACE PREP. SSPC SP3		
PAINT NOTE : GALVANIZED		

</