
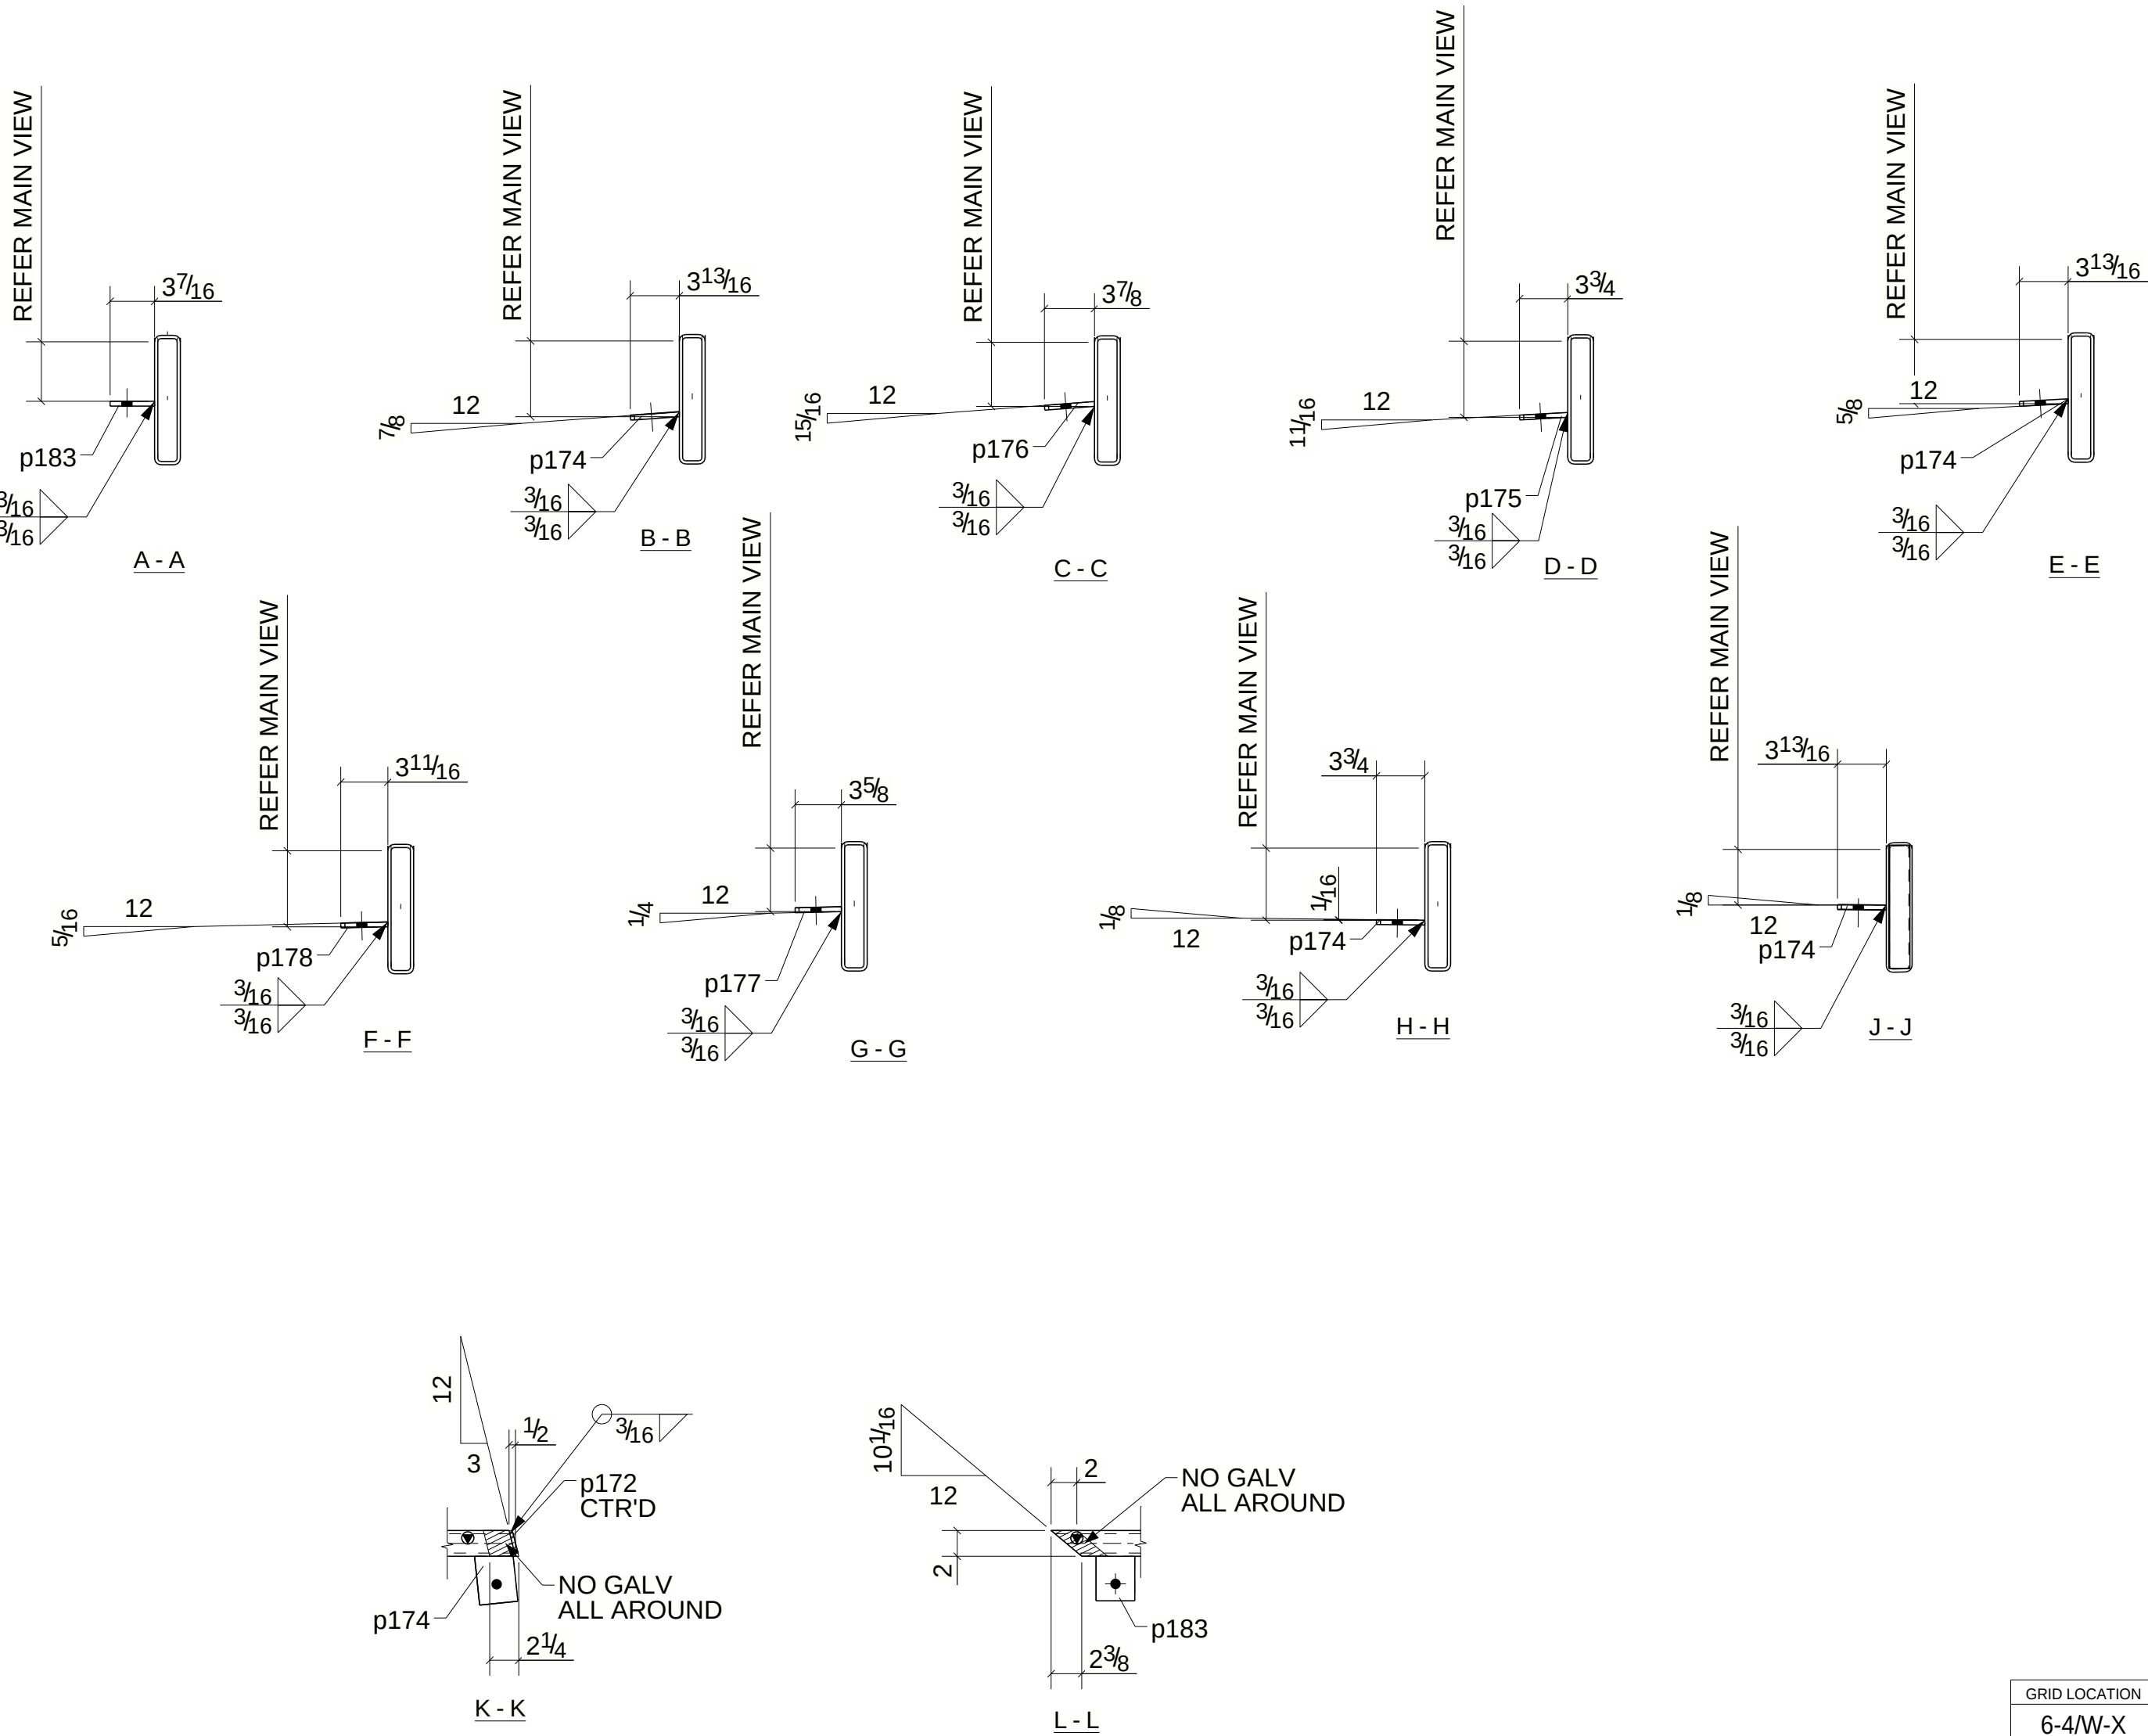


BILL OF MATERIAL							
MARK	TOTAL QTY	SHAPE	LENGTH	TOTAL WEIGHT	REMARKS	ADV MILL #	STEEL GRADE
1B48	1	HSS10X2X1/4	21'-7 3/4"	386	BEV-2 GALV		A500-GR B
p172	1	PL1/4"x1 5/8"	0'-9 9/16"	1			A36
p174	4	PL3/8"x3"	0'-3 13/16"	5			A36
p175	1	PL3/8"x3"	0'-3 3/4"	1			A36
p176	1	PL3/8"x3"	0'-3 7/8"	1			A36
p177	1	PL3/8"x3"	0'-3 5/8"	1			A36
p178	1	PL3/8"x3"	0'-3 11/16"	1			A36
p183	1	PL3/8"x3"	0'-3 7/16"	1			A36

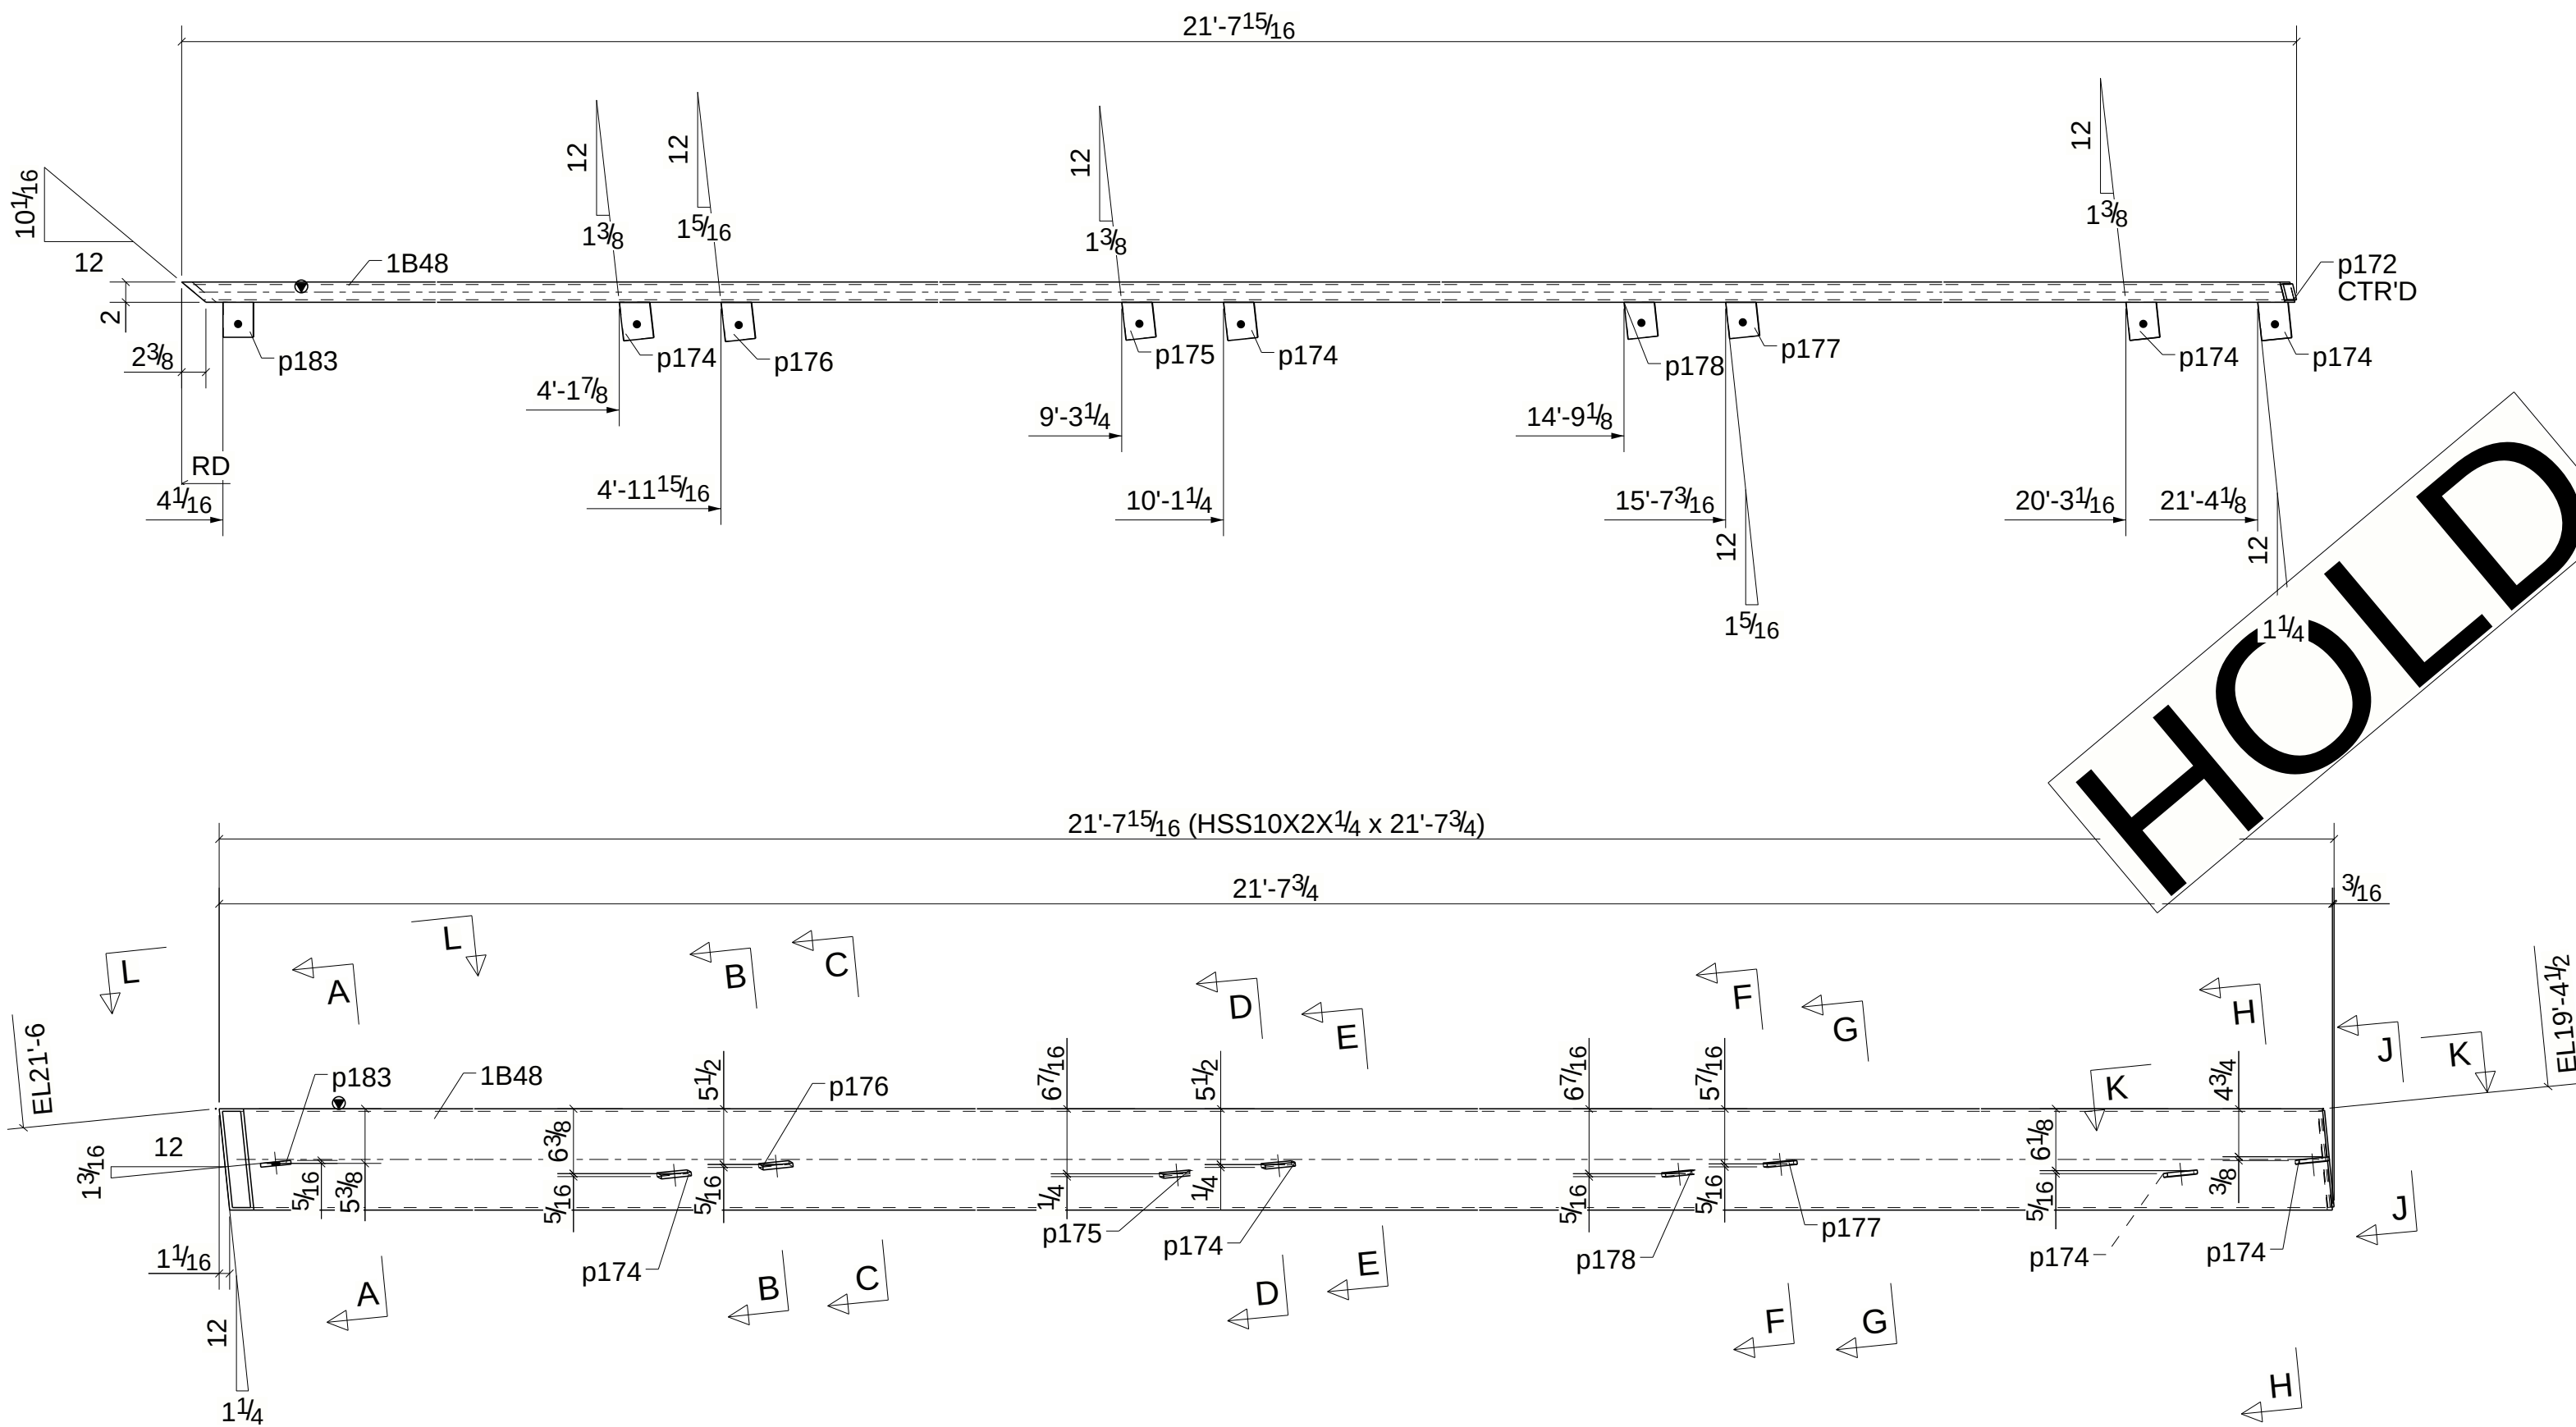

SHOP NOTE:
PROVIDE DRAIN AND VENT AS REQUIRED.

FABRICATOR NOTE:
NO GALV. & MASK HATCHED PORTION WITH TWO
PART OF EPOXY BEFORE GALVANIZATION.

ONE - BEAM - 1B48

0	04/11/2025	For Fabrication
A	03/24/2025	For Approval
REV.	DATE	DESCRIPTION
MATERIAL A36 UNO		
HOLES 13/16Ø UNO		
WELDS E70XX		
SURFACE PREP. SSPC SP3		
PAINT NOTE : GALVANIZED		
PROJECT NAME GSC JUNIPER RBP PHASE-II		
LOCATION PARKWAY EVERETT, MA		
CONTRACTOR BUILDING ENVELOPE SYSTEMS		
DWG TITLE BEAM		
DRAWN BY ABJ	CHECKED BY HSR	DATE DRAWN 03/24/2025
PLOT DATE 03/24/2025	DGSTS No. ---	REV. 0
CONTRACT No. 24050		DWG No. 1B48

Building Envelope Systems

20 HIGH STREET
PLAINSVILLE, MA 02762
PHONE (508) 381-0429
www.teambes.com

GRID LOCATION	BOTTOM ELEVATION
6-4/W-X	18'-6"7/16