
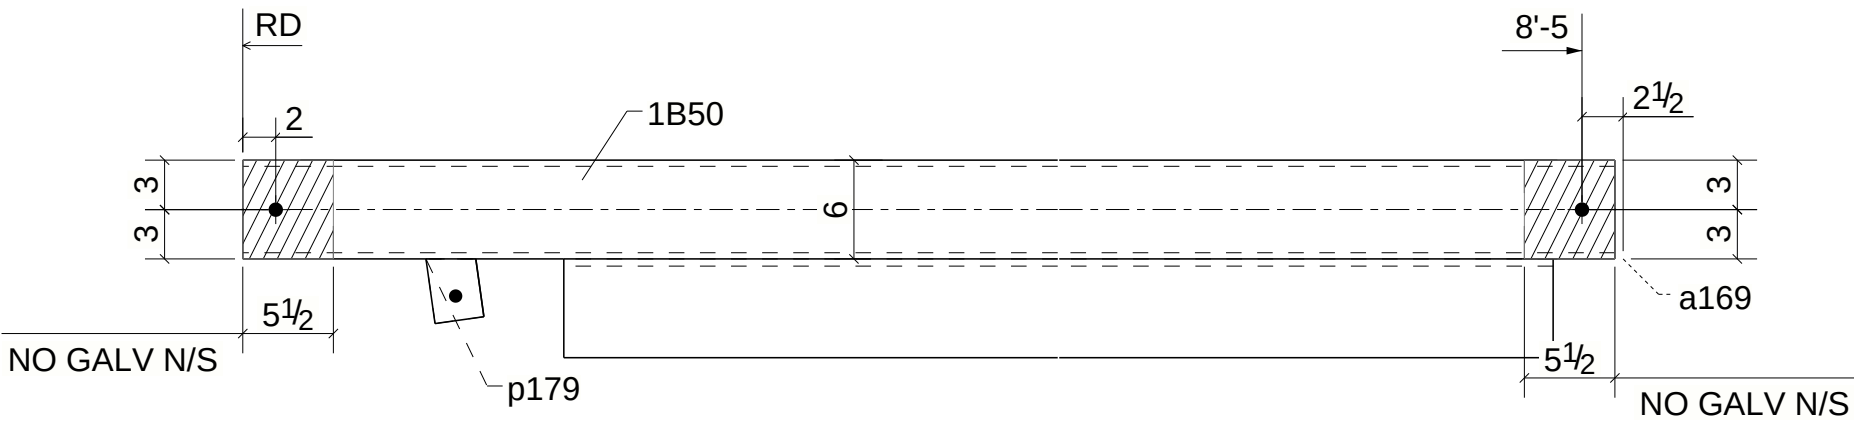
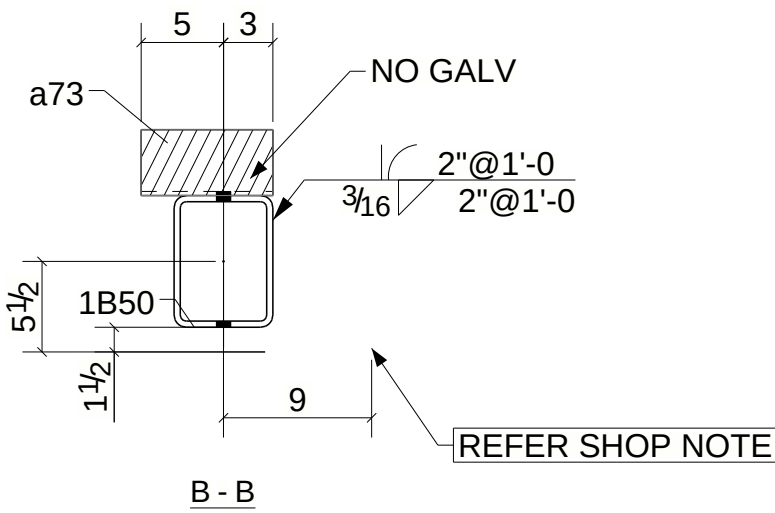
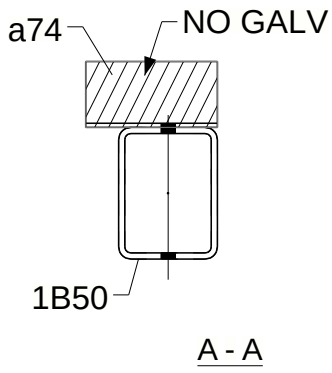
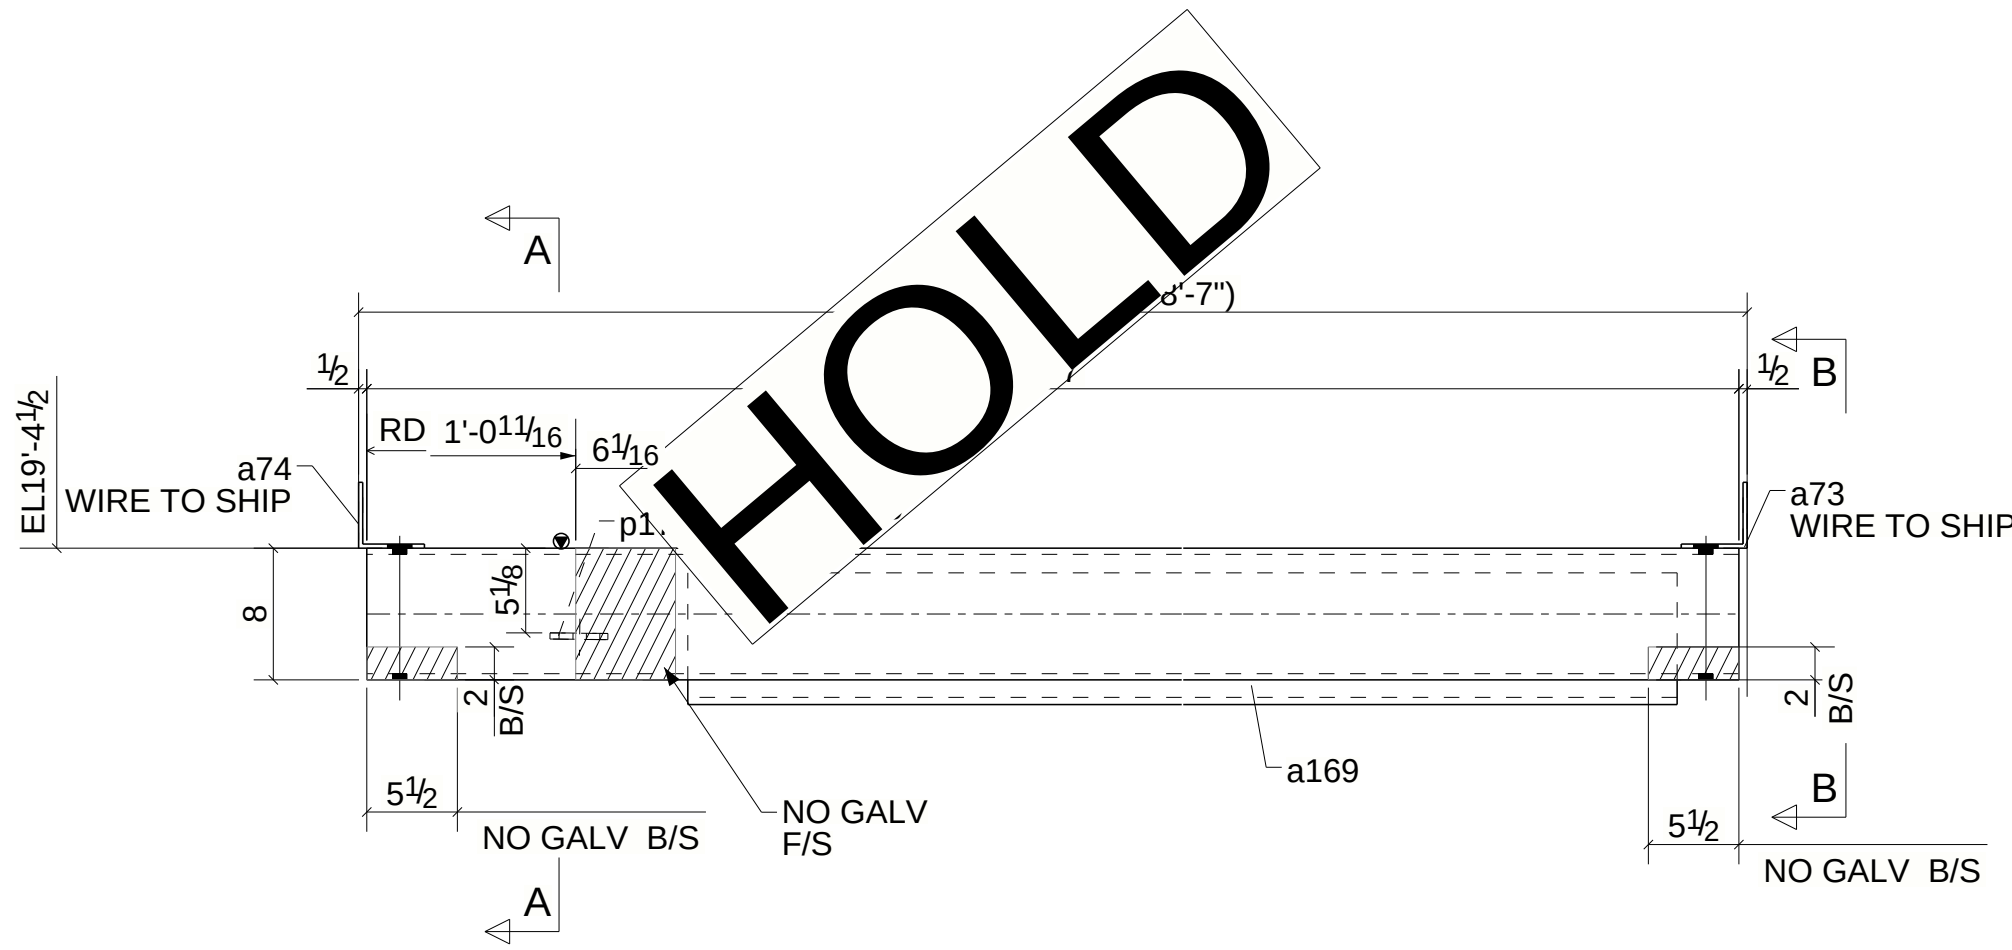


BILL OF MATERIAL

MARK	TOTAL QTY	SHAPE	LENGTH	TOTAL WEIGHT	REMARKS	ADV MILL #	STEEL GRADE
1B50	1	HSS8X6X3/8	8'-7"	262	SQ-2		A500-GR B
a73	1	L4X4X1/4	0'-8"	4			A36
a74	1	L4X4X1/4	0'-8"	4			A36
a169	1	L8X6X7/16	6'-7 3/4"	135	GALV.		A36
p179	1	PL3/8"X3"	0'-3 15/16"	1			A36

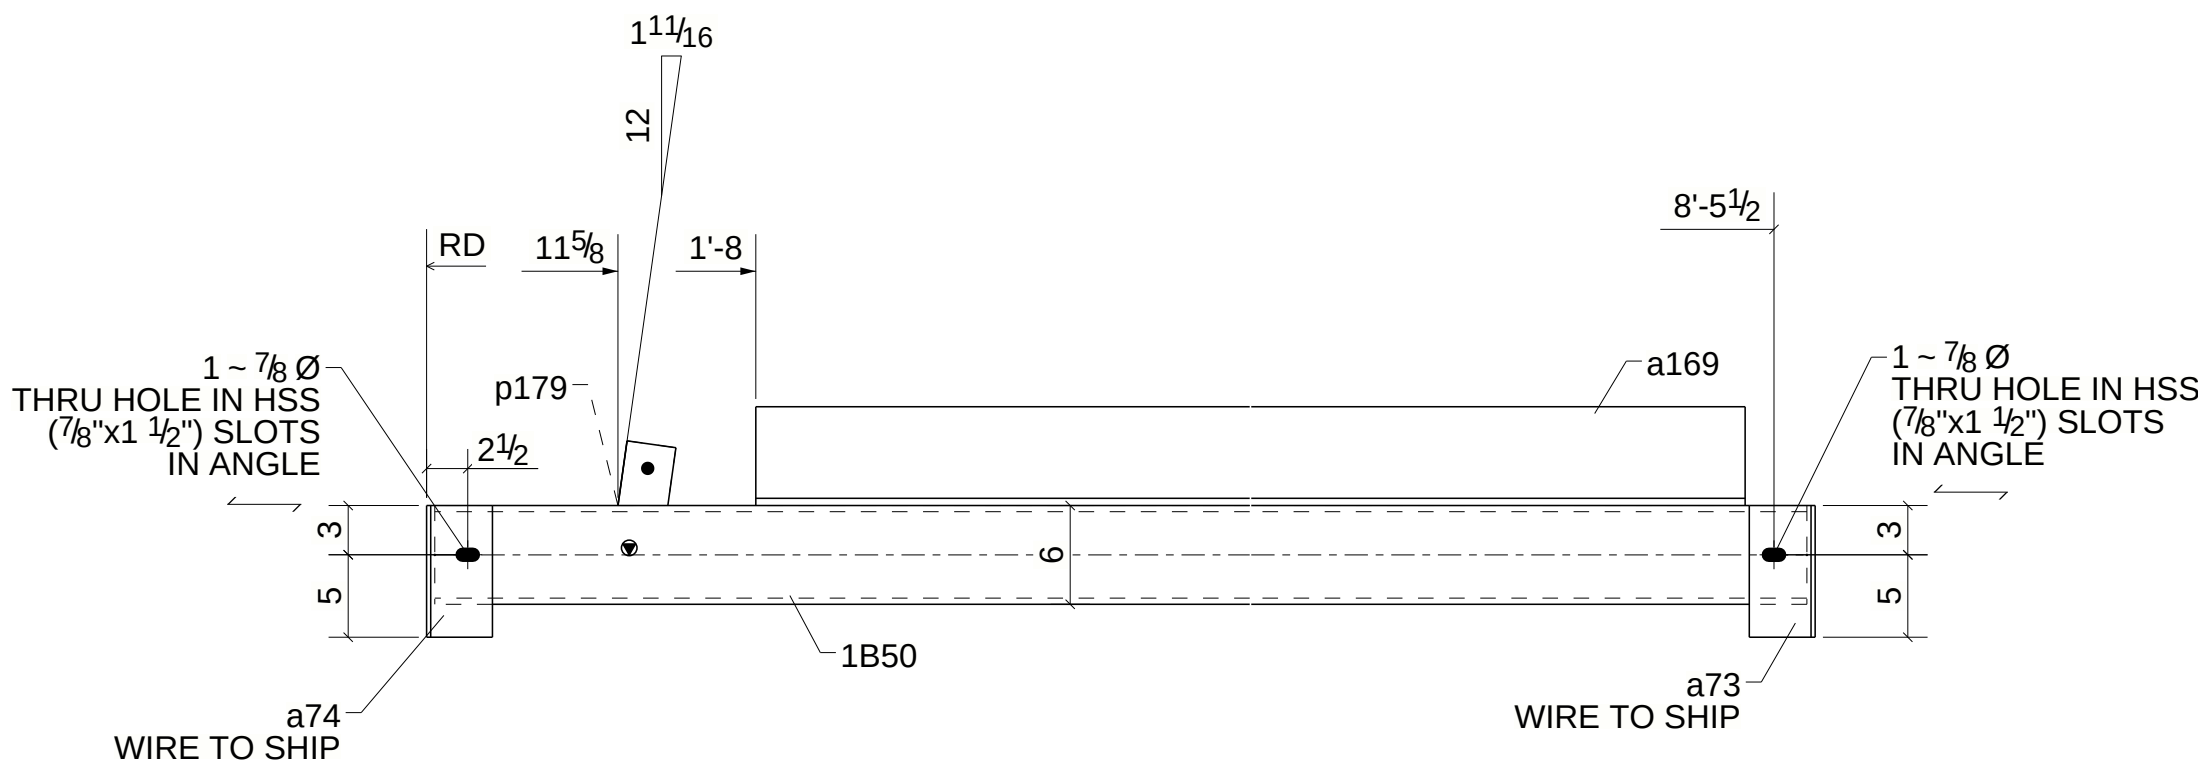

FABRICATOR NOTE:
NO GALV. & MASK HATCHED PORTION WITH TWO PART OF EPOXY BEFORE GALVANIZATION.

SHOP NOTE:
1. SHELF ANGLE SHOULD BE GALV. SEPERATELY BEFORE WELDING TO HSS.(SURFACE PREP : SSPC-SP3)

Building Envelope Systems

20 HIGH STREET
PLAINSVILLE, MA 02762
PHONE (508) 381-0429
www.teambes.com

0	04/11/2025	For Fabrication	PROJECT NAME		GSC JUNIPER RBP PHASE-II				
A	03/24/2025	For Re_Approval	LOCATION		PARKWAY EVERETT, MA				
REV.	DATE	DESCRIPTION	CONTRACTOR		BUILDING ENVELOPE SYSTEMS				
MATERIAL A36 UNO			DWG TITLE		HSS GIRT				
HOLES 13/16Ø UNO			DRAWN BY ABJ		CHECKED BY HSR		DATE DRAWN 03/24/2025	PLOT DATE 03/24/2025	DGSTS No. --
WELDS E70XX			CONTRACT No.		24050		DWG No.		1B50
SURFACE PREP. SSPC-SP3			PAINT NOTE :		GALVANIZED		REV.		0

ONE - HSS GIRT - 1B50