



Tekla Structures

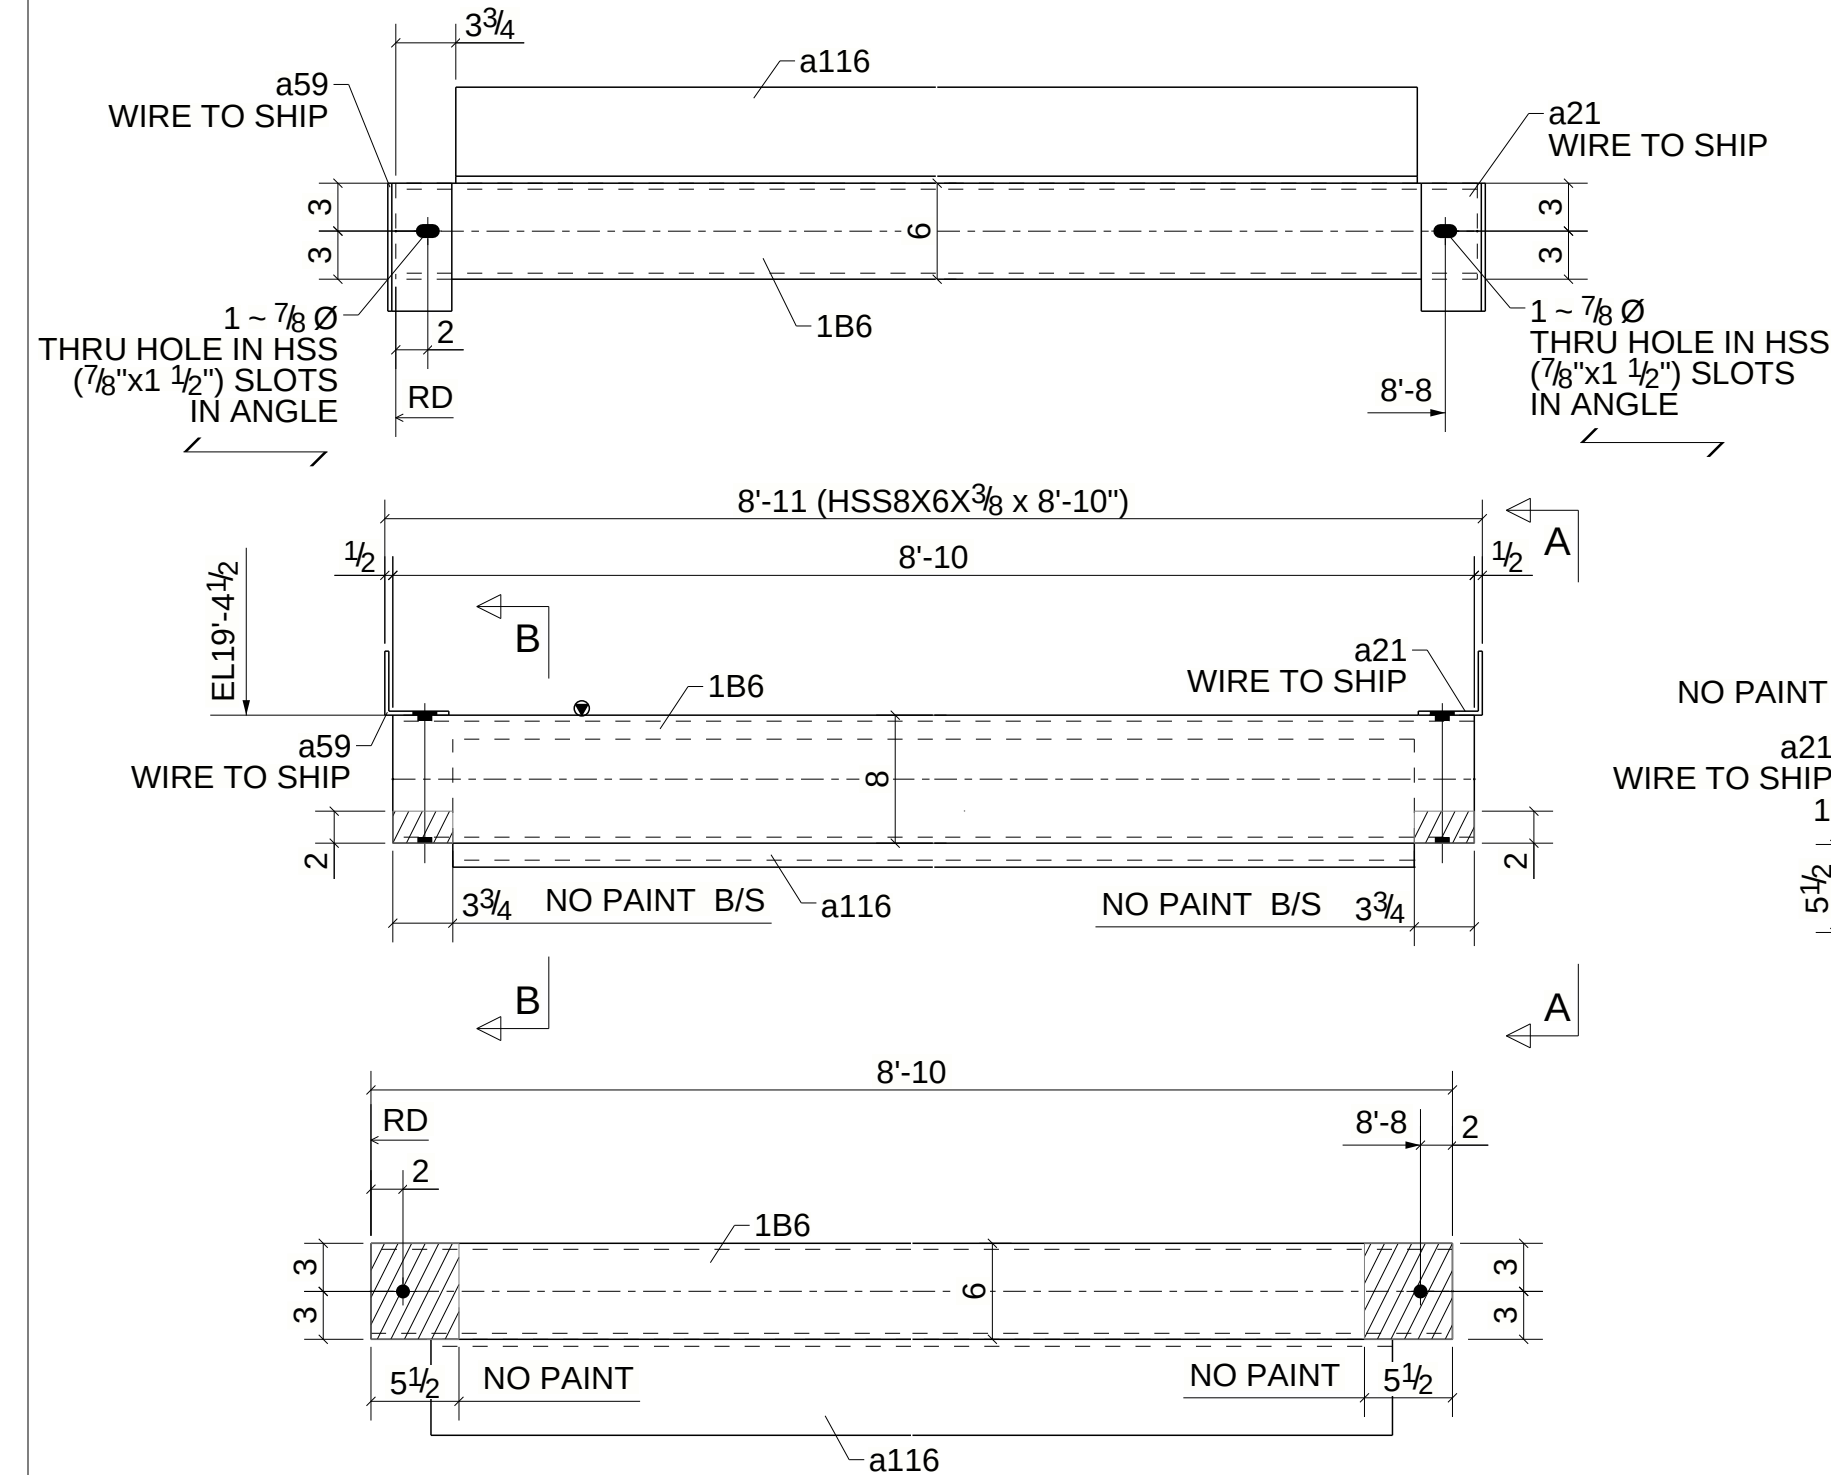

2 - HSS GIRTS - 1B6

BILL OF MATERIAL							
MARK	TOTAL QTY	SHAPE	LENGTH	TOTAL WEIGHT	REMARKS	ADV MILL #	STEEL GRADE
1B6	2	HSS8X6X3/8	8'-10"	539	SQ-2		A500-GR.B
a21	2	L4X4X1/4	0'-8"	9			A36
a59	2	L4X4X1/4	0'-8"	9			A36
a116	2	L8X6X7/16	8'-2 1/2"	335	GALV.		A36

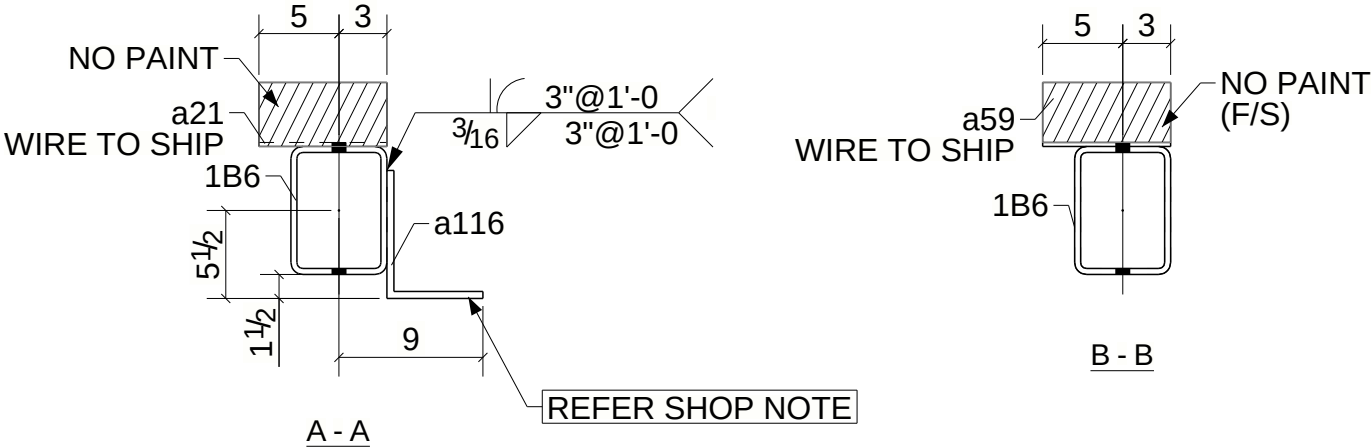

SHOP NOTE:
1. SHELF ANGLE SHOULD BE GALV. SEPERATELY BEFORE WELDING TO HSS.(SURFACE PREP : SSPC-SP3



20 HIGH STREET
PLAINVILLE, MA 02762
PHONE (508) 381-0429
www.teambes.com

0	04/11/2025	For Fabrication	PROJECT NAME GSC JUNIPER RBP PHASE-II			
A	10/16/2024	For Approval				
REV.	DATE	DESCRIPTION	LOCATION PARKWAY EVERETT, MA			
MATERIAL A36 UNO			CONTRACTOR BUILDING ENVELOPE SYSTEMS			
HOLES 13/16Ø UNO			DWG TITLE HSS GIRT			
WELDS E70XX			DRAWN BY ABJ	CHECKED BY HSR	DATE DRAWN 10/15/2024	PLOT DATE 10/15/2024
SURFACE PREP. SSPC SP2			CONTRACT No. 24050		DWG No. 1B6	
PAINT NOTE : SW SHOP PRIMER (U.N.O)					DGSTS No. --	REV. 0