

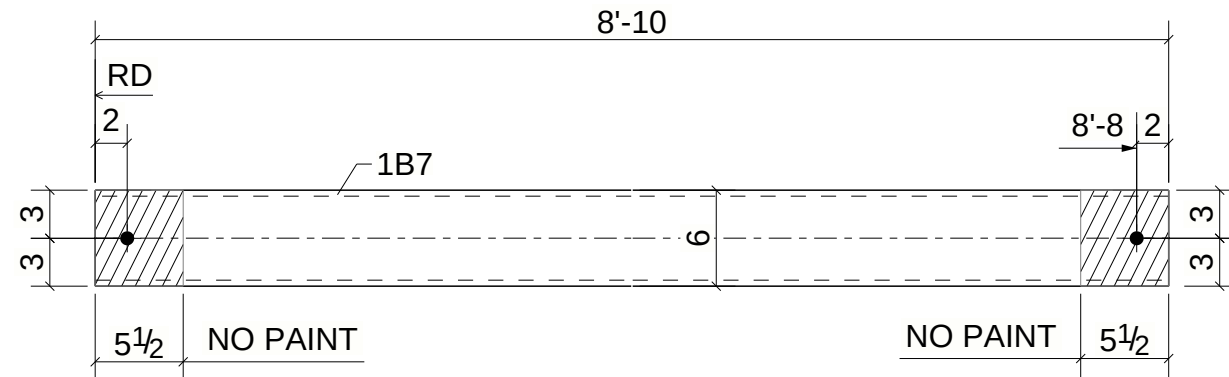
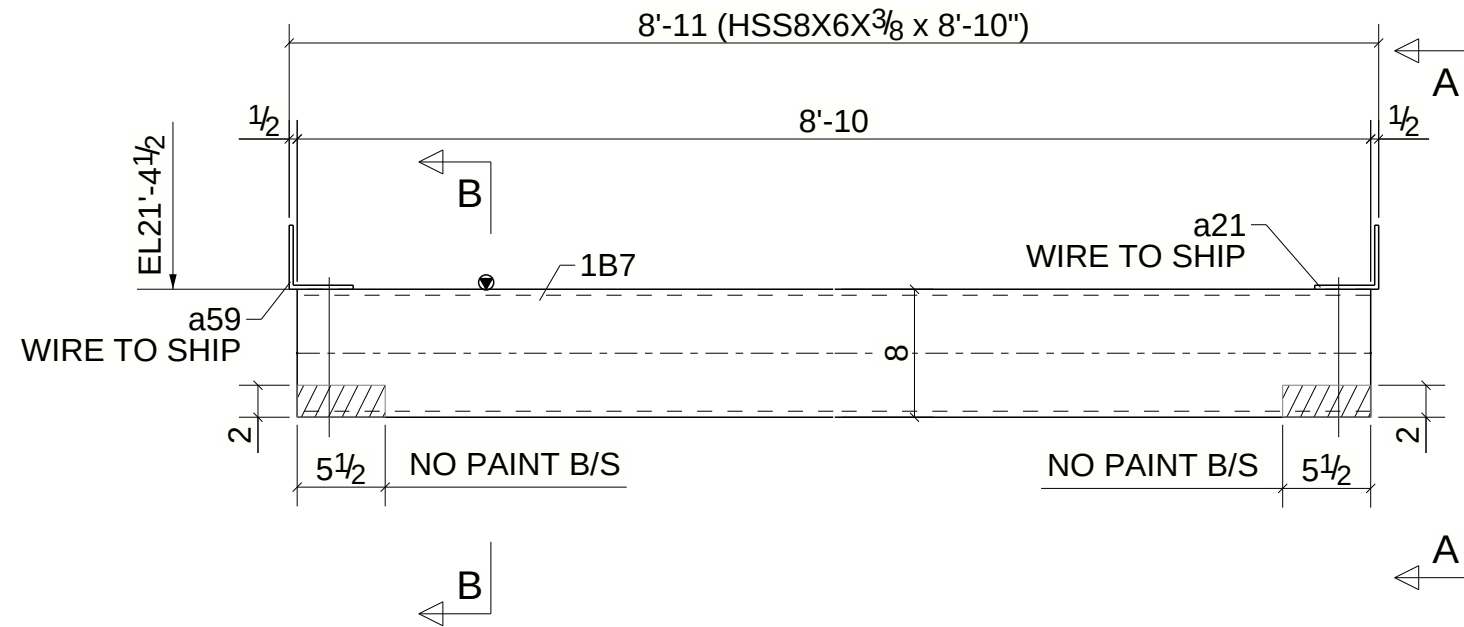
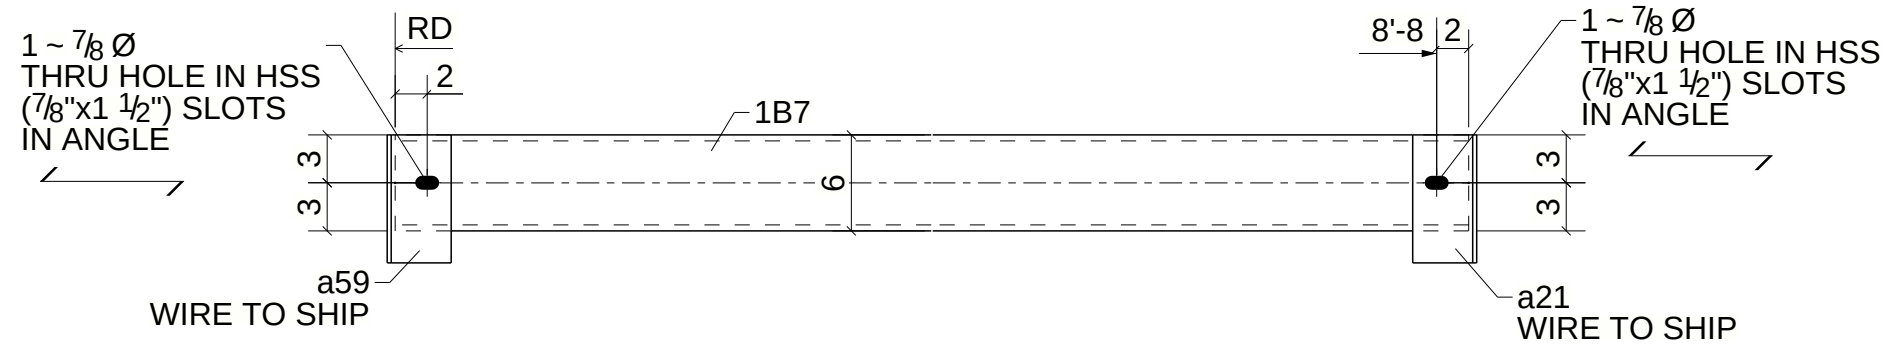


Tekla Structures

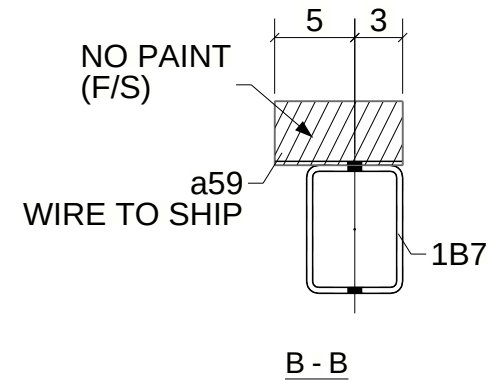

ONE - HSS GIRT - 1B7

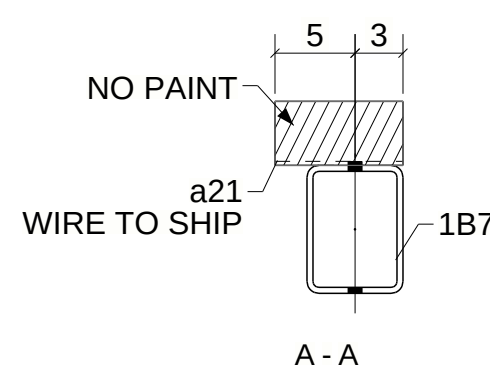

BILL OF MATERIAL

MARK	TOTAL QTY	SHAPE	LENGTH	TOTAL WEIGHT	REMARKS	ADV MILL #	STEEL GRADE
1B7	1	HSS8X6X3/8	8'-10"	270	SQ-2		A500-GR.B
a21	1	L4X4X1/4	0'-8"	4			A36
a59	1	L4X4X1/4	0'-8"	4			A36

0	04/11/2025	For Fabrication
A	10/16/2024	For Approval
REV.	DATE	DESCRIPTION
MATERIAL A36 UNO		
HOLES 13/16 inch UNO		
WELDS E70XX		
SURFACE PREP. SSPC SP2		
PAINT NOTE : SW SHOP PRIMER		

Building Envelope Systems  20 HIGH STREET PLAINSVILLE, MA 02762 PHONE (508) 381-0429 www.teambes.com	
PROJECT NAME GSC JUNIPER RBP PHASE-II	
LOCATION PARKWAY EVERETT, MA	
CONTRACTOR BUILDING ENVELOPE SYSTEMS	
DWG TITLE HSS GIRT	
DRAWN BY ABJ	CHECKED BY HSR DATE DRAWN 10/15/2024
	PLOT DATE 10/15/2024 DGSTS No. --
CONTRACT No. 24050	DWG No. 1B7 REV. 0