


Tekla Structures

BILL OF MATERIAL							
MARK	TOTAL QTY	SHAPE	LENGTH	TOTAL WEIGHT	REMARKS	ADV MILL #	STEEL GRADE
1C1	2	HSS6X6X3/8	8'-7 1/2"	445	SQ-2		A500-GR.B
a72	4	L7X4X3/8	0'-4"	18			A36
	2	3/4"Ø A325N BOLT	0'-8"	3	Workshop		

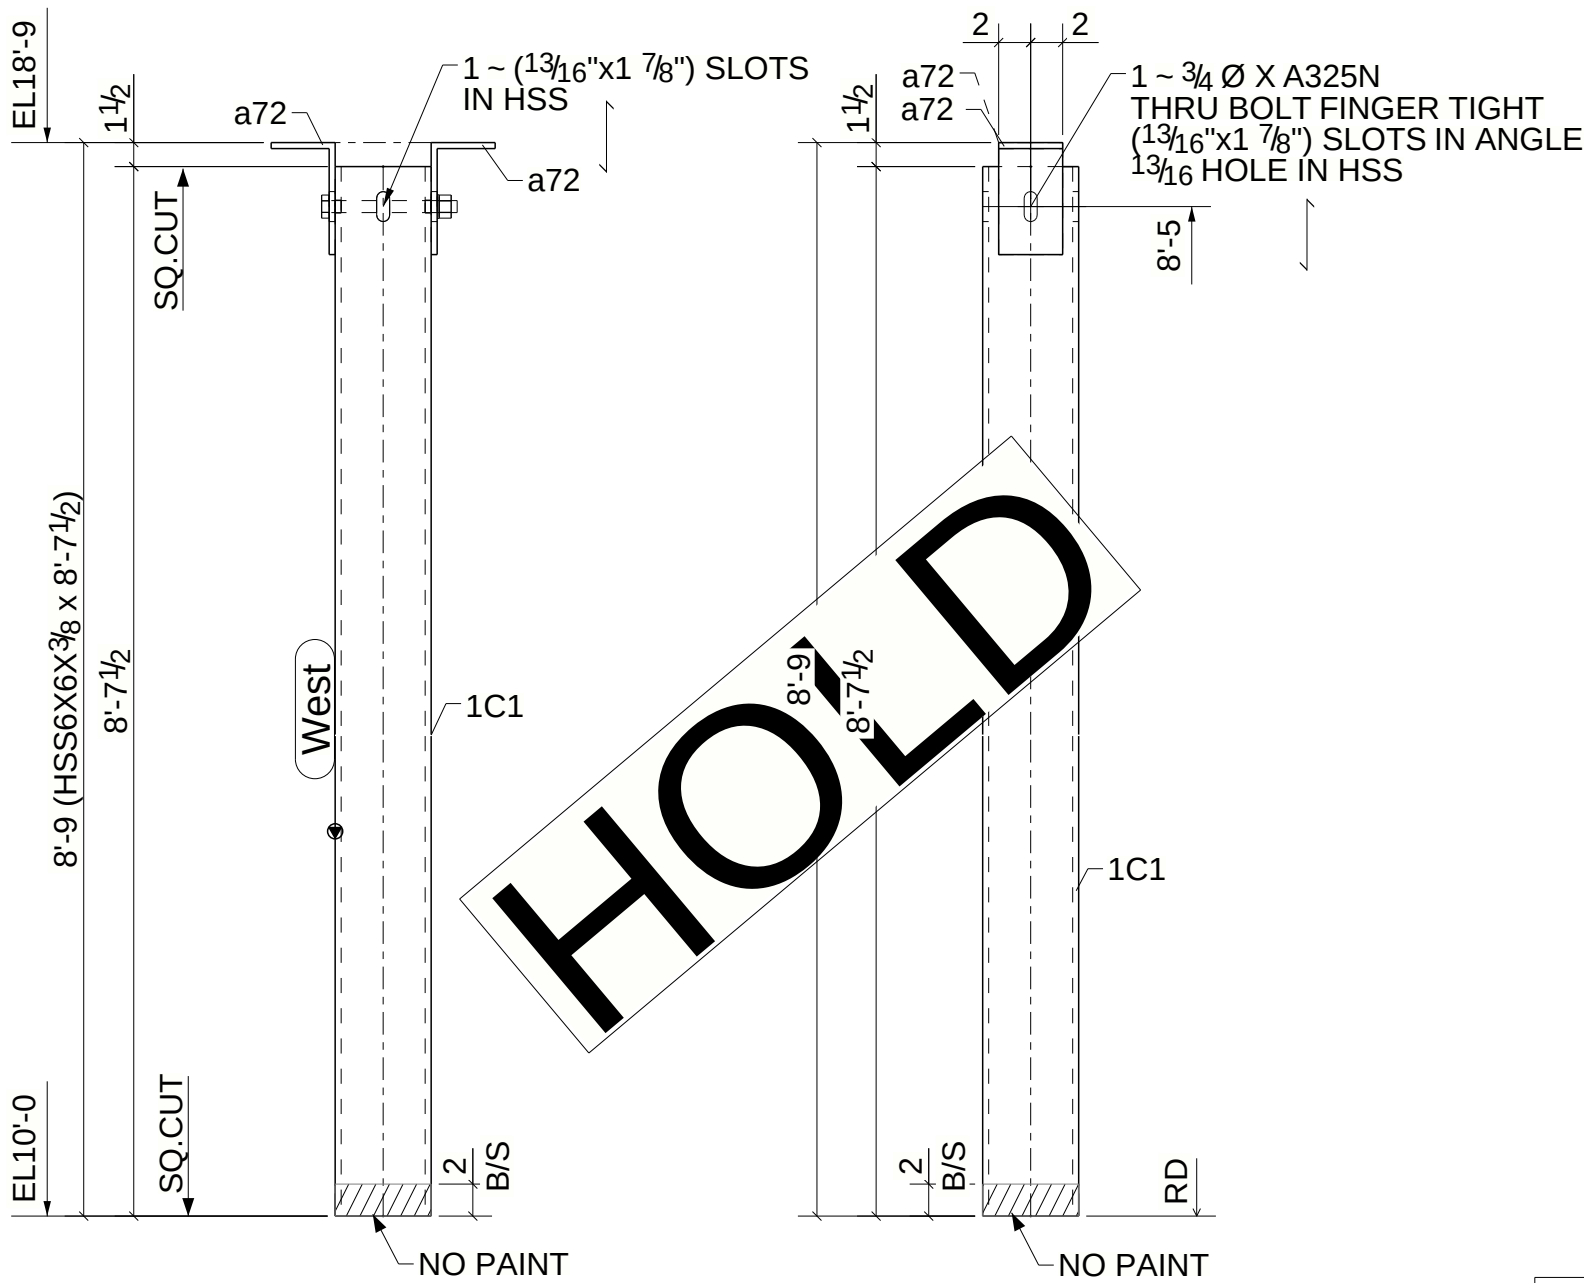

2 - COLUMNS - 1C1

GRID LOCATION	BOTTOM ELEVATION
8-7/T	10'-0"
8-7/T	10'-0"



20 HIGH STREET
PLAINSVILLE, MA 02762
PHONE (508) 381-0429
www.teambes.com

0	04/11/2025	For Fabrication
0	04/11/2025	For Fabrication
A	10/16/2024	For Approval
REV.	DATE	DESCRIPTION
MATERIAL A36 UNO		
HOLES 13/16Ø UNO		
WELDS E70XX		
SURFACE PREP. SSPC SP2		
PAINT NOTE : SW SHOP PRIMER		

PROJECT NAME GSC JUNIPER RBP PHASE-II					
LOCATION PARKWAY EVERETT, MA					
CONTRACTOR BUILDING ENVELOPE SYSTEMS					
DWG TITLE COLUMN					
DRAWN BY ABJ	CHECKED BY HSR	DATE DRAWN 10/15/2024	PLOT DATE 10/15/2024	DGSTS No. --	REV. 0
CONTRACT No. 24050		DWG No. 1C1			