
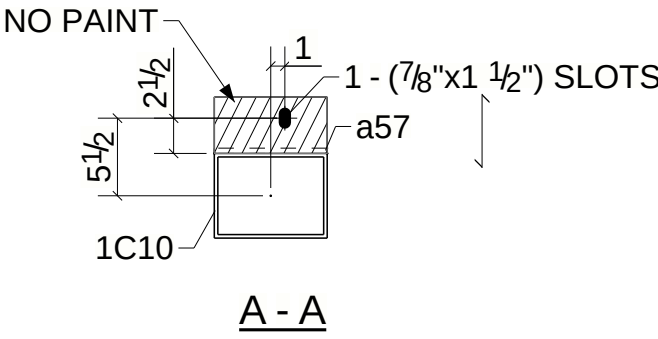


BILL OF MATERIAL							
MARK	TOTAL QTY	SHAPE	LENGTH	TOTAL WEIGHT	REMARKS	ADV MILL #	STEEL GRADE
1C10	2	HSS8X6X1/4	20'-1 3/4"	846	SQ-2		A500-GR B
a56	4	L7X4X3/8	0'-4"	18			A36
a57	6	L4X4X3/8	0'-8"	39			A36
	2	3/4"Ø A325N BOLT	0'-8"	3	Workshop		

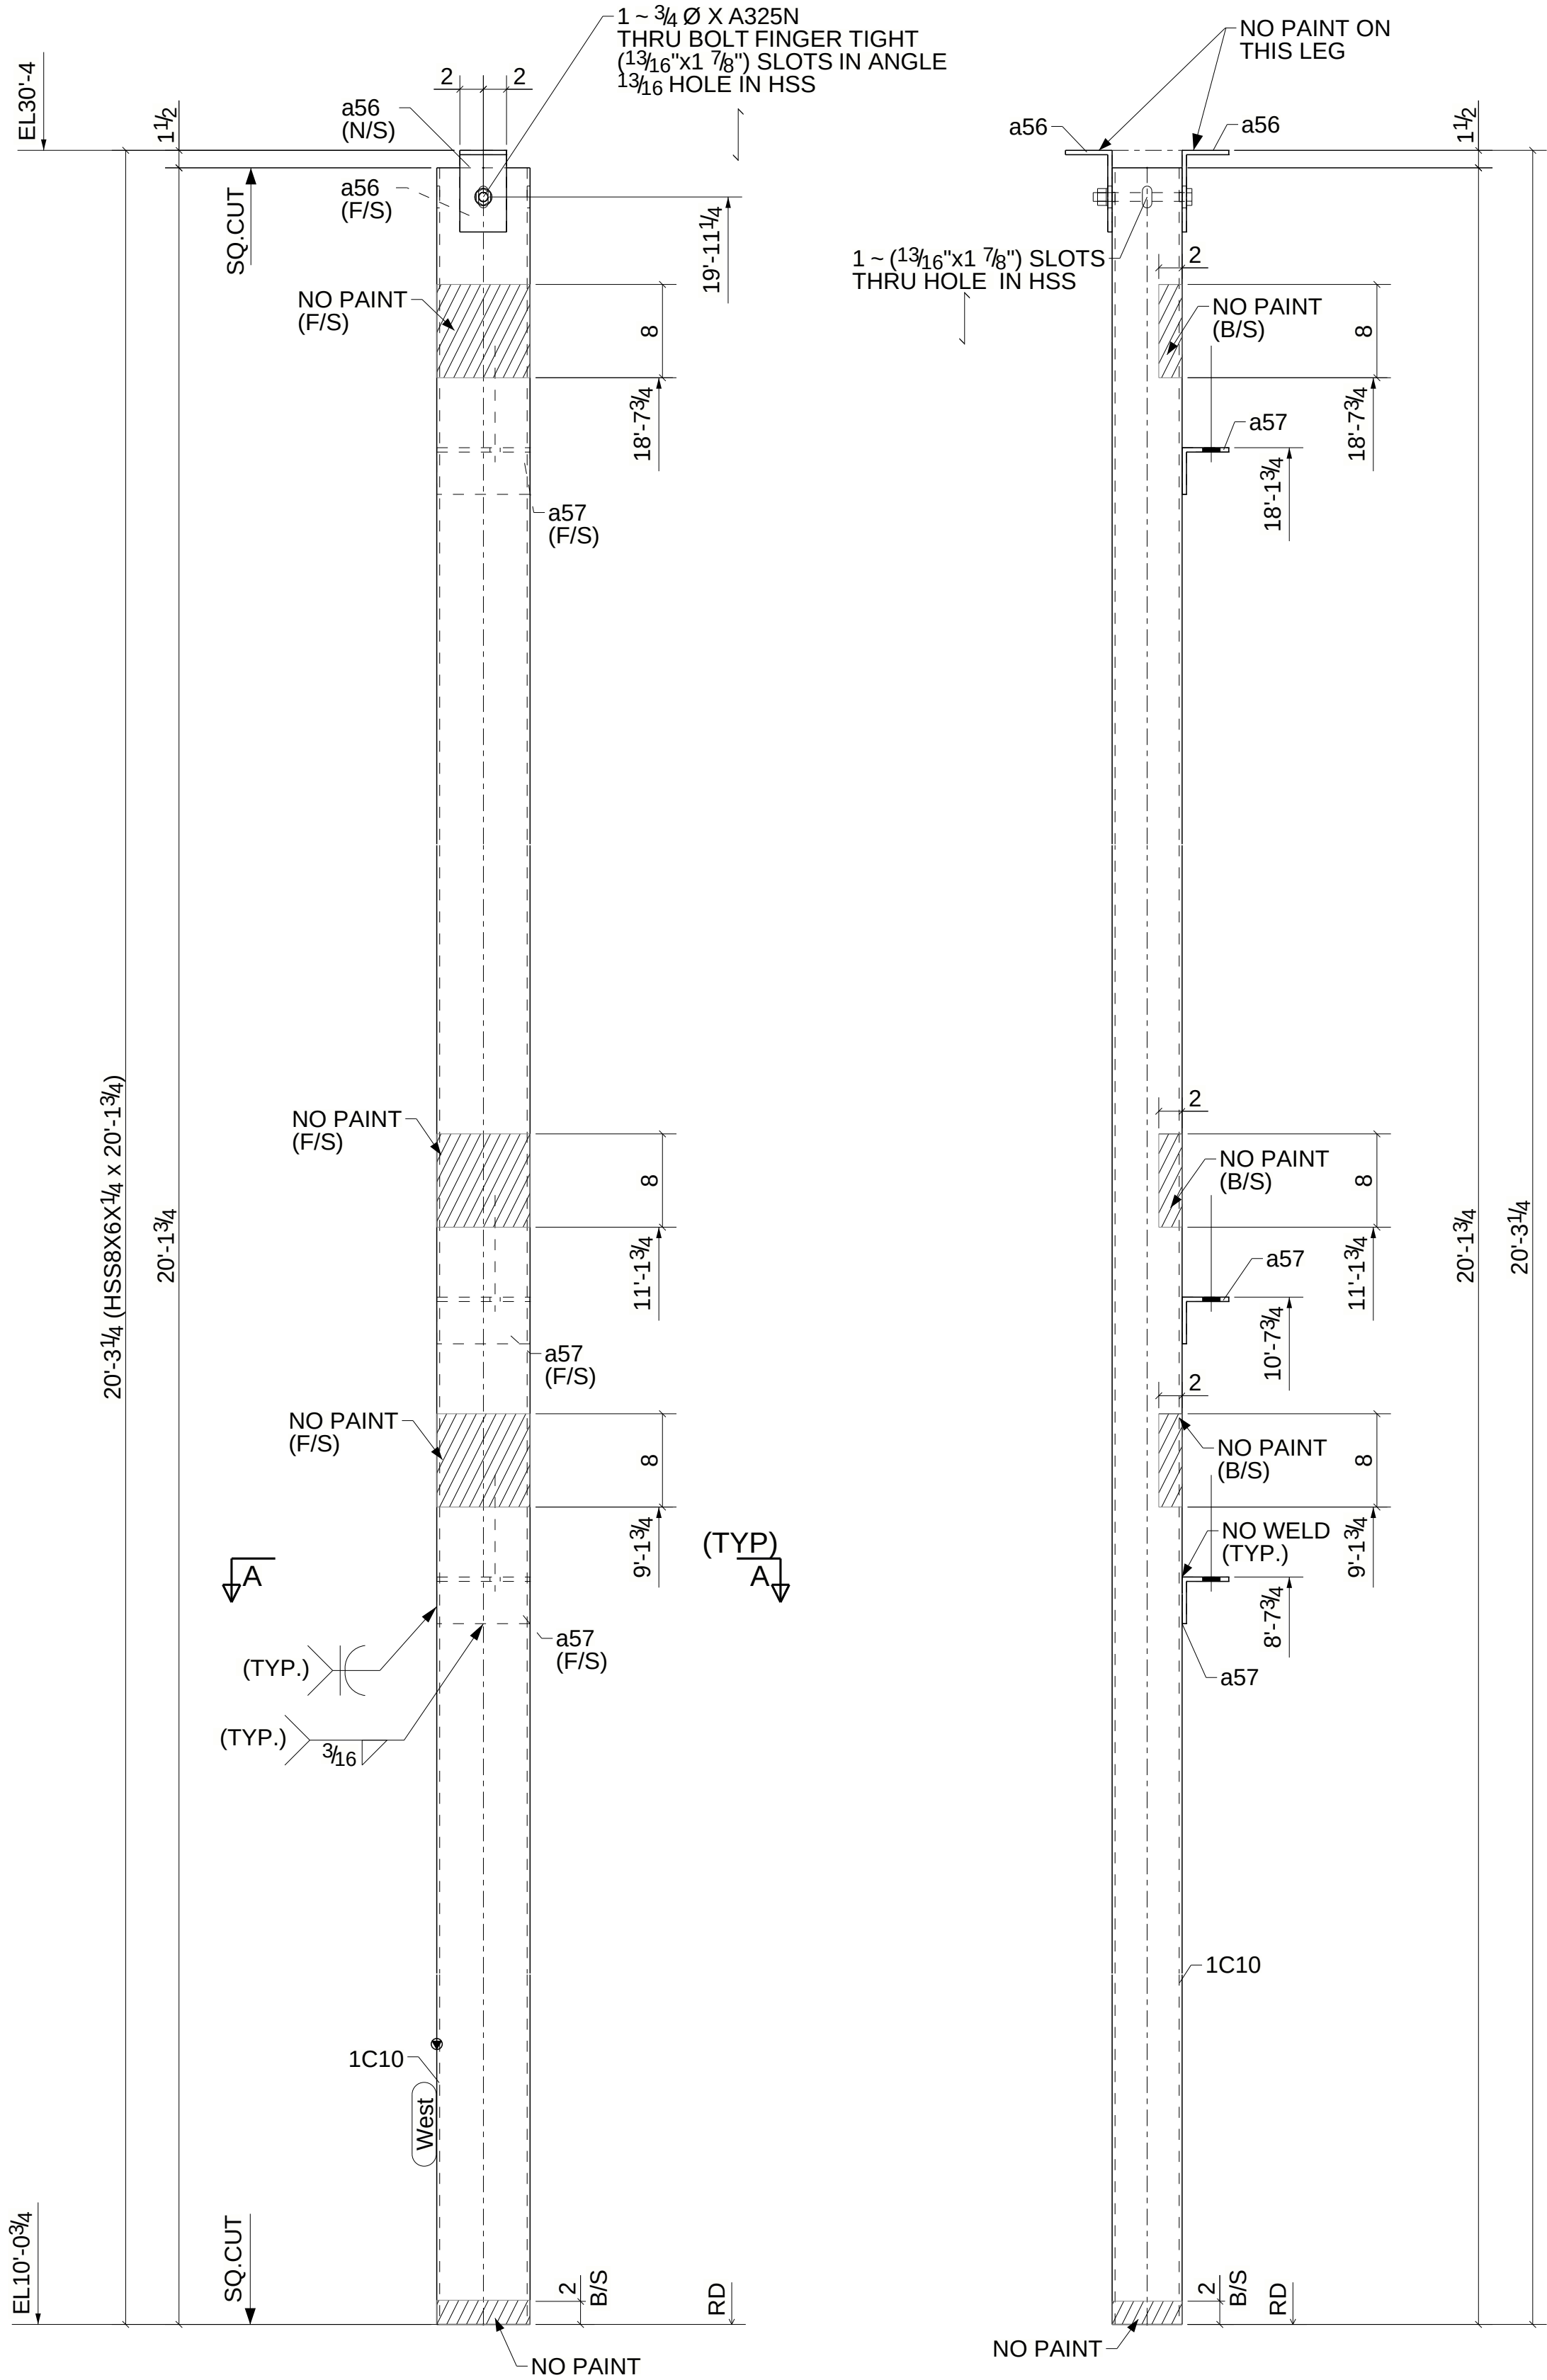

2 - COLUMNS - 1C10

0	04/11/2025	For Fabrication	PROJECT NAME GSC JUNIPER RBP PHASE-II			
A	10/16/2024	For Approval				
REV.	DATE	DESCRIPTION				
MATERIAL A36 UNO			LOCATION PARKWAY EVERETT, MA			
HOLES 13/16Ø UNO			CONTRACTOR BUILDING ENVELOPE SYSTEMS			
WELDS E70XX			DWG TITLE COLUMN			
SURFACE PREP. SSPC SP2		DRAWN BY ABJ	CHECKED BY HSR	DATE DRAWN 10/15/2024	PLOT DATE 10/15/2024	DGSTS No. --
PAINT NOTE: SW SHOP PRIMER		CONTRACT No. 24050			DWG No. 1C10	REV. 0

Building Envelope Systems



20 HIGH STREET
PLAINSVILLE, MA 02762
PHONE (508) 381-0429
www.teambes.com