
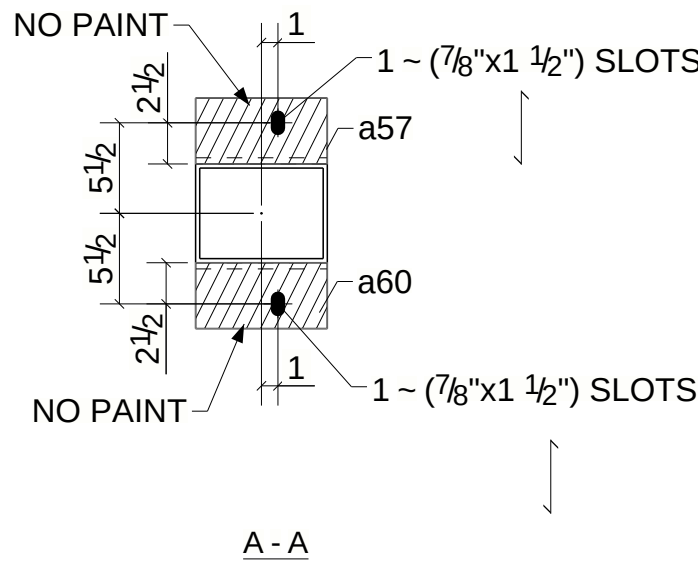


BILL OF MATERIAL							
MARK	TOTAL QTY	SHAPE	LENGTH	TOTAL WEIGHT	REMARKS	ADV MILL #	STEEL GRADE
1C11	1	HSS8X6X1/4	20'-1 7/8"	423	SQ-2		A500-GR B
a56	2	L7X4X3/8	0'-4"	9			A36
a57	3	L4X4X3/8	0'-8"	19			A36
a60	3	L4X4X3/8	0'-8"	19			A36
	1	3/4"Ø A325N BOLT	0'-8"	1	Workshop		

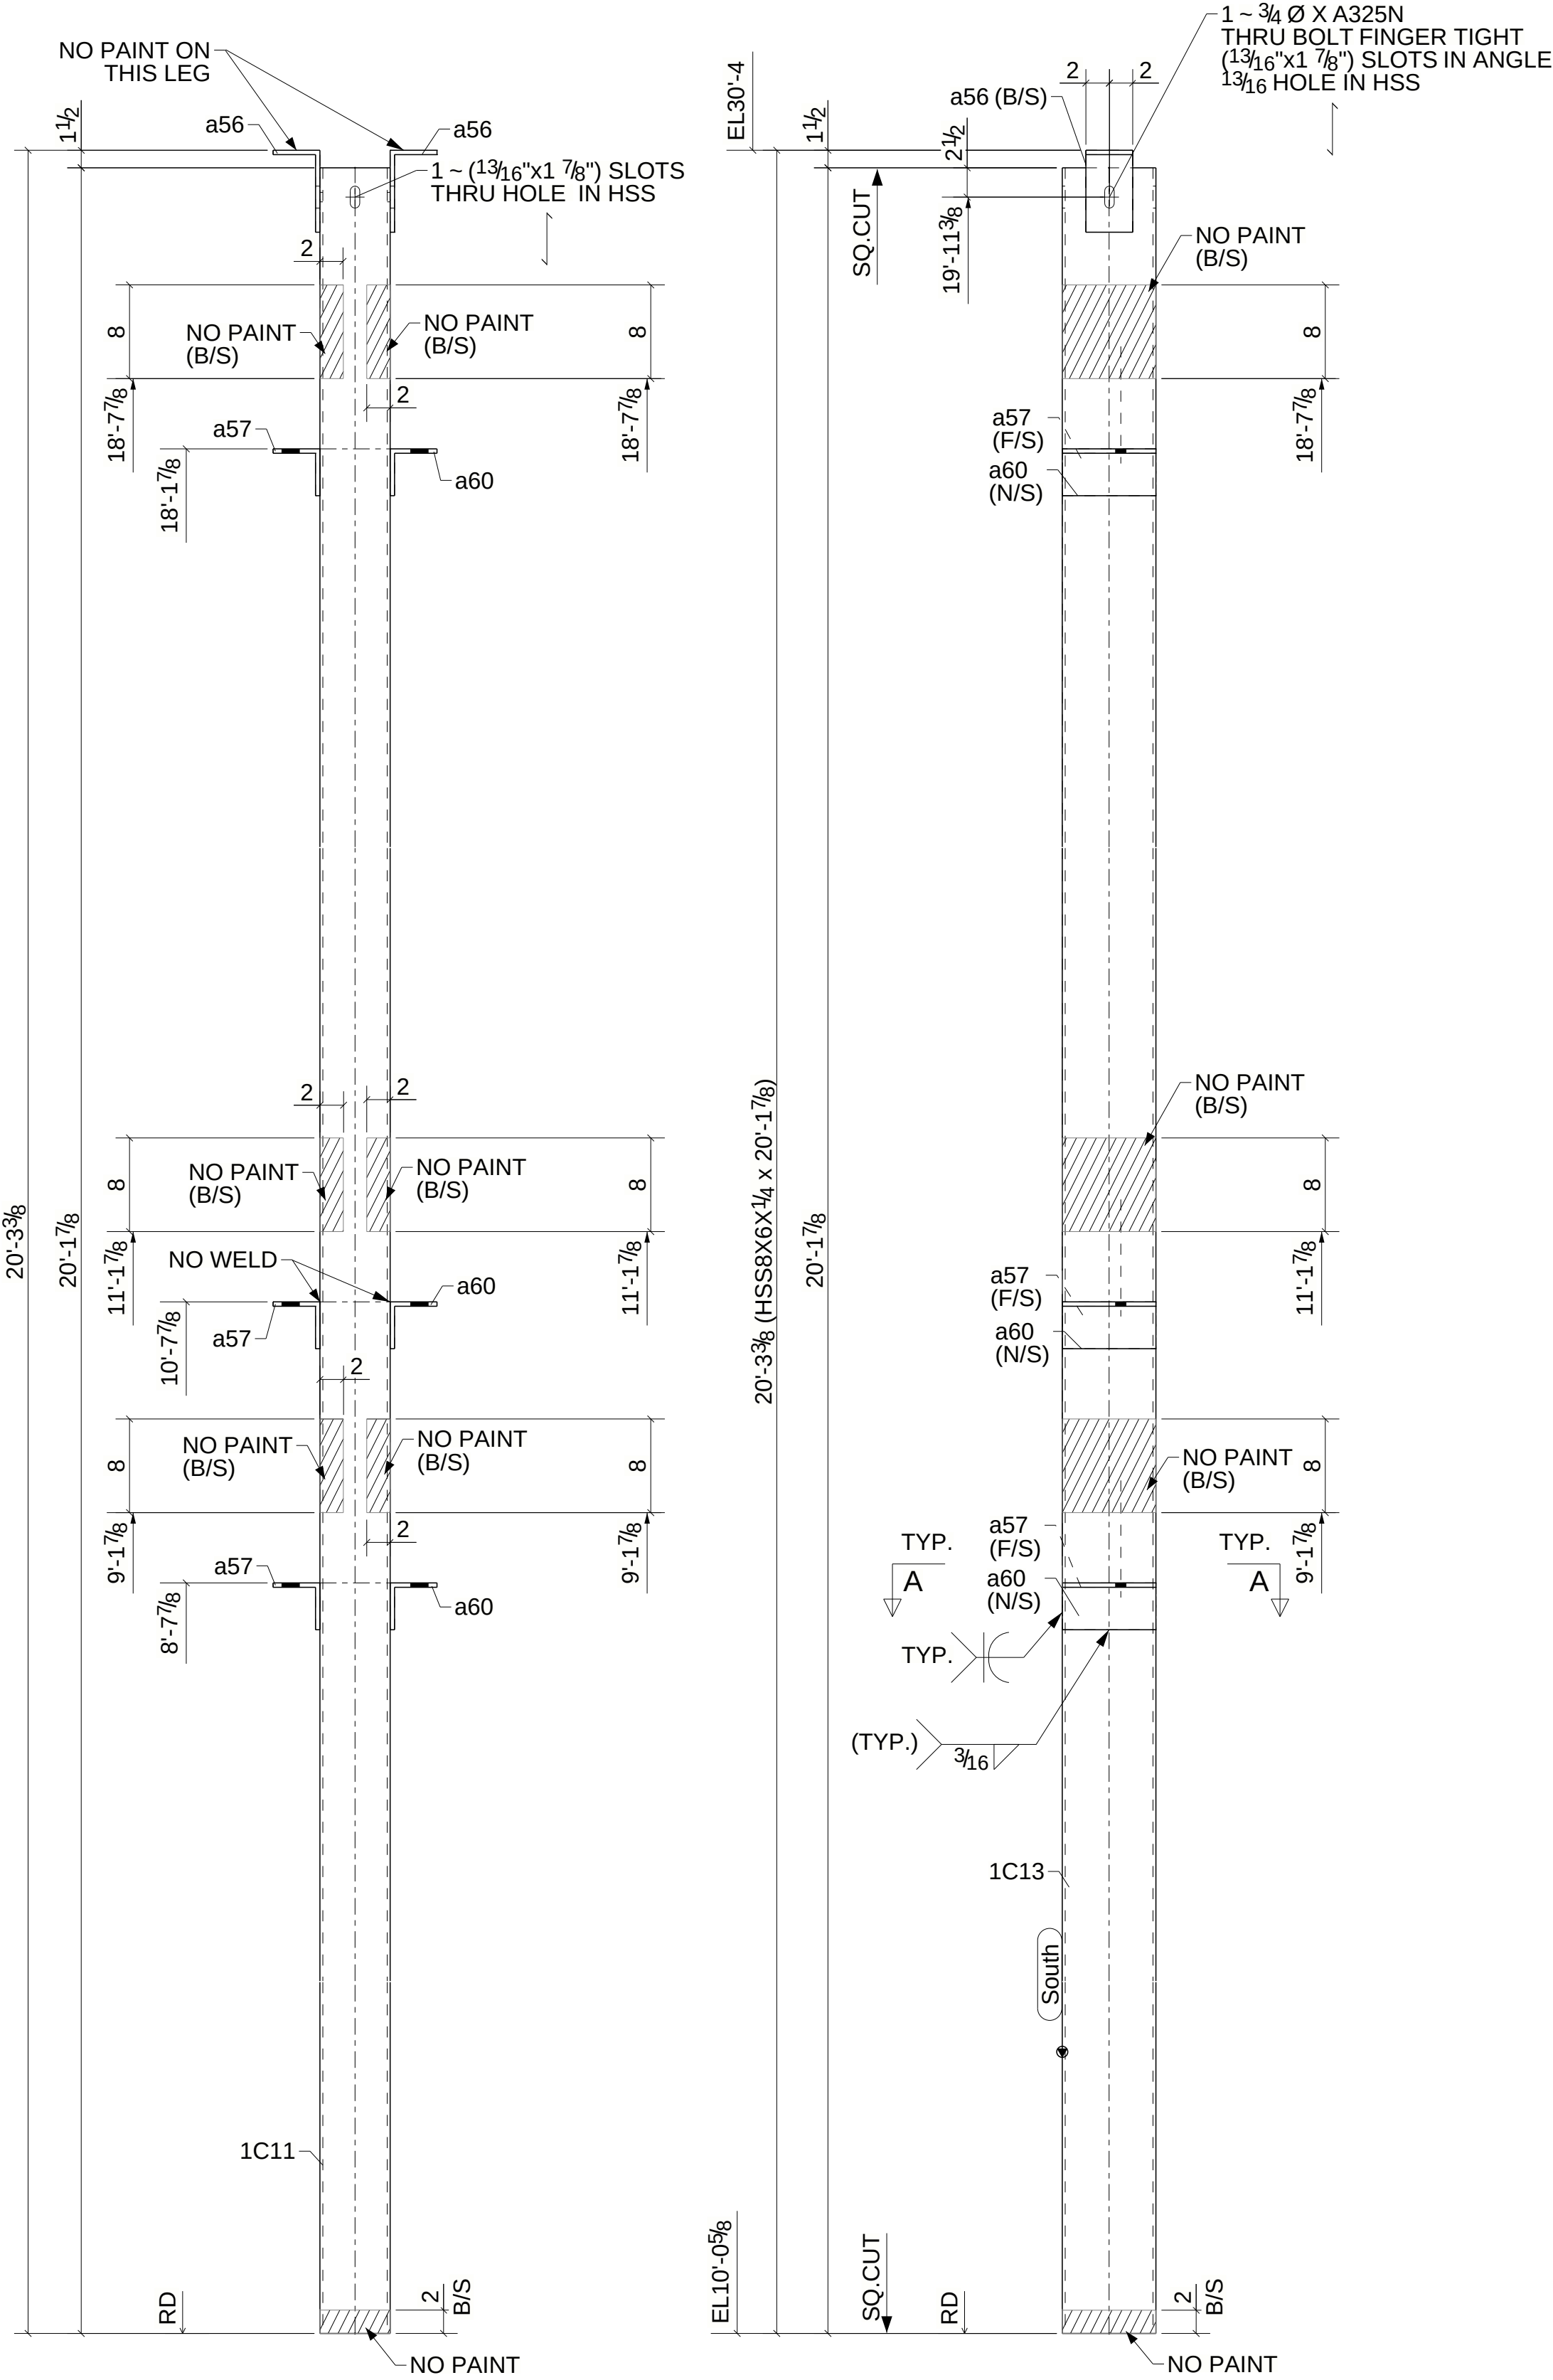

GRID LOCATION	BOTTOM ELEVATION
102-101/***	10'-0"5/8

0	04/11/2025	For Fabrication
A	10/16/2024	For Approval
REV.	DATE	DESCRIPTION
MATERIAL A36 UNO		
HOLES 13/16Ø UNO		
WELDS E70XX		
SURFACE PREP. SSPC SP2		
PAINT NOTE: SW SHOP PRIMER		

Building Envelope Systems		20 HIGH STREET PLAINSVILLE, MA 02762 PHONE (508) 381-0429 www.teambes.com			
PROJECT NAME GSC JUNIPER RBP PHASE-II					
LOCATION PARKWAY EVERETT, MA					
CONTRACTOR BUILDING ENVELOPE SYSTEMS					
DWG TITLE COLUMN					
DRAWN BY ABJ	CHECKED BY HSR	DATE DRAWN 10/15/2024	REV. 0		
CONTRACT No. 24050		DWG No. 1C11			