
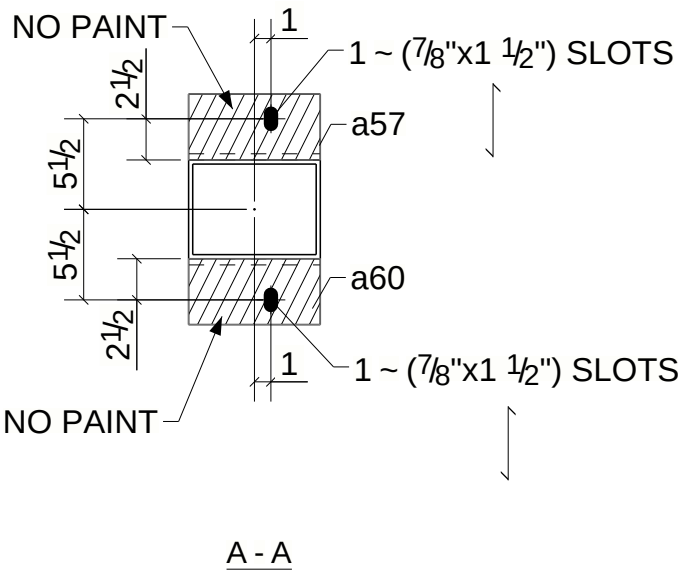


BILL OF MATERIAL							
MARK	TOTAL QTY	SHAPE	LENGTH	TOTAL WEIGHT	REMARKS	ADV MILL #	STEEL GRADE
1C13	1	HSS8X6X1/4	20'-1 3/4"	423	SQ-2		A500-GR B
a56	2	L7X4X3/8	0'-4"	9			A36
a57	3	L4X4X3/8	0'-8"	19			A36
a60	3	L4X4X3/8	0'-8"	19			A36
	1	3/4"Ø A325N BOLT	0'-8"	1	Workshop		

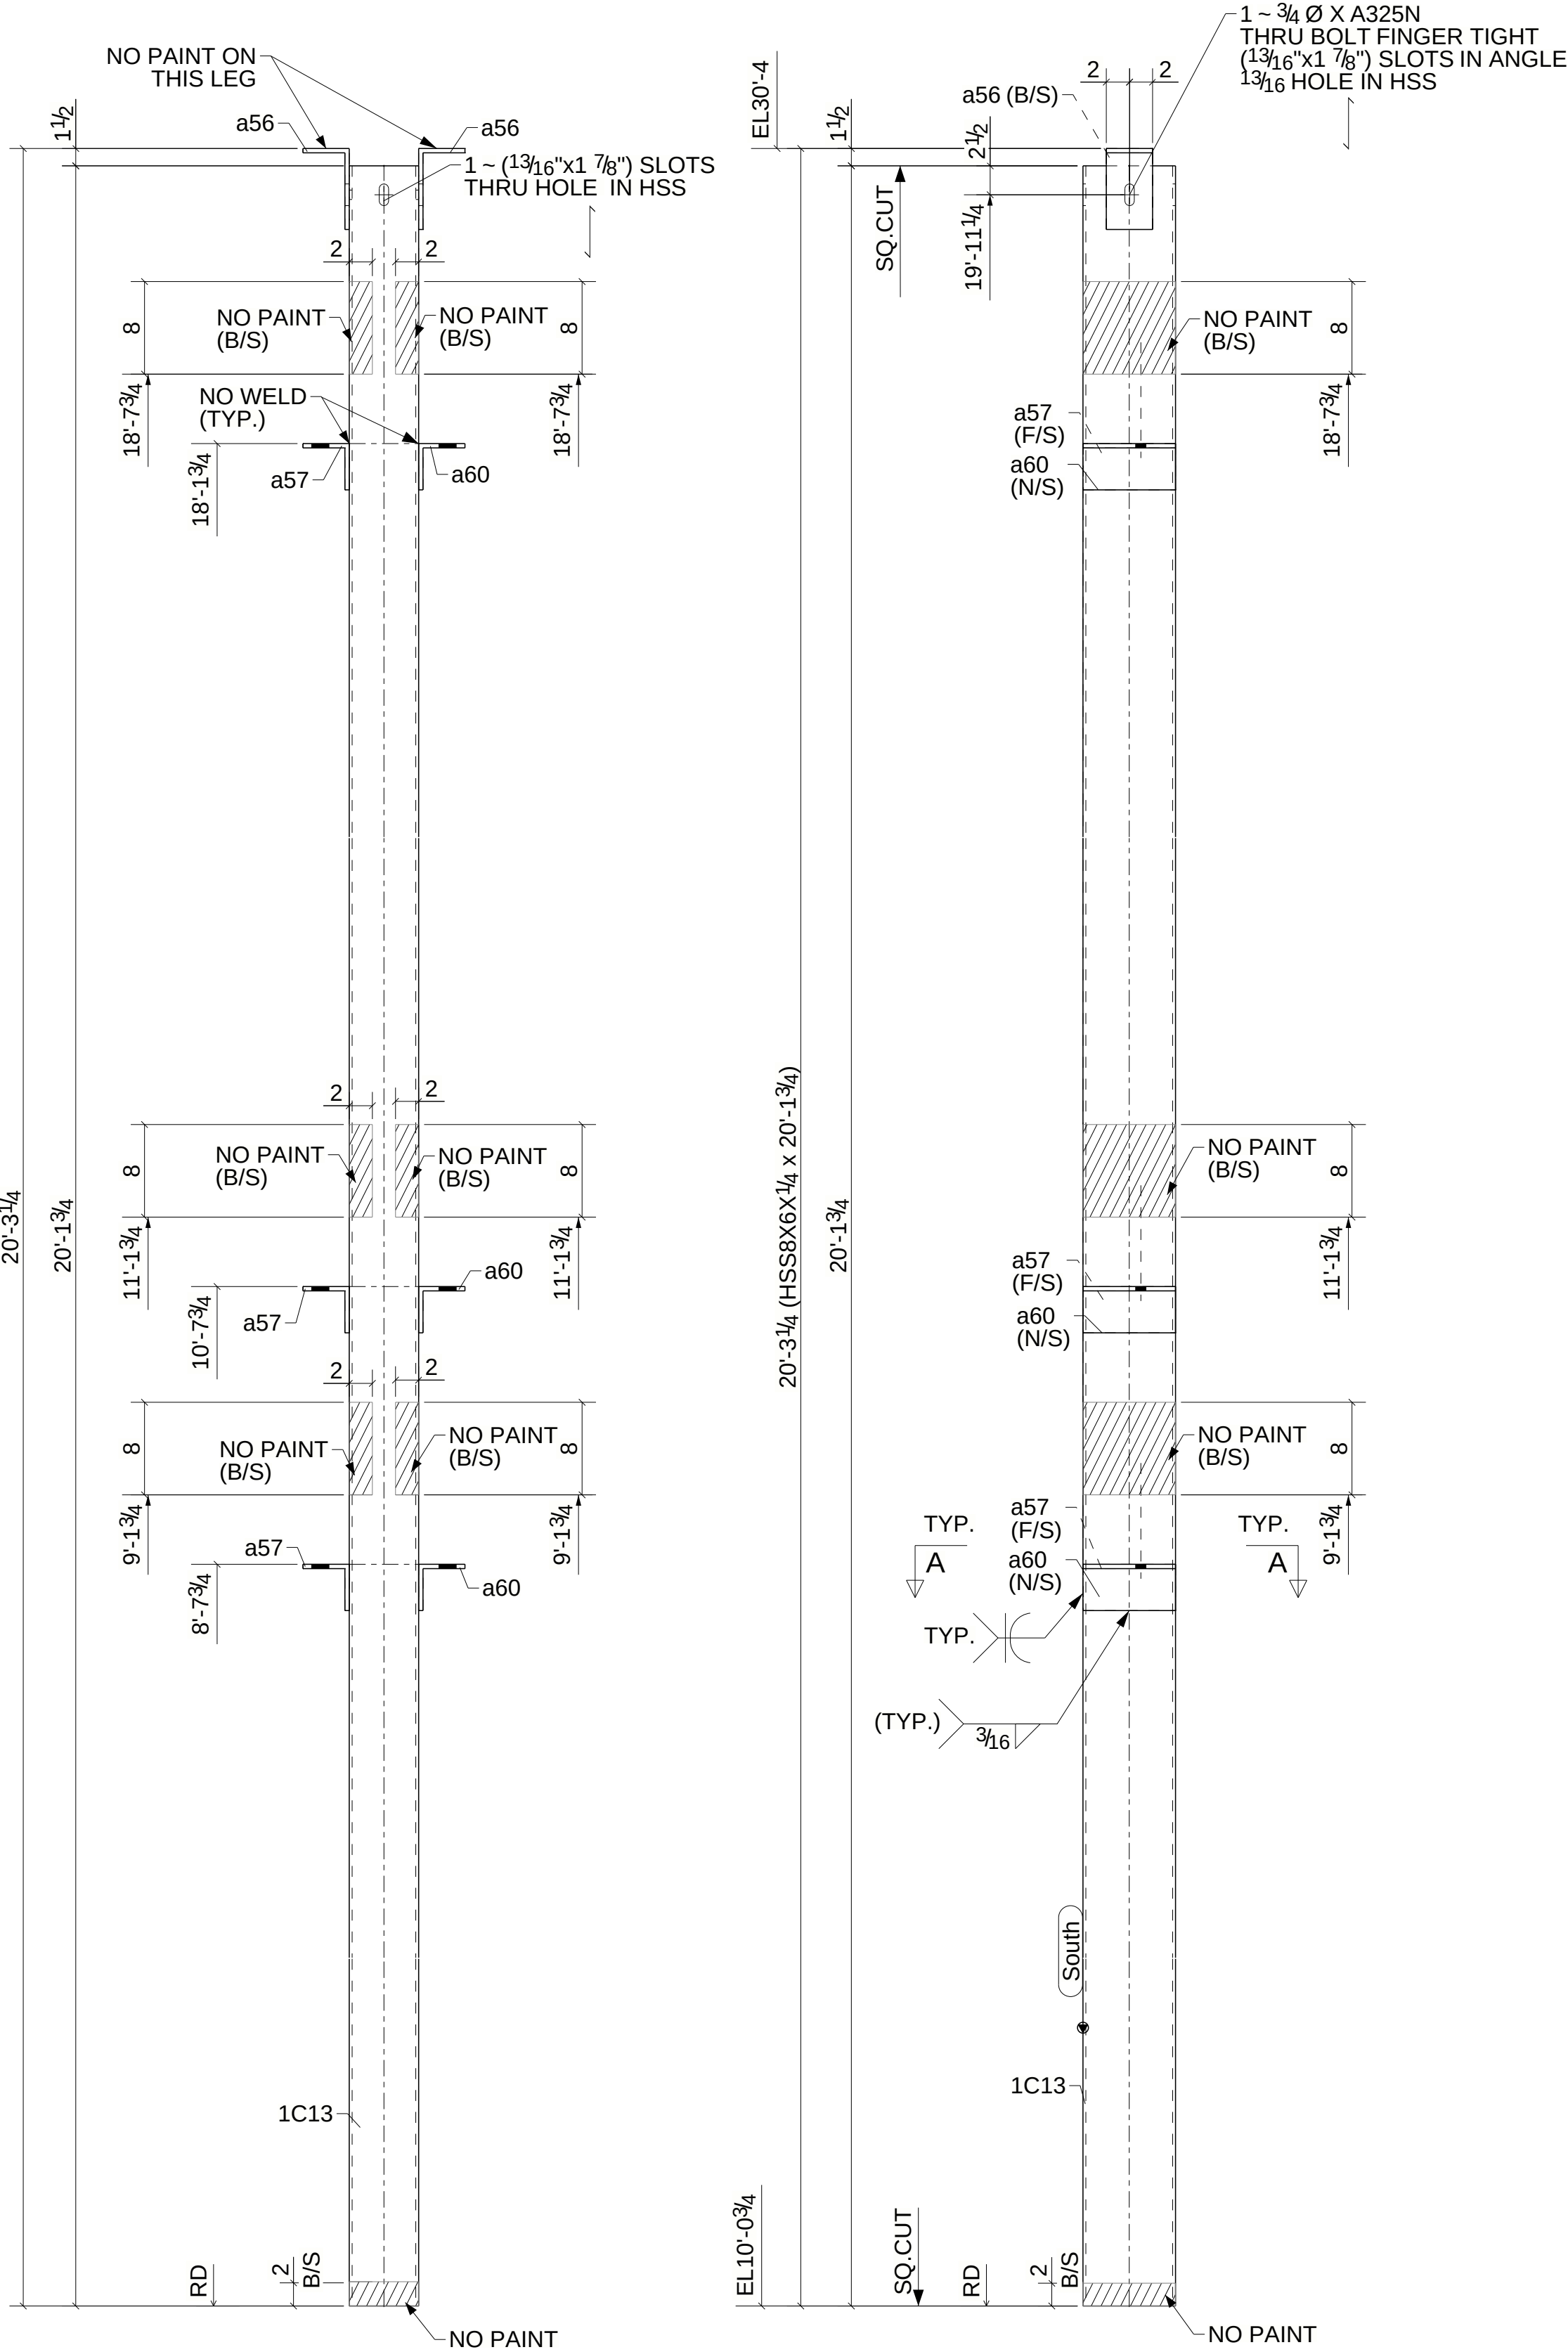

ONE - COLUMN - 1C13

0	04/11/2025	For Fabrication
A	10/16/2024	For Approval
REV.	DATE	DESCRIPTION
MATERIAL	A36 UNO	
HOLES	13/16Ø UNO	
WELDS	E70XX	
SURFACE PREP.	SSPC SP2	
PAINT NOTE:	SW SHOP PRIMER	

<