


Tekla Structures

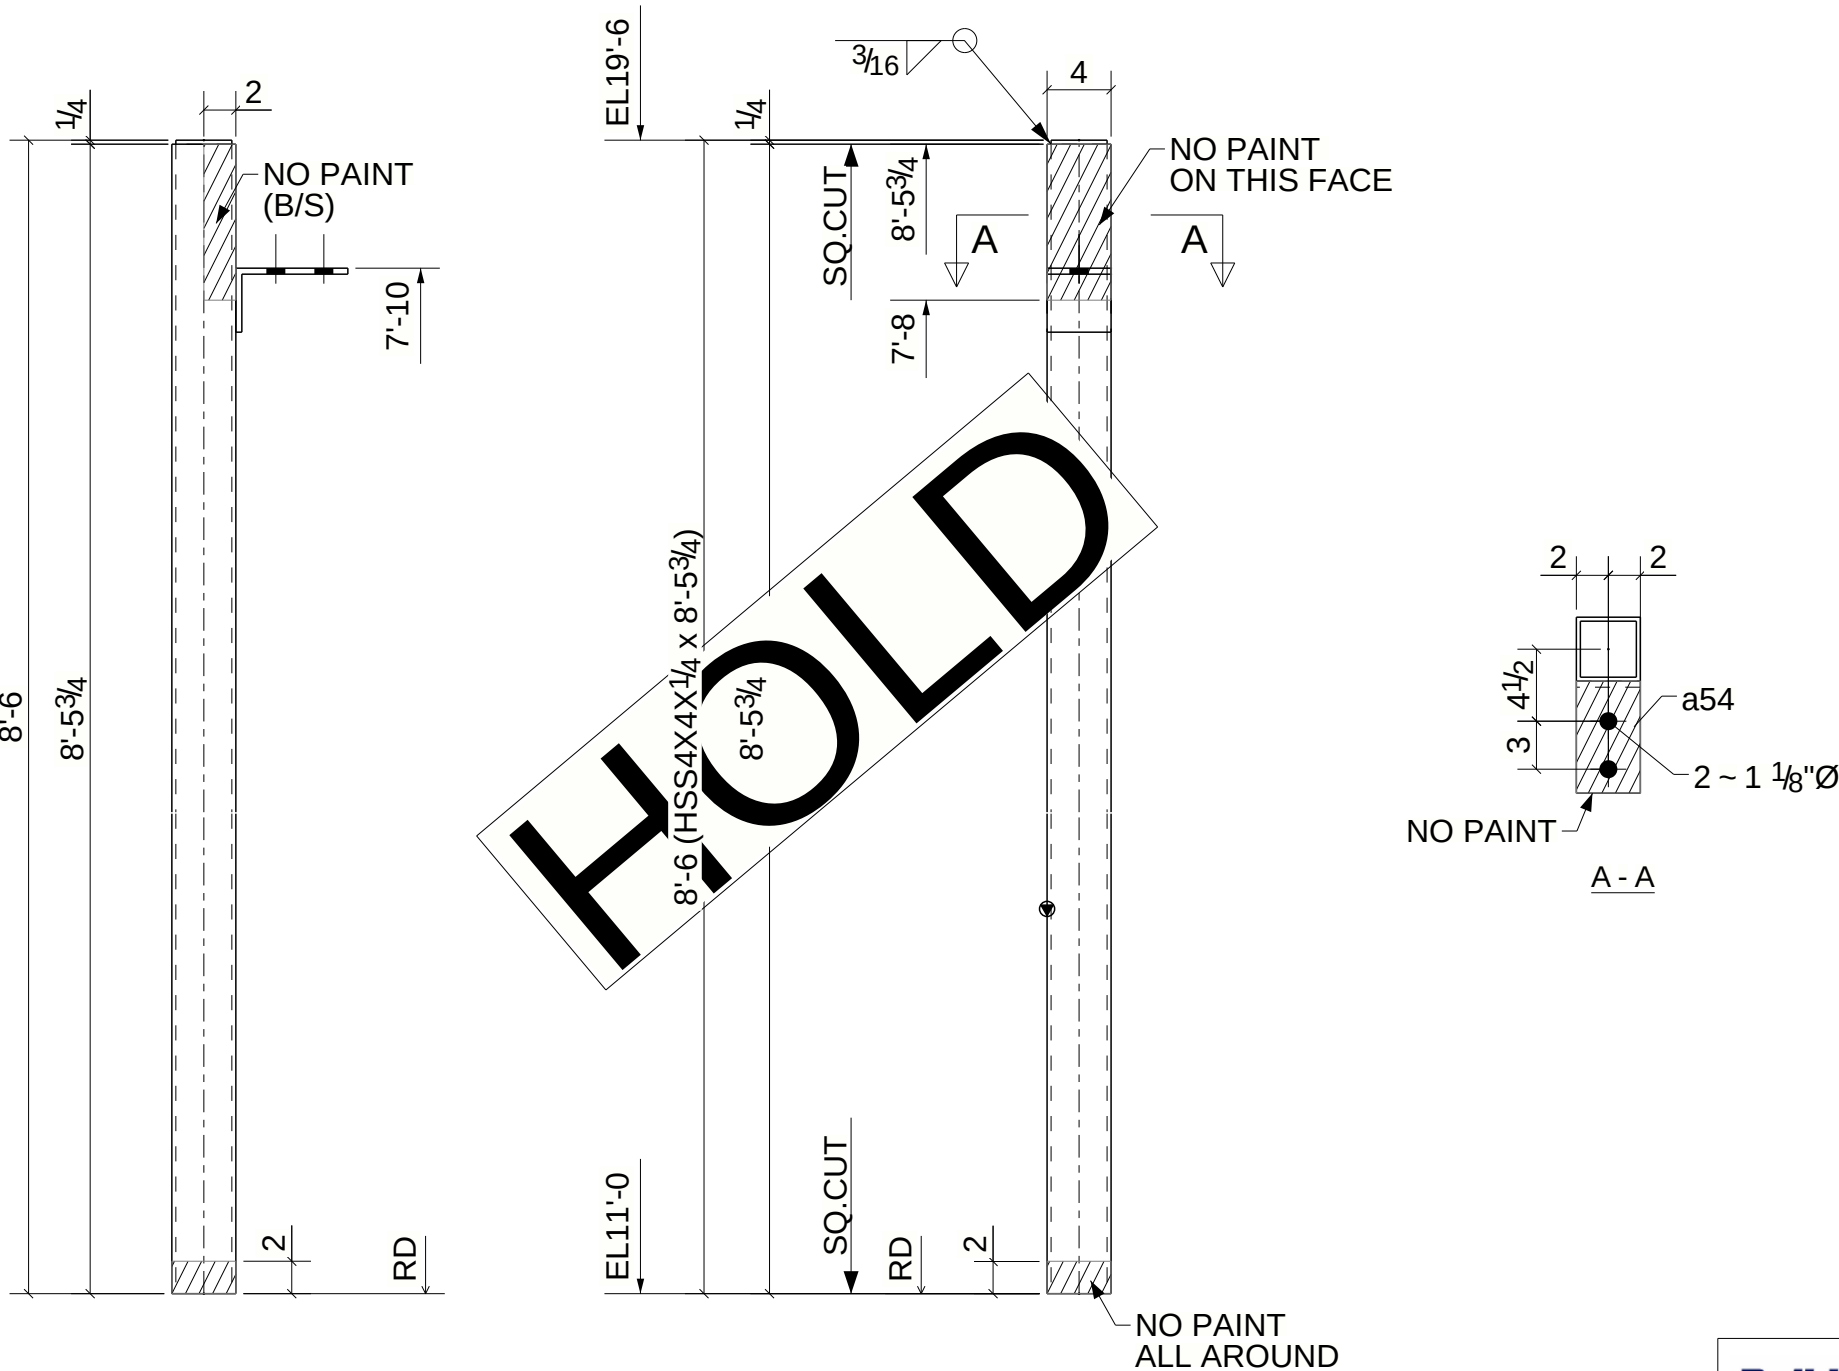

GRID LOCATION	BOTTOM ELEVATION
102-101/<XX	11'-0"



20 HIGH STREET
PLAINSVILLE, MA 02762
PHONE (508) 381-0429
www.teambes.com

0	04/11/2025	For Fabrication	PROJECT NAME			
A	10/16/2024	For Approval	GSC JUNIPER RBP PHASE-II			
REV.	DATE	DESCRIPTION	LOCATION			
MATERIAL A36 UNO			PARKWAY EVERETT, MA			
HOLES 13/16Ø UNO			CONTRACTOR			
WELDS E70XX			BUILDING ENVELOPE SYSTEMS			
SURFACE PREP. SSPC SP2			DWG TITLE			
PAINT NOTE : SW SHOP PRIMER			COLUMN			
			DRAWN BY ABJ	CHECKED BY HSR	DATE DRAWN 10/15/2024	PLOT DATE 10/15/2024
			CONTRACT No. 24050		DWG No. 1C18	DGSTS No. --
						REV. 0

BILL OF MATERIAL

MARK	TOTAL QTY	SHAPE	LENGTH	TOTAL WEIGHT	REMARKS	ADV MILL #	STEEL GRADE
1C18	1	HSS4X4X1/4	8'-5 3/4"	97	SQ-2		A500-GR.B
a54	1	L7X4X3/8	0'-4"	5			A36
p131	1	PL1/4"X3 1/2"	0'-3 1/2"	1			A36