



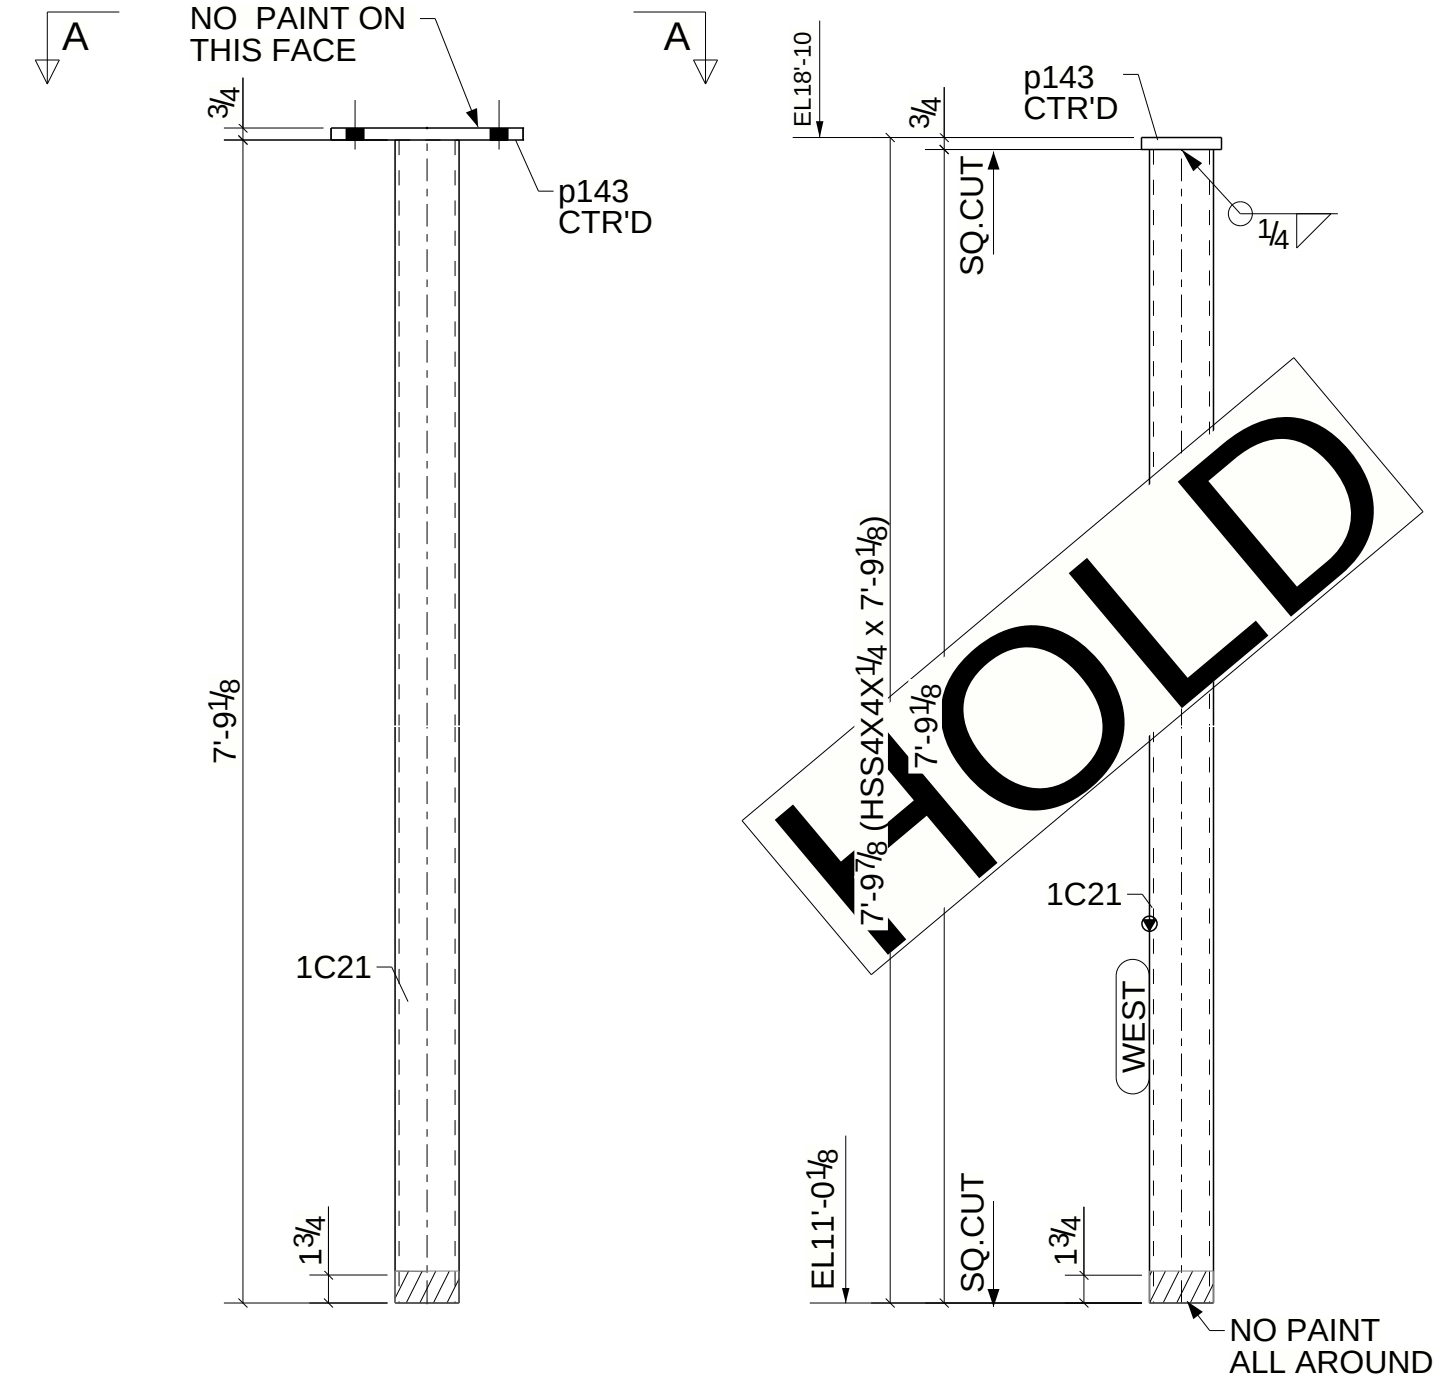

ONE - COLUMN - 1C21

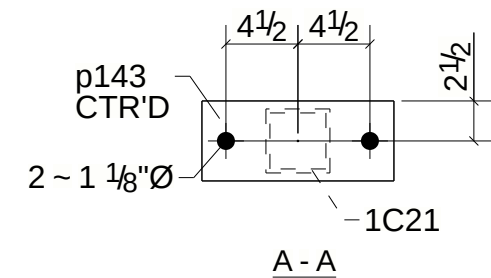

| GRID LOCATION | BOTTOM ELEVATION |
|---------------|------------------|
| 102.5-10***   | 11'-0"1/8        |

**Building Envelope Systems**

20 HIGH STREET  
PLAINSVILLE, MA 02762  
PHONE (508) 381-0429  
www.teambes.com

PROJECT NAME  
GSC JUNIPER RBP PHASE-II

LOCATION  
PARKWAY EVERETT, MA

CONTRACTOR  
BUILDING ENVELOPE SYSTEMS

DWG TITLE  
COLUMN

DRAWN BY  
CHECKED BY  
DATE DRAWN  
PLOT DATE  
DGSTS No.  
REV.

CONTRACT No. 24050  
DWG No. 1C21  
0

| 0                   | 04/11/2025 | For Fabrication |
|---------------------|------------|-----------------|
| REV.                | DATE       | DESCRIPTION     |
| MATERIAL<br>A36 UNO |            |                 |
| HOLES<br>13/16Ø UNO |            |                 |
| WELDS<br>E70XX      |            |                 |
| SURFACE PREP.       |            |                 |
| PAINT NOTE :        |            |                 |

| BILL OF MATERIAL |           |            |           |              |         |            |             |
|------------------|-----------|------------|-----------|--------------|---------|------------|-------------|
| MARK             | TOTAL QTY | SHAPE      | LENGTH    | TOTAL WEIGHT | REMARKS | ADV MILL # | STEEL GRADE |
| 1C21             | 1         | HSS4X4X1/4 | 7'-9 1/8" | 89           | SQ-2    |            | A500-GR.B   |
| p143             | 1         | PL3/4"X5"  | 1'-0"     | 13           |         |            | A36         |