


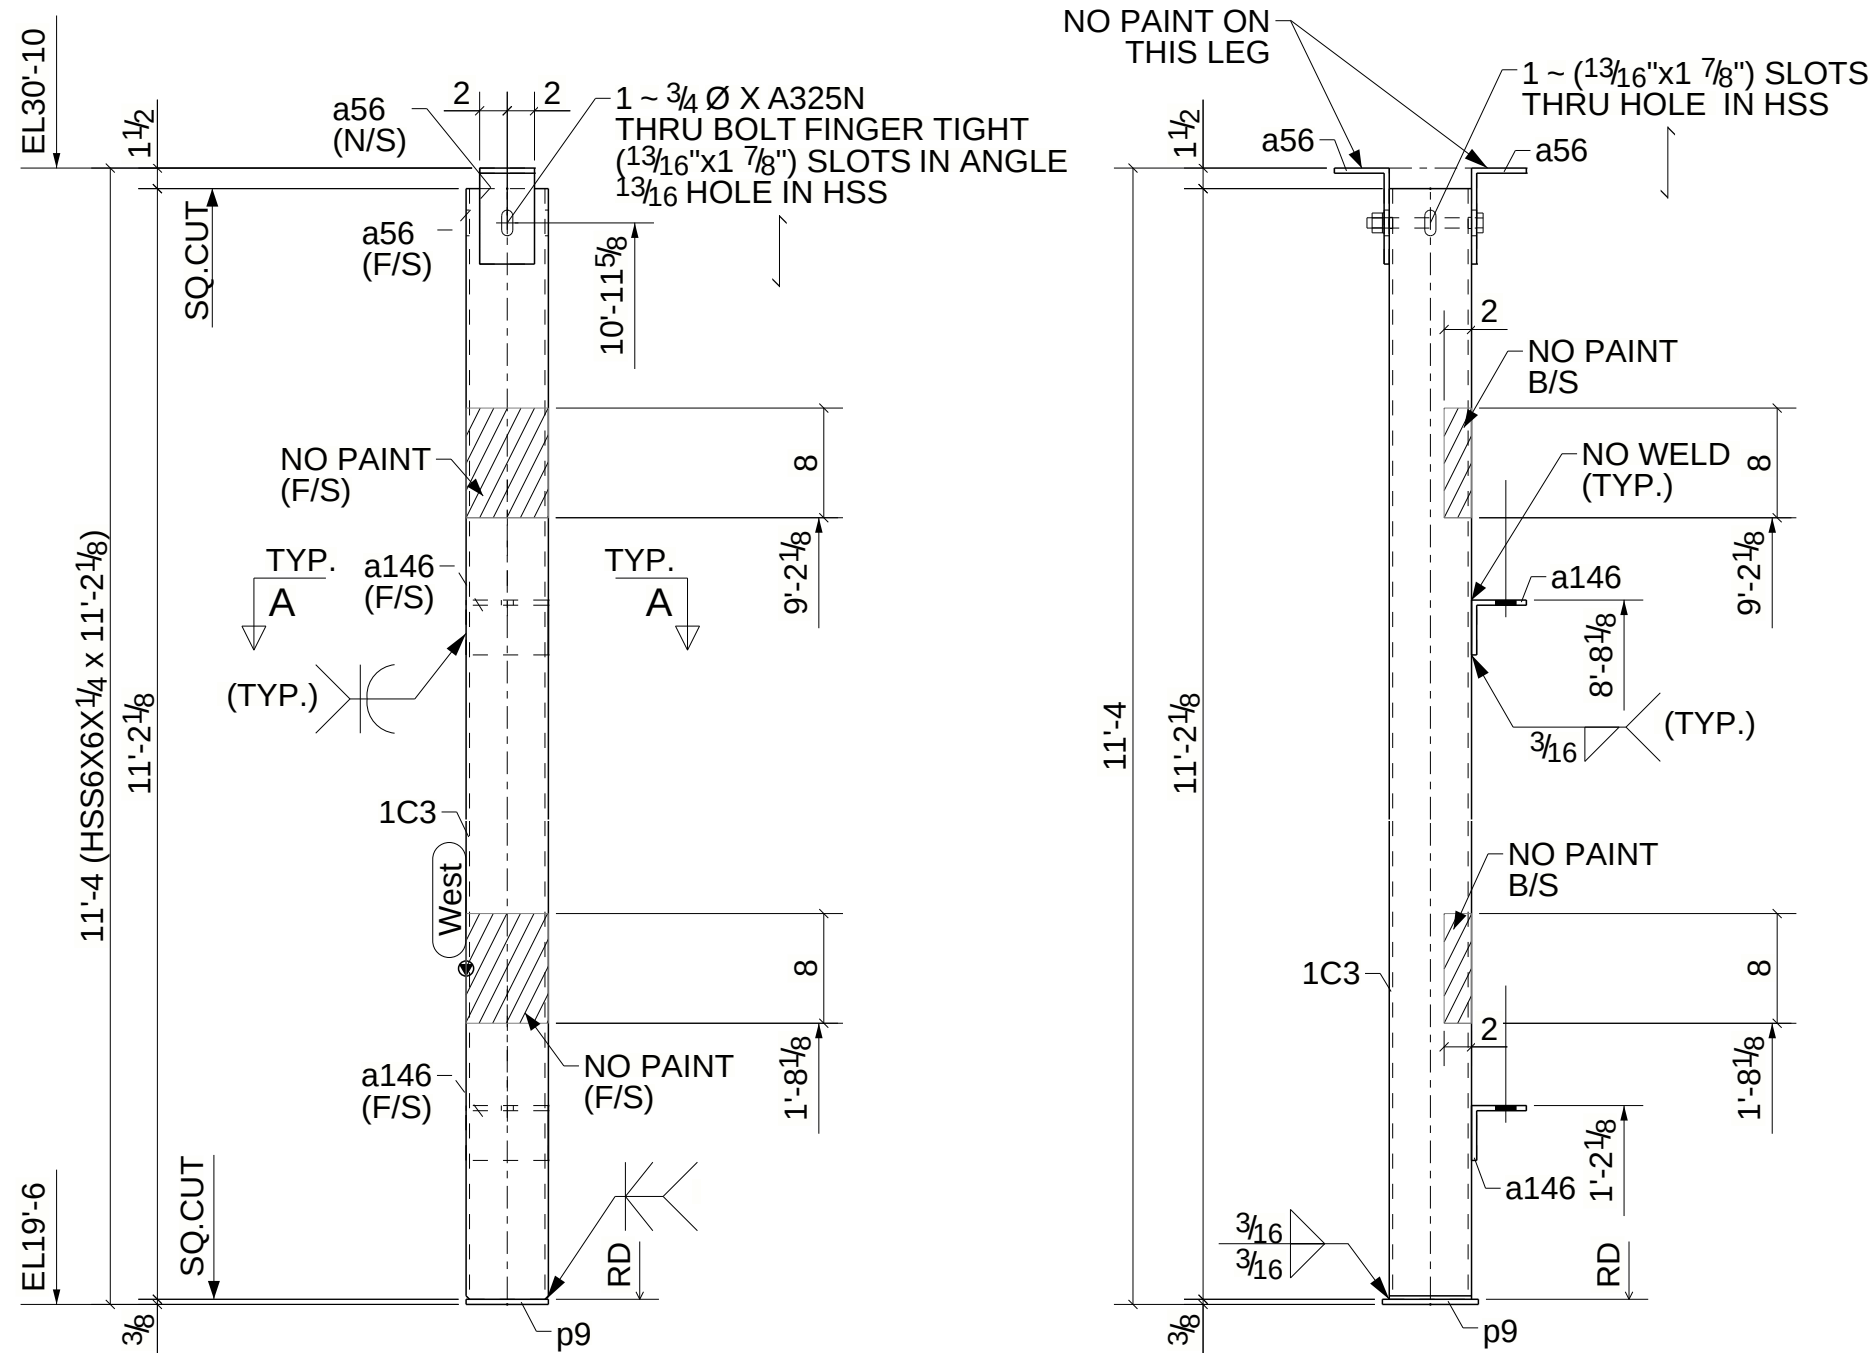

ONE - COLUMN - 1C3

BILL OF MATERIAL

MARK	TOTAL QTY	SHAPE	LENGTH	TOTAL WEIGHT	REMARKS	ADV MILL #	STEEL GRADE
1C3	1	HSS6X6X1/4	11'-2 1/8"	199	SQ-2		A500-GR.B
a56	2	L7X4X3/8	0'-4"	9			A36
a146	2	L4X4X3/8	0'-6"	10			A36
p9	1	PL3/8"X6"	0'-7"	4			A36
	1	3/4"Ø A325N BOLT	0'-8"	1	Workshop		

0	04/11/2025	For Fabrication
A	10/16/2024	For Approval
REV.	DATE	DESCRIPTION
MATERIAL A36 UNO		
HOLES 13/16Ø UNO		
WELDS E70XX		
SURFACE PREP. SSPC SP2		
PAINT NOTE : SW SHOP PRIMER		

Building Envelope Systems 		20 HIGH STREET PLAINSVILLE, MA 02762 PHONE (508) 381-0429 www.teambes.com			
PROJECT NAME GSC JUNIPER RBP PHASE-II					
LOCATION PARKWAY EVERETT, MA					
CONTRACTOR BUILDING ENVELOPE SYSTEMS					
DWG TITLE COLUMN					
DRAWN BY ABJ		CHECKED BY HSR	DATE DRAWN 10/15/2024	PLOT DATE 10/15/2024	DGSTS No. --
CONTRACT No. 24050			DWG No. 1C3		REV. 0

GRID LOCATION	BOTTOM ELEVATION
5-4/U.5-V	19'-6"