

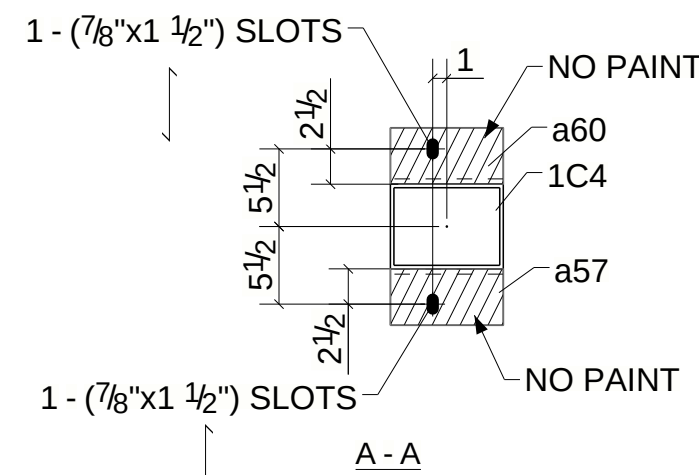
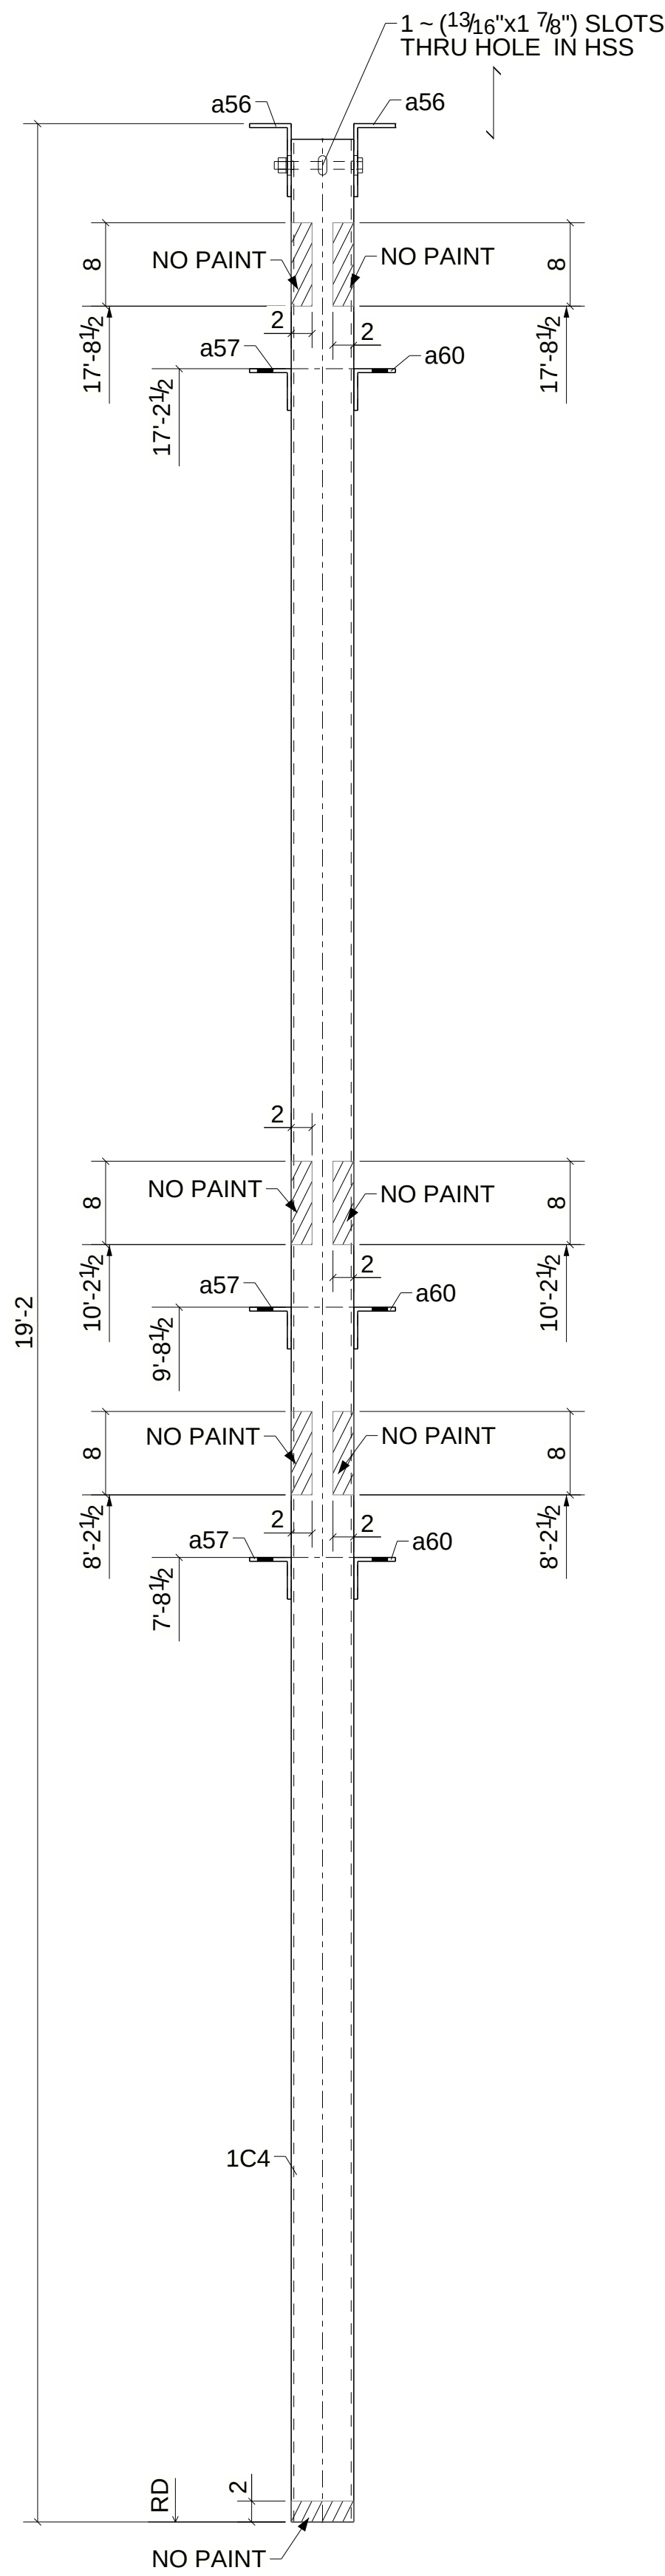


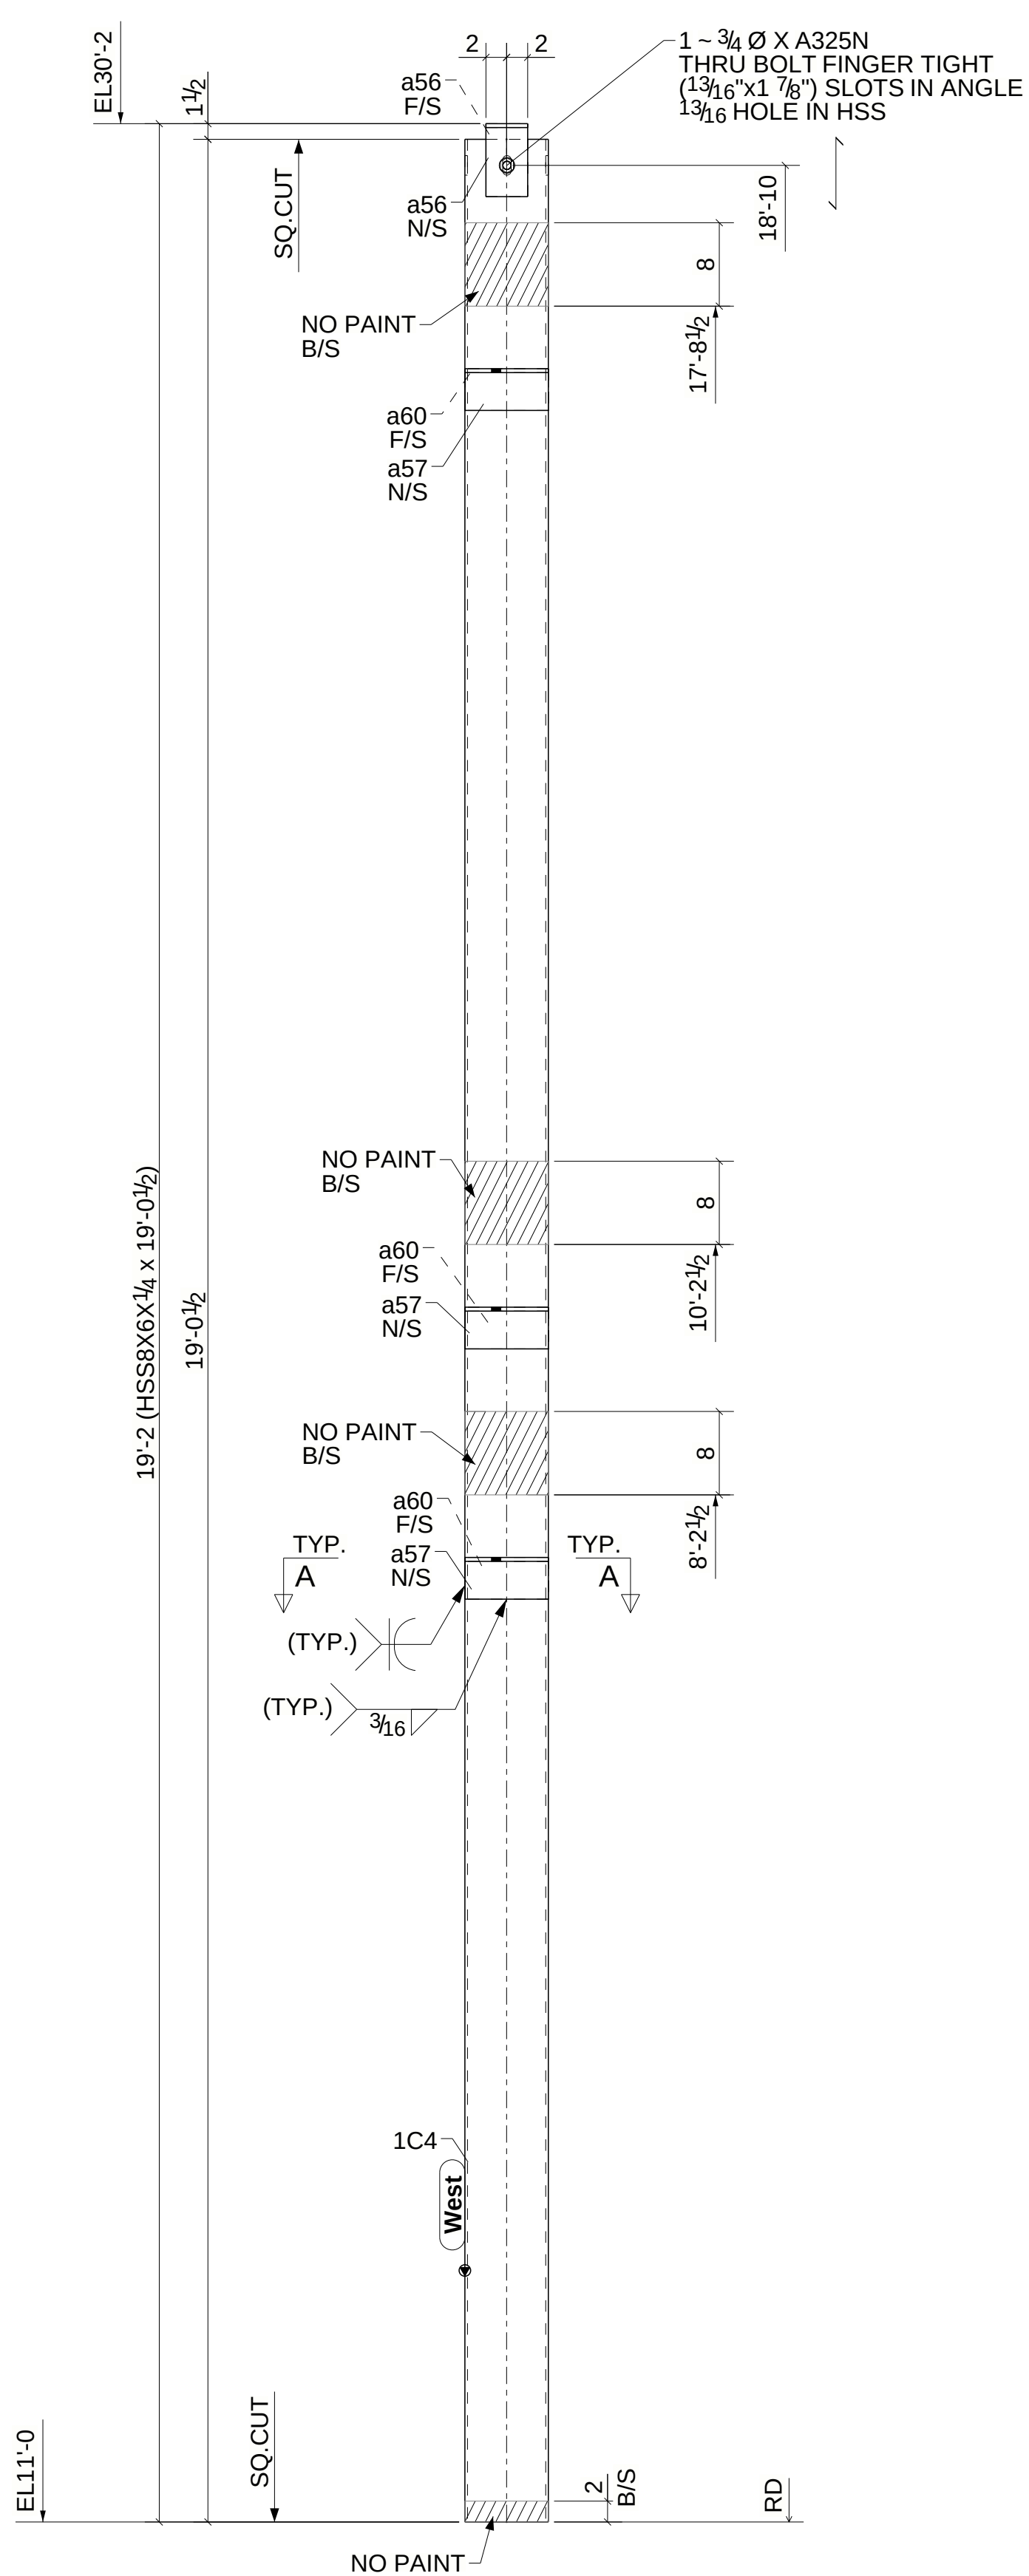

BILL OF MATERIAL

MARK	TOTAL QTY	SHAPE	LENGTH	TOTAL WEIGHT	REMARKS	ADV MILL #	STEEL GRADE
1C4	1	HSS8X6X1/4	19'-0 1/2"	400	SQ-2		A500-GR B
a56	2	L7X4X3/8	0'-4"	9			A36
a57	3	L4X4X3/8	0'-8"	19			A36
a60	3	L4X4X3/8	0'-8"	19			A36
	1	3/4"Ø A325N BOLT	0'-8"	1	Workshop		

GRID LOCATION	BOTTOM ELEVATION
<103/YY	11'-0"

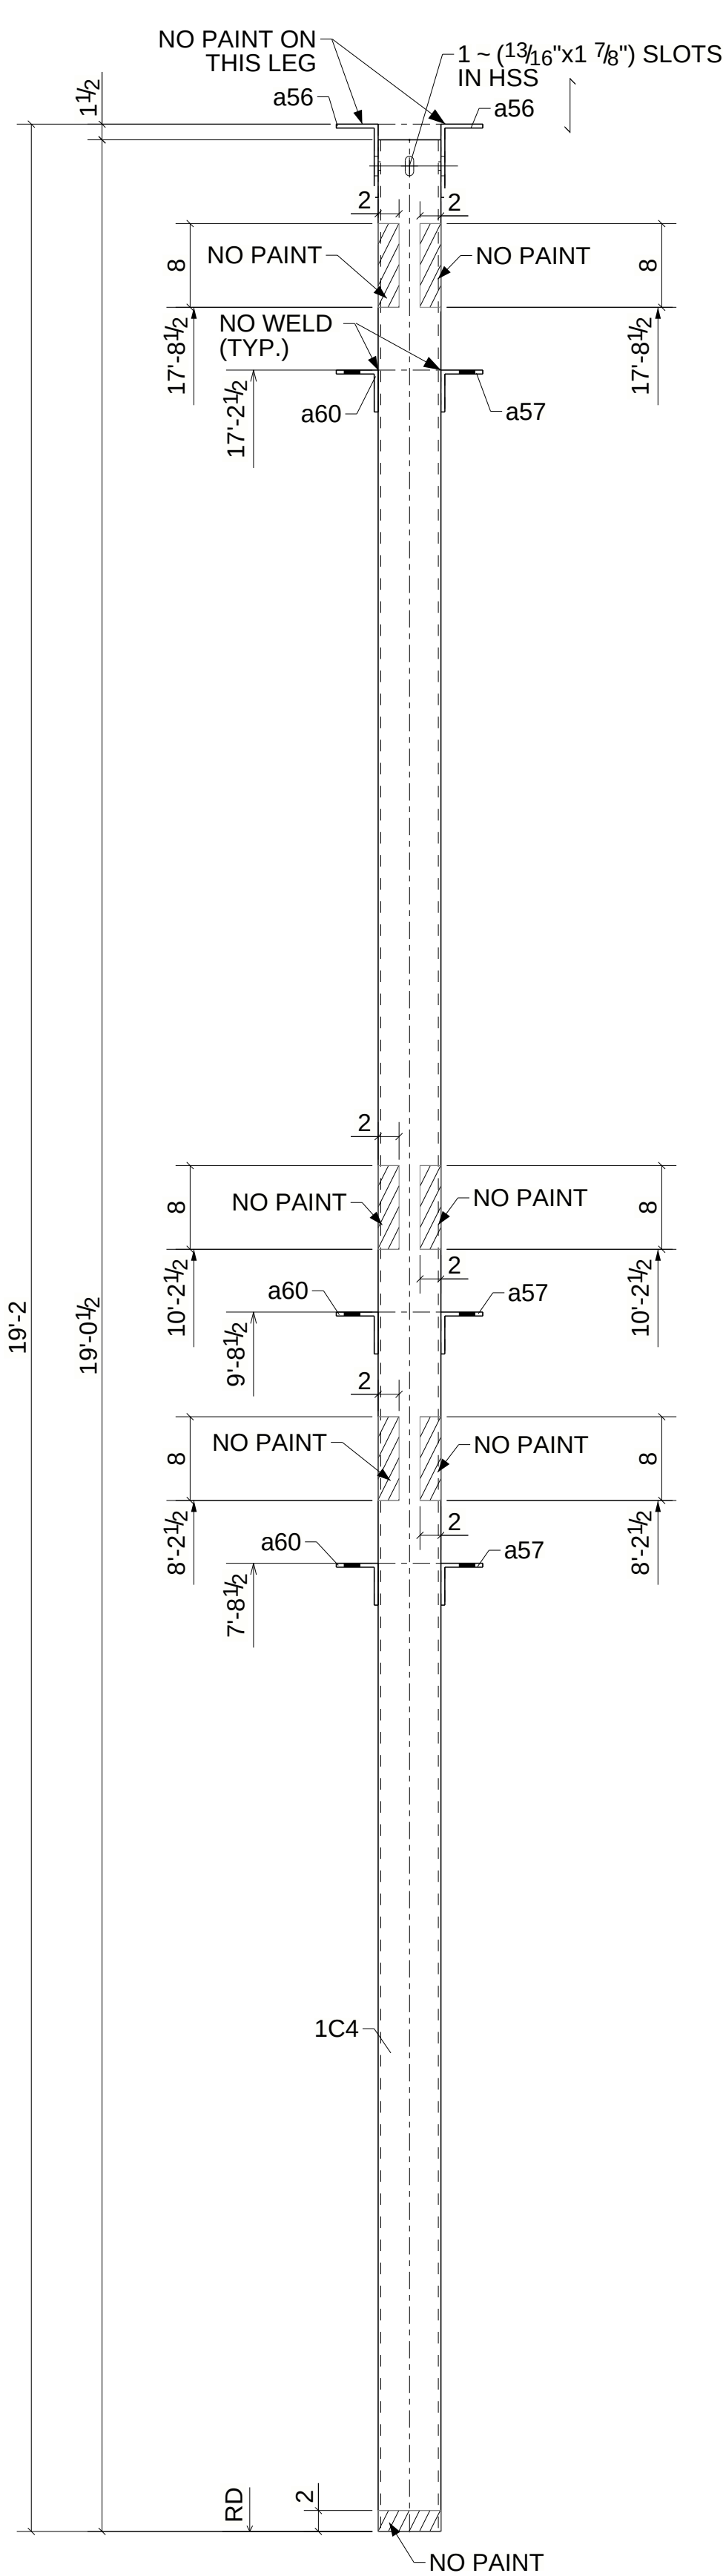

20 HIGH STREET
PLAINSVILLE, MA 02762
PHONE (508) 381-0429
www.teambes.com

0	04/11/2025	For Fabrication	PROJECT NAME	GSC JUNIPER RBP PHASE-II			
A	10/16/2024	For Approval	LOCATION	PARKWAY EVERETT, MA			
REV.	DATE	DESCRIPTION	CONTRACTOR	BUILDING ENVELOPE SYSTEMS			
MATERIAL A36 UNO			DWG TITLE	COLUMN			
HOLES 13/16Ø UNO			DRAWN BY	ABJ	CHECKED BY	HSR	DATE DRAWN 10/15/2024
WELDS E70XX			DATE DRAWN	10/15/2024	PLOT DATE	10/15/2024	DGSTS No. ---
SURFACE PREP. SSPC SP2			CONTRACT No.	24050	DWG No.	1C4	REV. 0
PAINT NOTE: SW SHOP PRIMER							

ONE - COLUMN - 1C4