


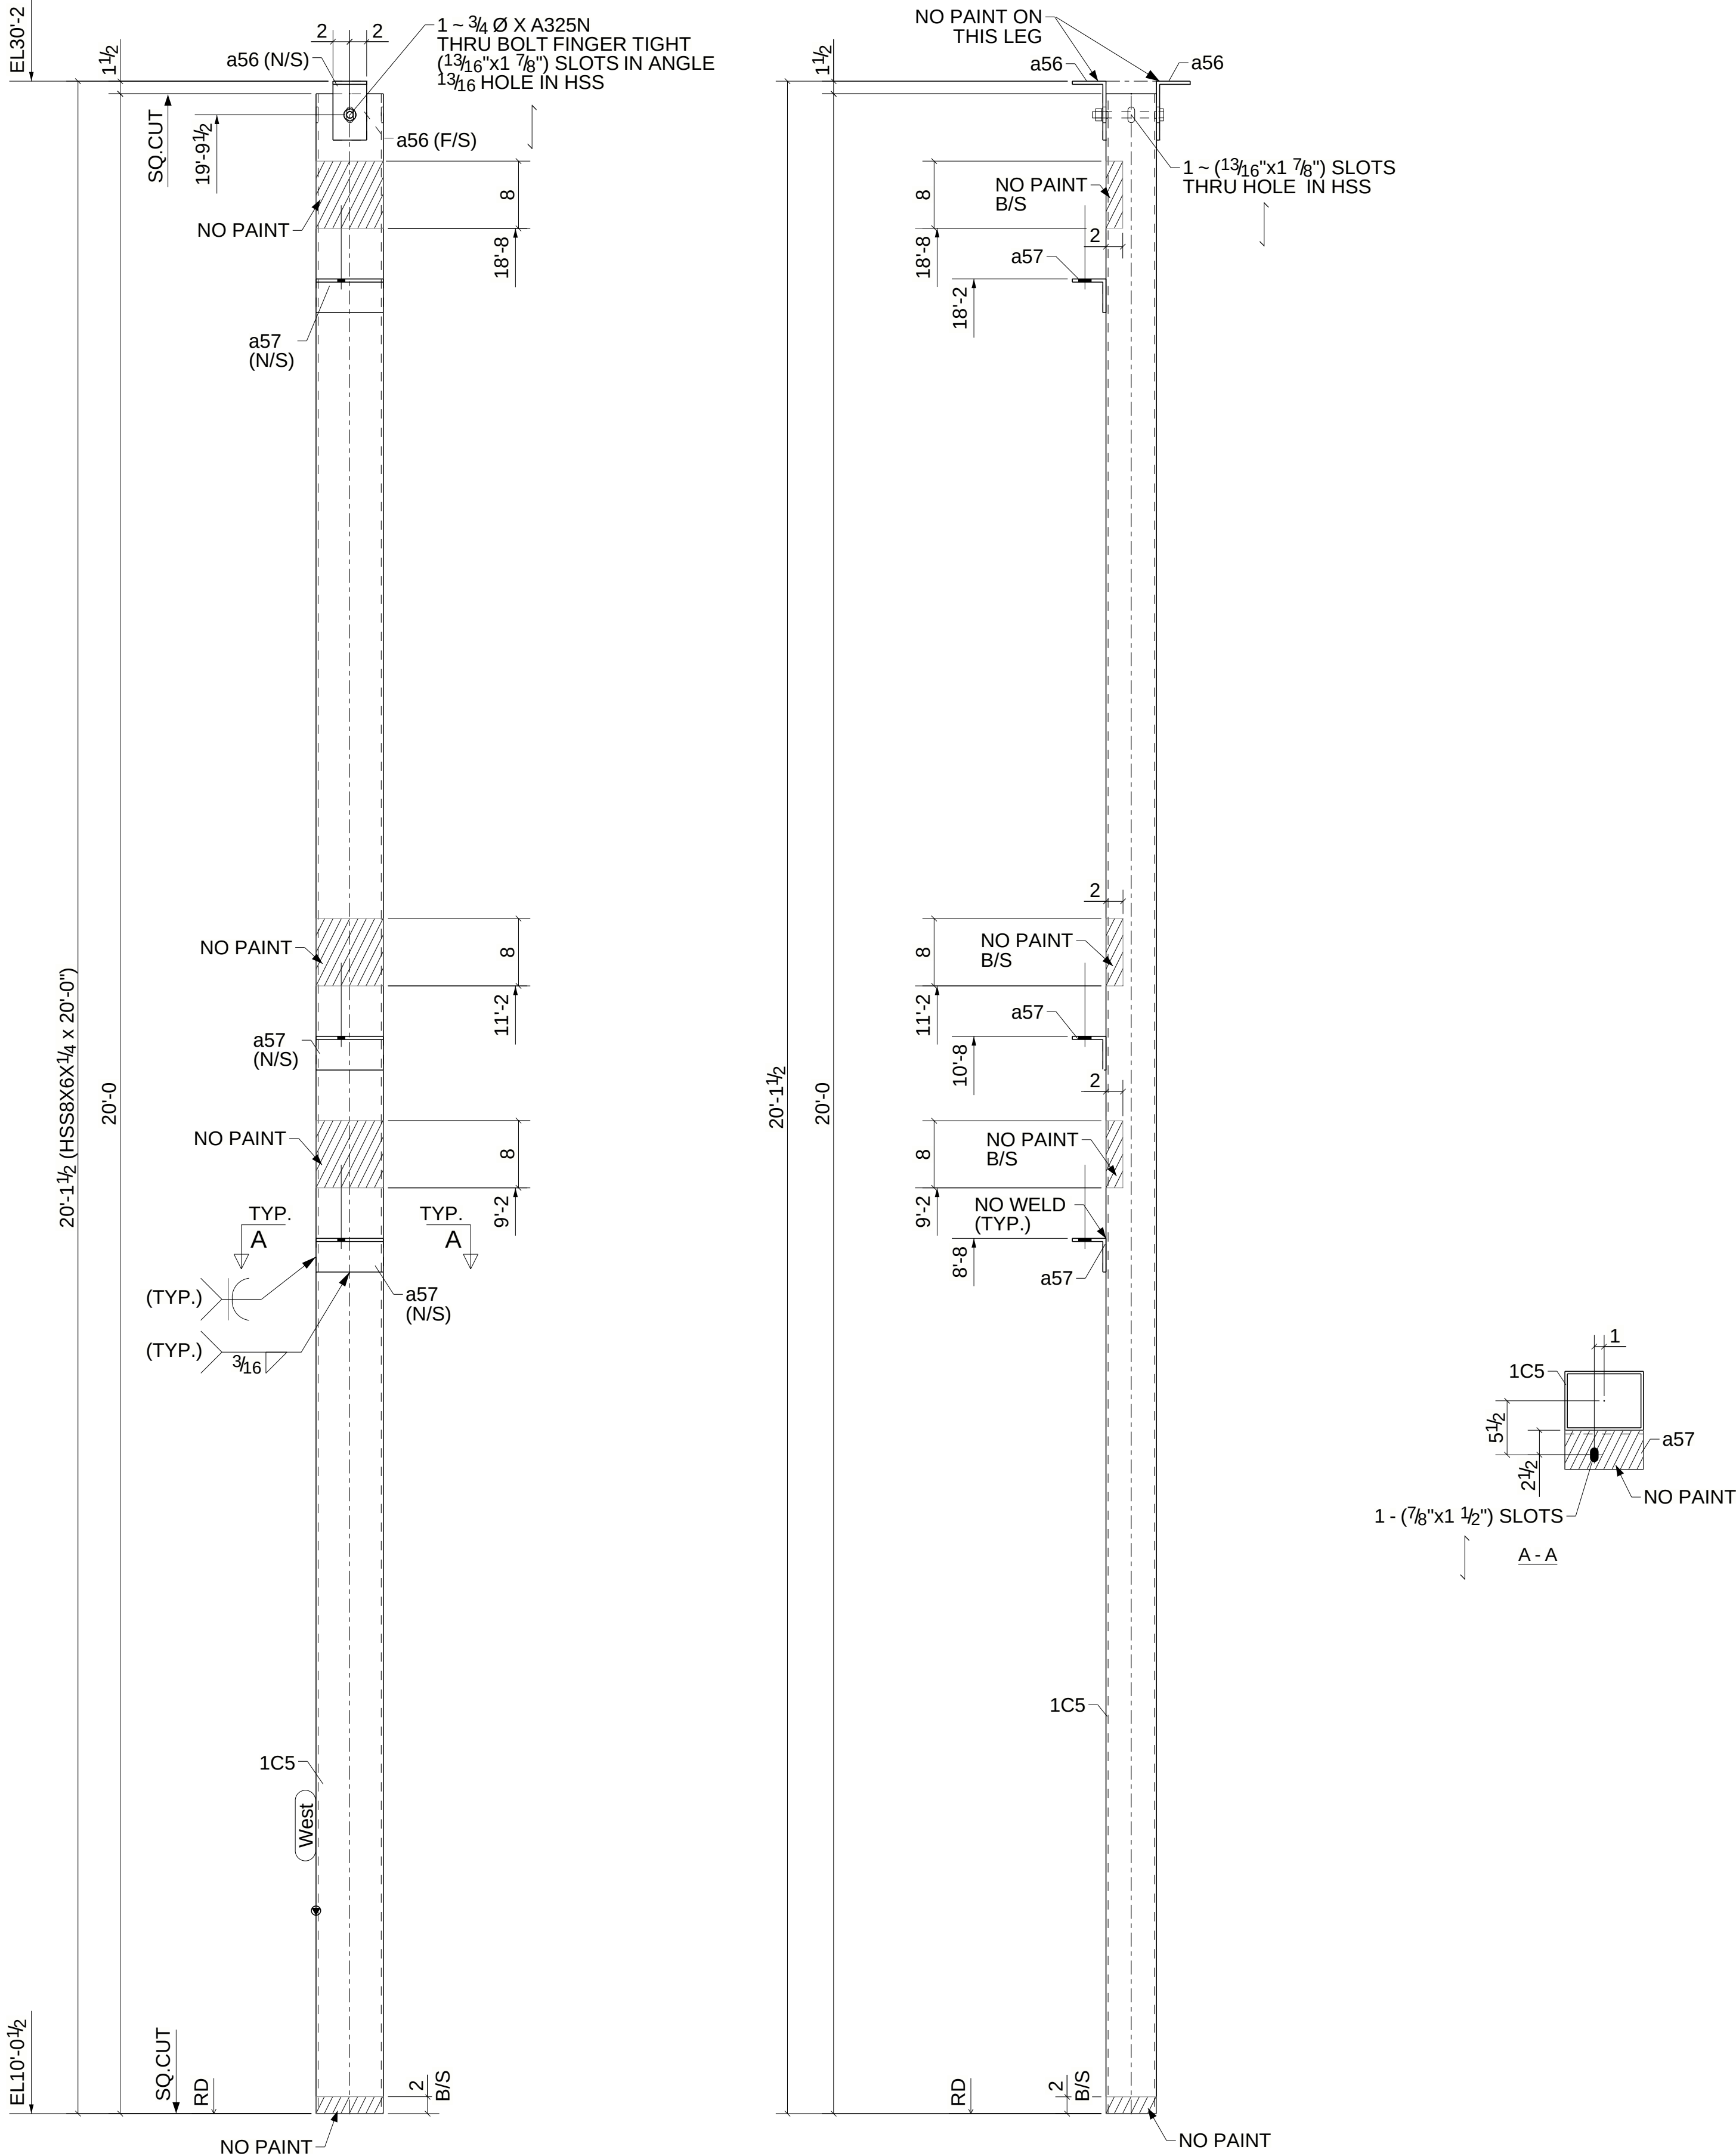

ONE - COLUMN - 1C5

BILL OF MATERIAL							
MARK	TOTAL QTY	SHAPE	LENGTH	TOTAL WEIGHT	REMARKS	ADV MILL #	STEEL GRADE
1C5	1	HSS8X6X1/4	20'-0"	420	SQ-2		A500-GR B
a56	2	L7X4X3/8	0'-4"	9			A36
a57	3	L4X4X3/8	0'-8"	19			A36
	1	3/4"Ø A325N BOLT	0'-8"	1	Workshop		

0		04/11/2025		For Fabrication		PROJECT NAME GSC JUNIPER RBP PHASE-II											
A		10/15/2024		For Approval													
REV.		DATE	DESCRIPTION														
MATERIAL A36 UNO						LOCATION PARKWAY EVERETT, MA											
HOLES 13/16Ø UNO						CONTRACTOR BUILDING ENVELOPE SYSTEMS											
WELDS E70XX						DWG TITLE COLUMN											
SURFACE PREP. SSPC SP2						DRAWN BY ABJ		CHECKED BY HSR		DATE DRAWN 10/15/2024		PLOT DATE 10/15/2024		DGSTS No. --			
PAINT NOTE: SW SHOP PRIMER						CONTRACT No. 24050						DWG No. 1C5		REV.		0	

Building Envelope Systems



20 HIGH STREET
PLAINSVILLE, MA 02762
PHONE (508) 381-0429
www.teambes.com