
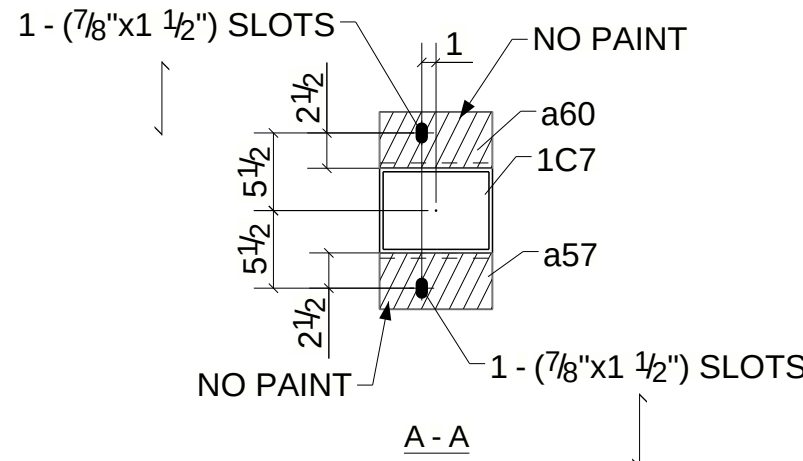
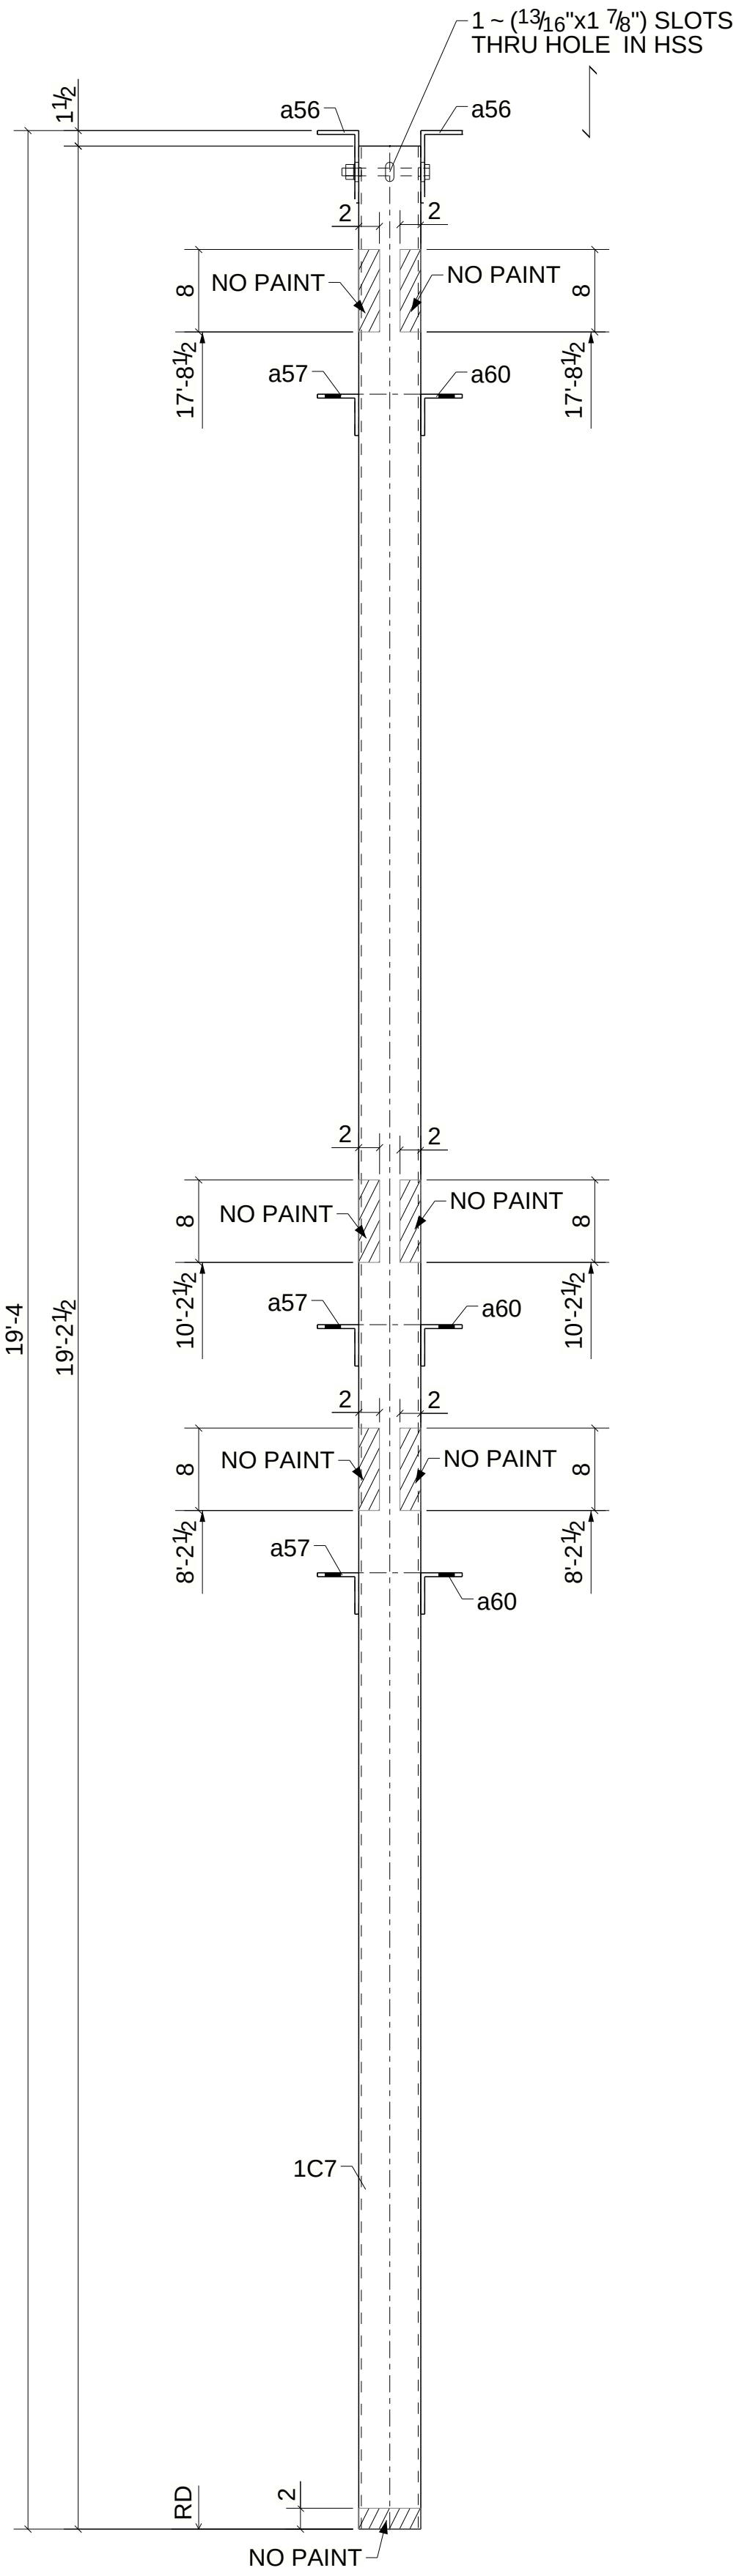
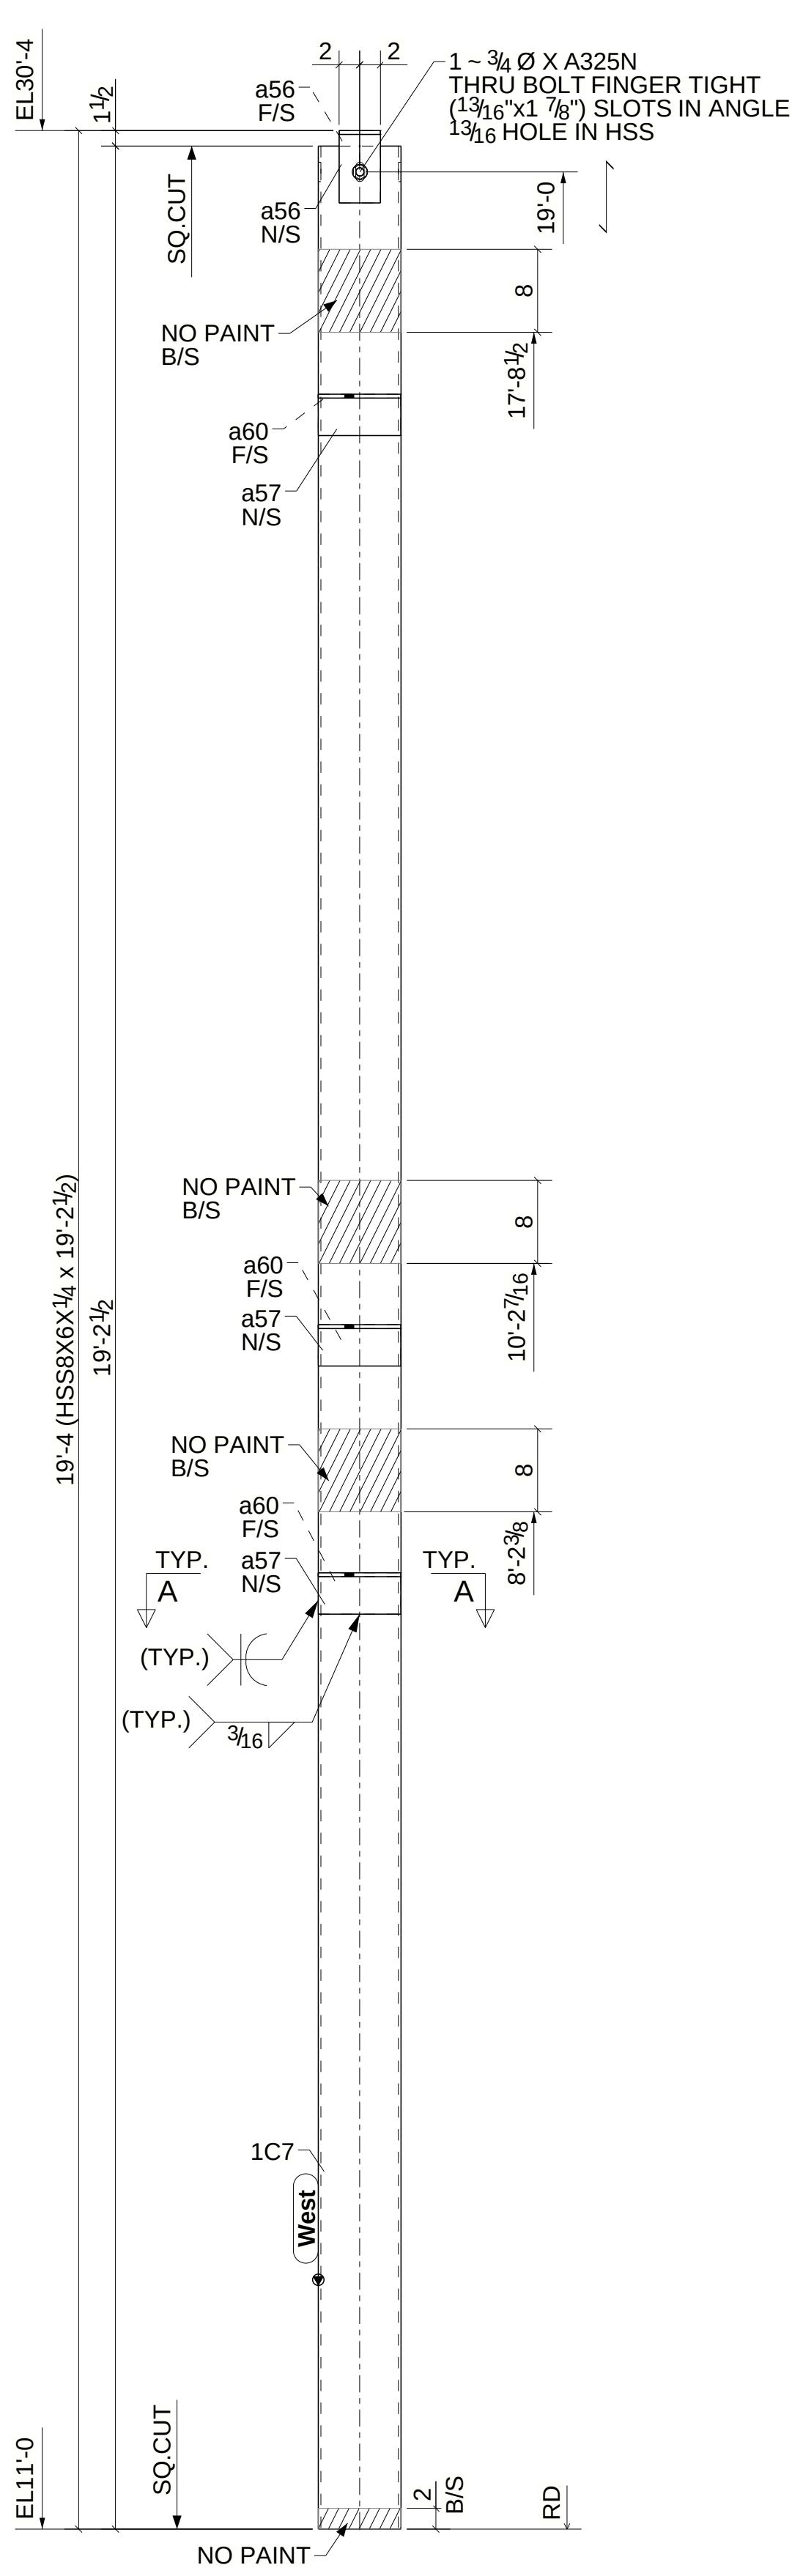


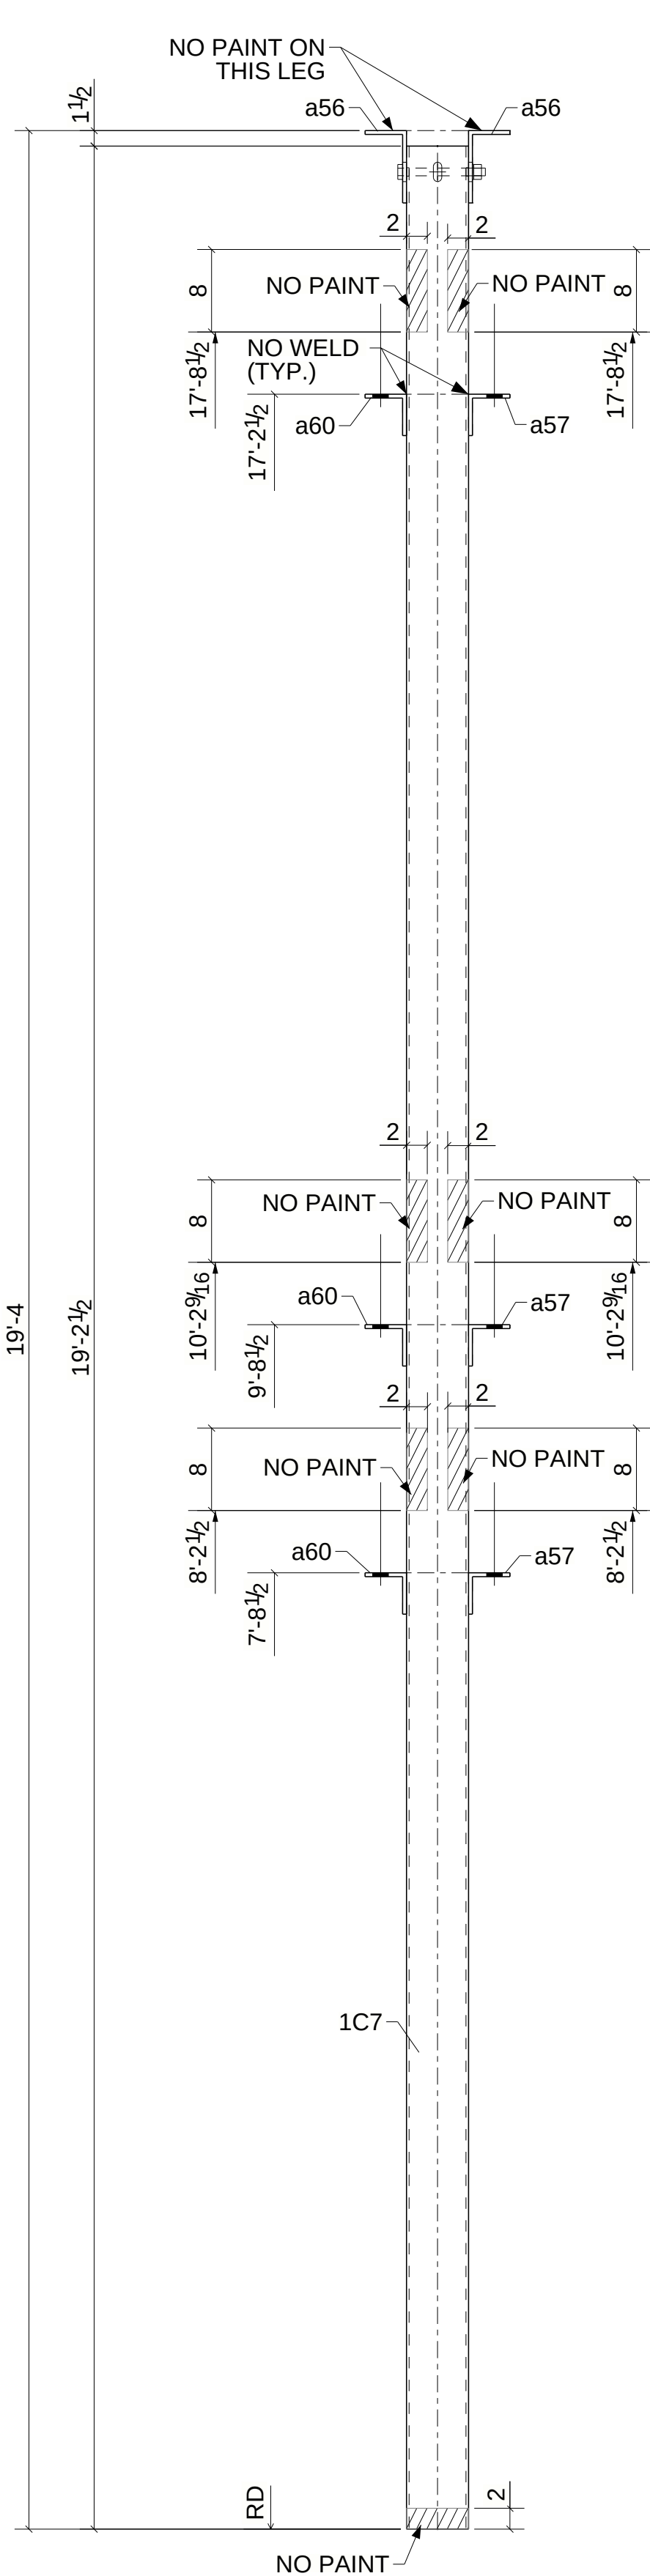

ONE - COLUMN - 1C7

BILL OF MATERIAL

MARK	TOTAL QTY	SHAPE	LENGTH	TOTAL WEIGHT	REMARKS	ADV MILL #	STEEL GRADE
1C7	1	HSS8X6X1/4	19'-2 1/2"	403	SQ-2		A500-GR B
a56	2	L7X4X3/8	0'-4"	9			A36
a57	3	L4X4X3/8	0'-8"	19			A36
a60	3	L4X4X3/8	0'-8"	19			A36
	1	3/4"Ø A325N BOLT	0'-8"	1	Workshop		

GRID LOCATION	BOTTOM ELEVATION
<103/XX-YY	11'-0"



20 HIGH STREET
PLAINSVILLE, MA 02762
PHONE (508) 381-0429
www.teambes.com

0	04/11/2025	For Fabrication	PROJECT NAME	GSC JUNIPER RBP PHASE-II
A	10/16/2024	For Approval	LOCATION	PARKWAY EVERETT, MA
REV.	DATE	DESCRIPTION	CONTRACTOR	BUILDING ENVELOPE SYSTEMS
MATERIAL	A36 UNO		DWG TITLE	COLUMN
HOLES	13/16Ø UNO		DRAWN BY	ABJ
WELDS	E70XX		CHECKED BY	HSR
SURFACE PREP.	SSPC SP2		DATE DRAWN	10/15/2024
PAINT NOTE:	SW SHOP PRIMER		PLOT DATE	10/15/2024
			DGSTS No.	--
			REV.	0
			CONTRACT No.	24050
			DWG No.	1C7