

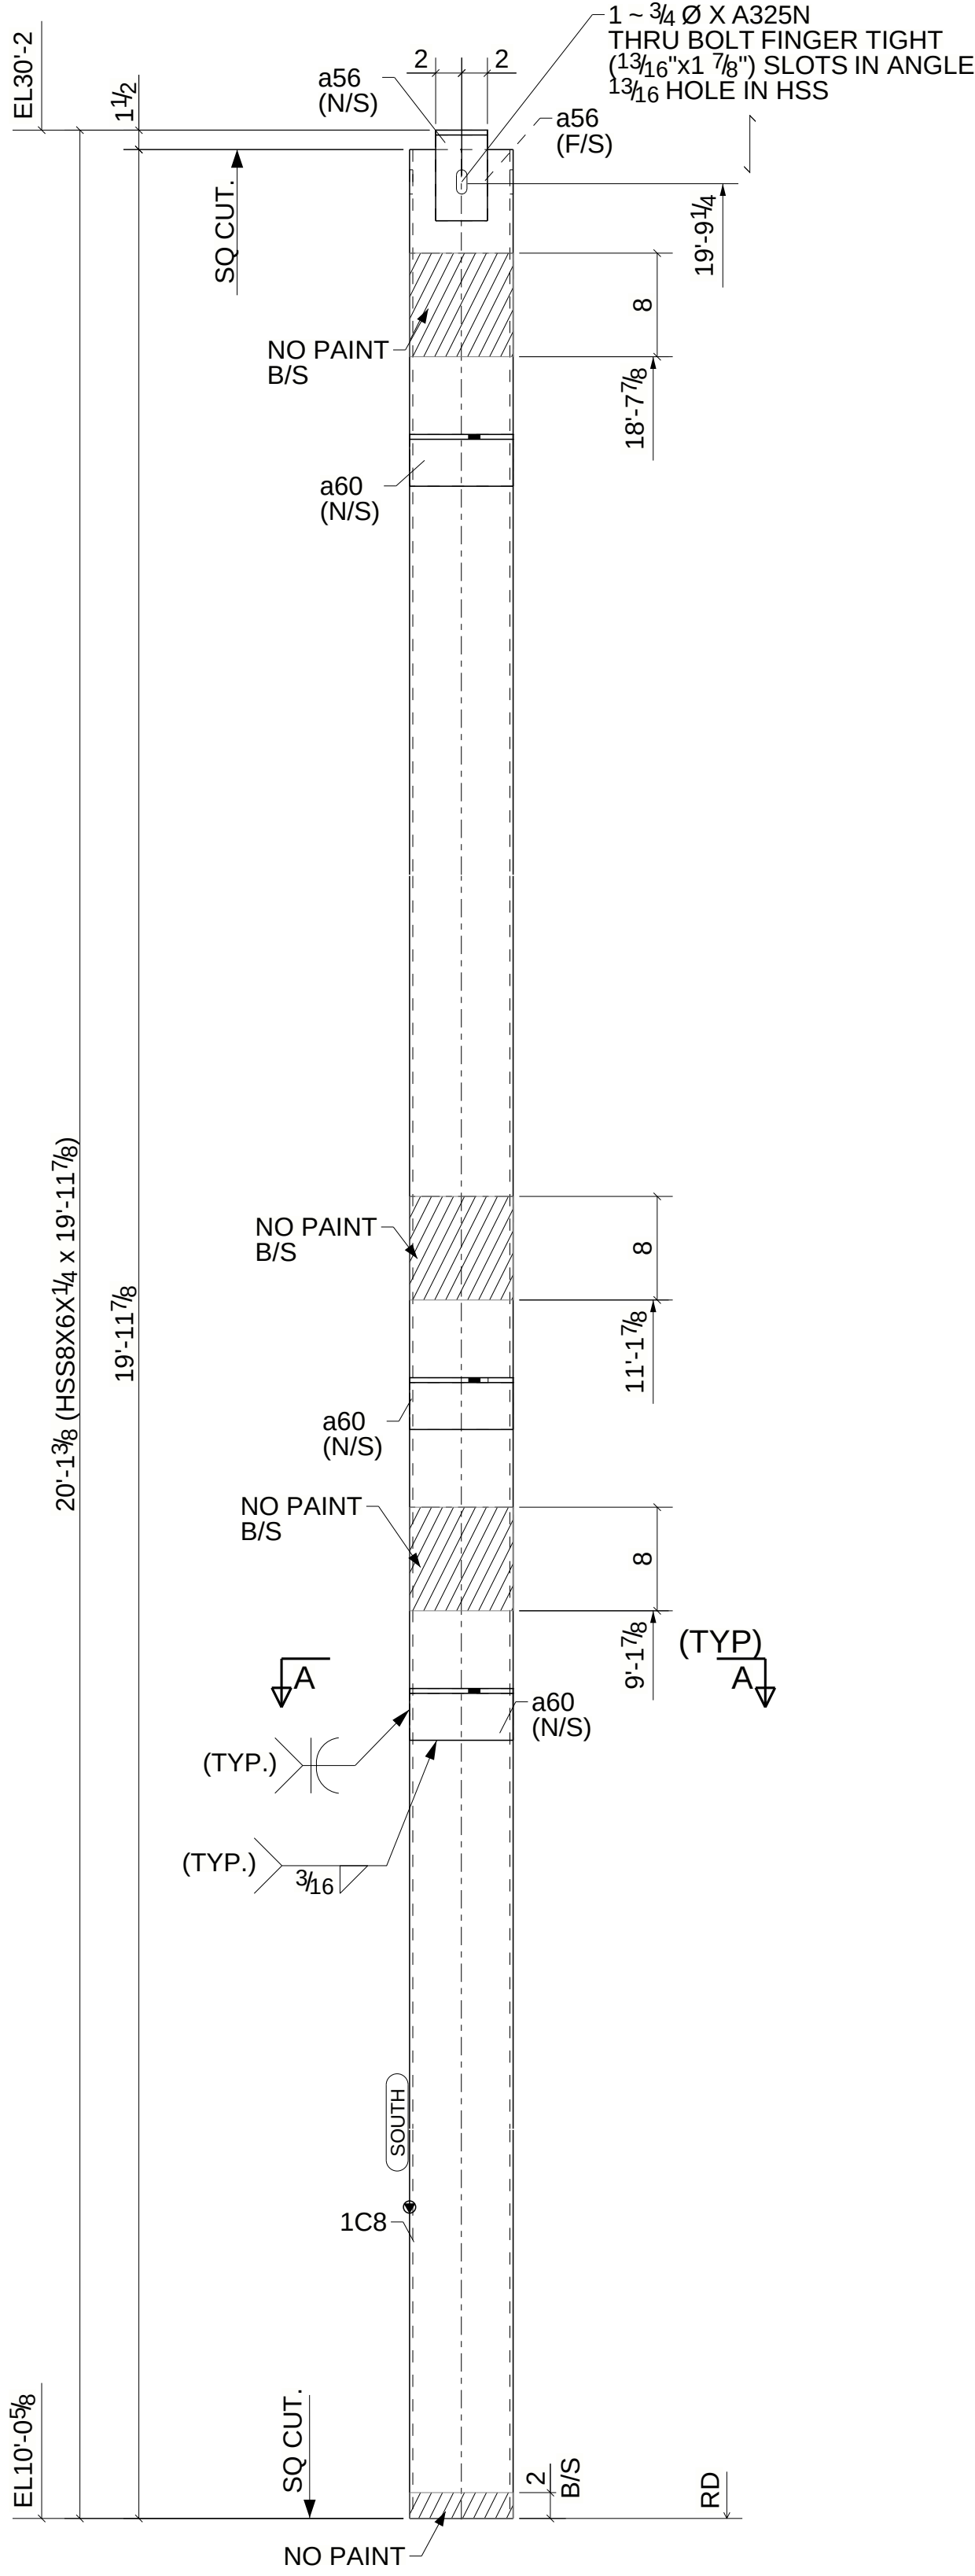


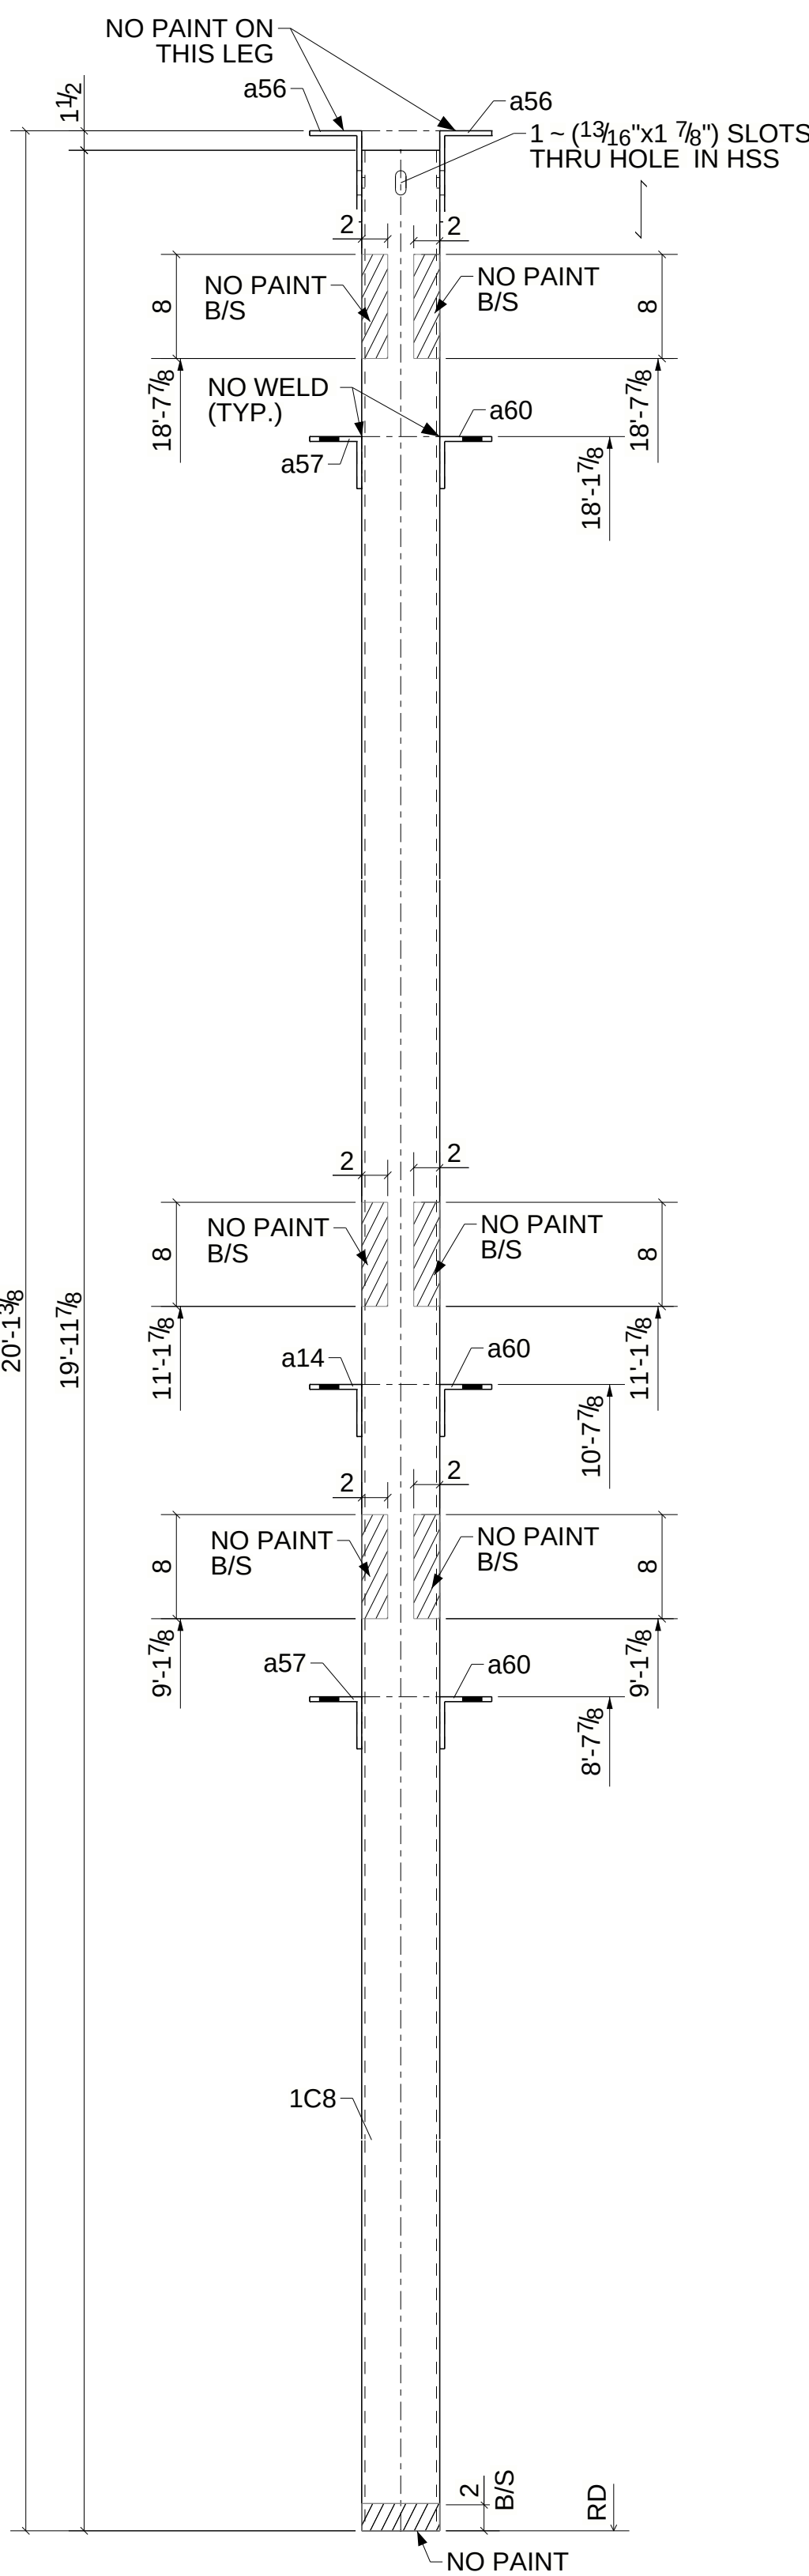

ONE - COLUMN - 1C8

BILL OF MATERIAL

MARK	TOTAL QTY	SHAPE	LENGTH	TOTAL WEIGHT	REMARKS	ADV MILL #	STEEL GRADE
1C8	1	HSS8X6X1/4	19'-11 7/8"	420	SQ-2		A500-GR B
a14	1	L4X4X3/8	0'-8"	6			A36
a56	2	L7X4X3/8	0'-4"	9			A36
a57	2	L4X4X3/8	0'-8"	13			A36
a60	3	L4X4X3/8	0'-8"	19			A36
	1	3/4"Ø A325N BOLT	0'-8"	1	Workshop		

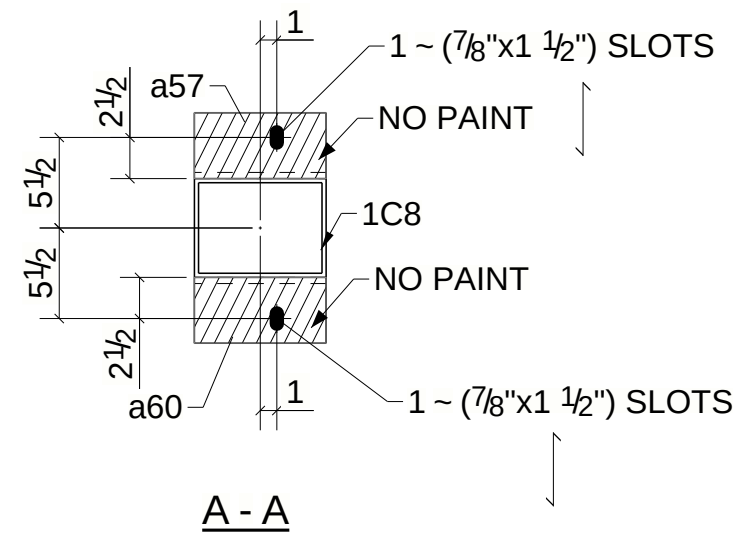

GRID LOCATION	BOTTOM ELEVATION
102.5-10***	10'-0"5/8



20 HIGH STREET
PLAINSVILLE, MA 02762
PHONE (508) 381-0429
www.teambes.com

0	04/11/2025	For Fabrication
A	10/16/2024	For Approval
REV.	DATE	DESCRIPTION
MATERIAL	A36 UNO	
HOLES	13/16Ø UNO	
WELDS	E70XX	
SURFACE PREP.	SSPC SP2	
PAINT NOTE:	SW SHOP PRIMER	

PROJECT NAME	GSC JUNIPER RBP PHASE-II				
LOCATION	PARKWAY EVERETT, MA				
CONTRACTOR	BUILDING ENVELOPE SYSTEMS				
DWG TITLE	COLUMN				
DRAWN BY	ABJ	CHECKED BY	HSR	DATE DRAWN	10/15/2024
PLLOT DATE	10/15/2024	DGSTS No.	---	REV.	0
CONTRACT No.	24050		DWG No.	1C8	