

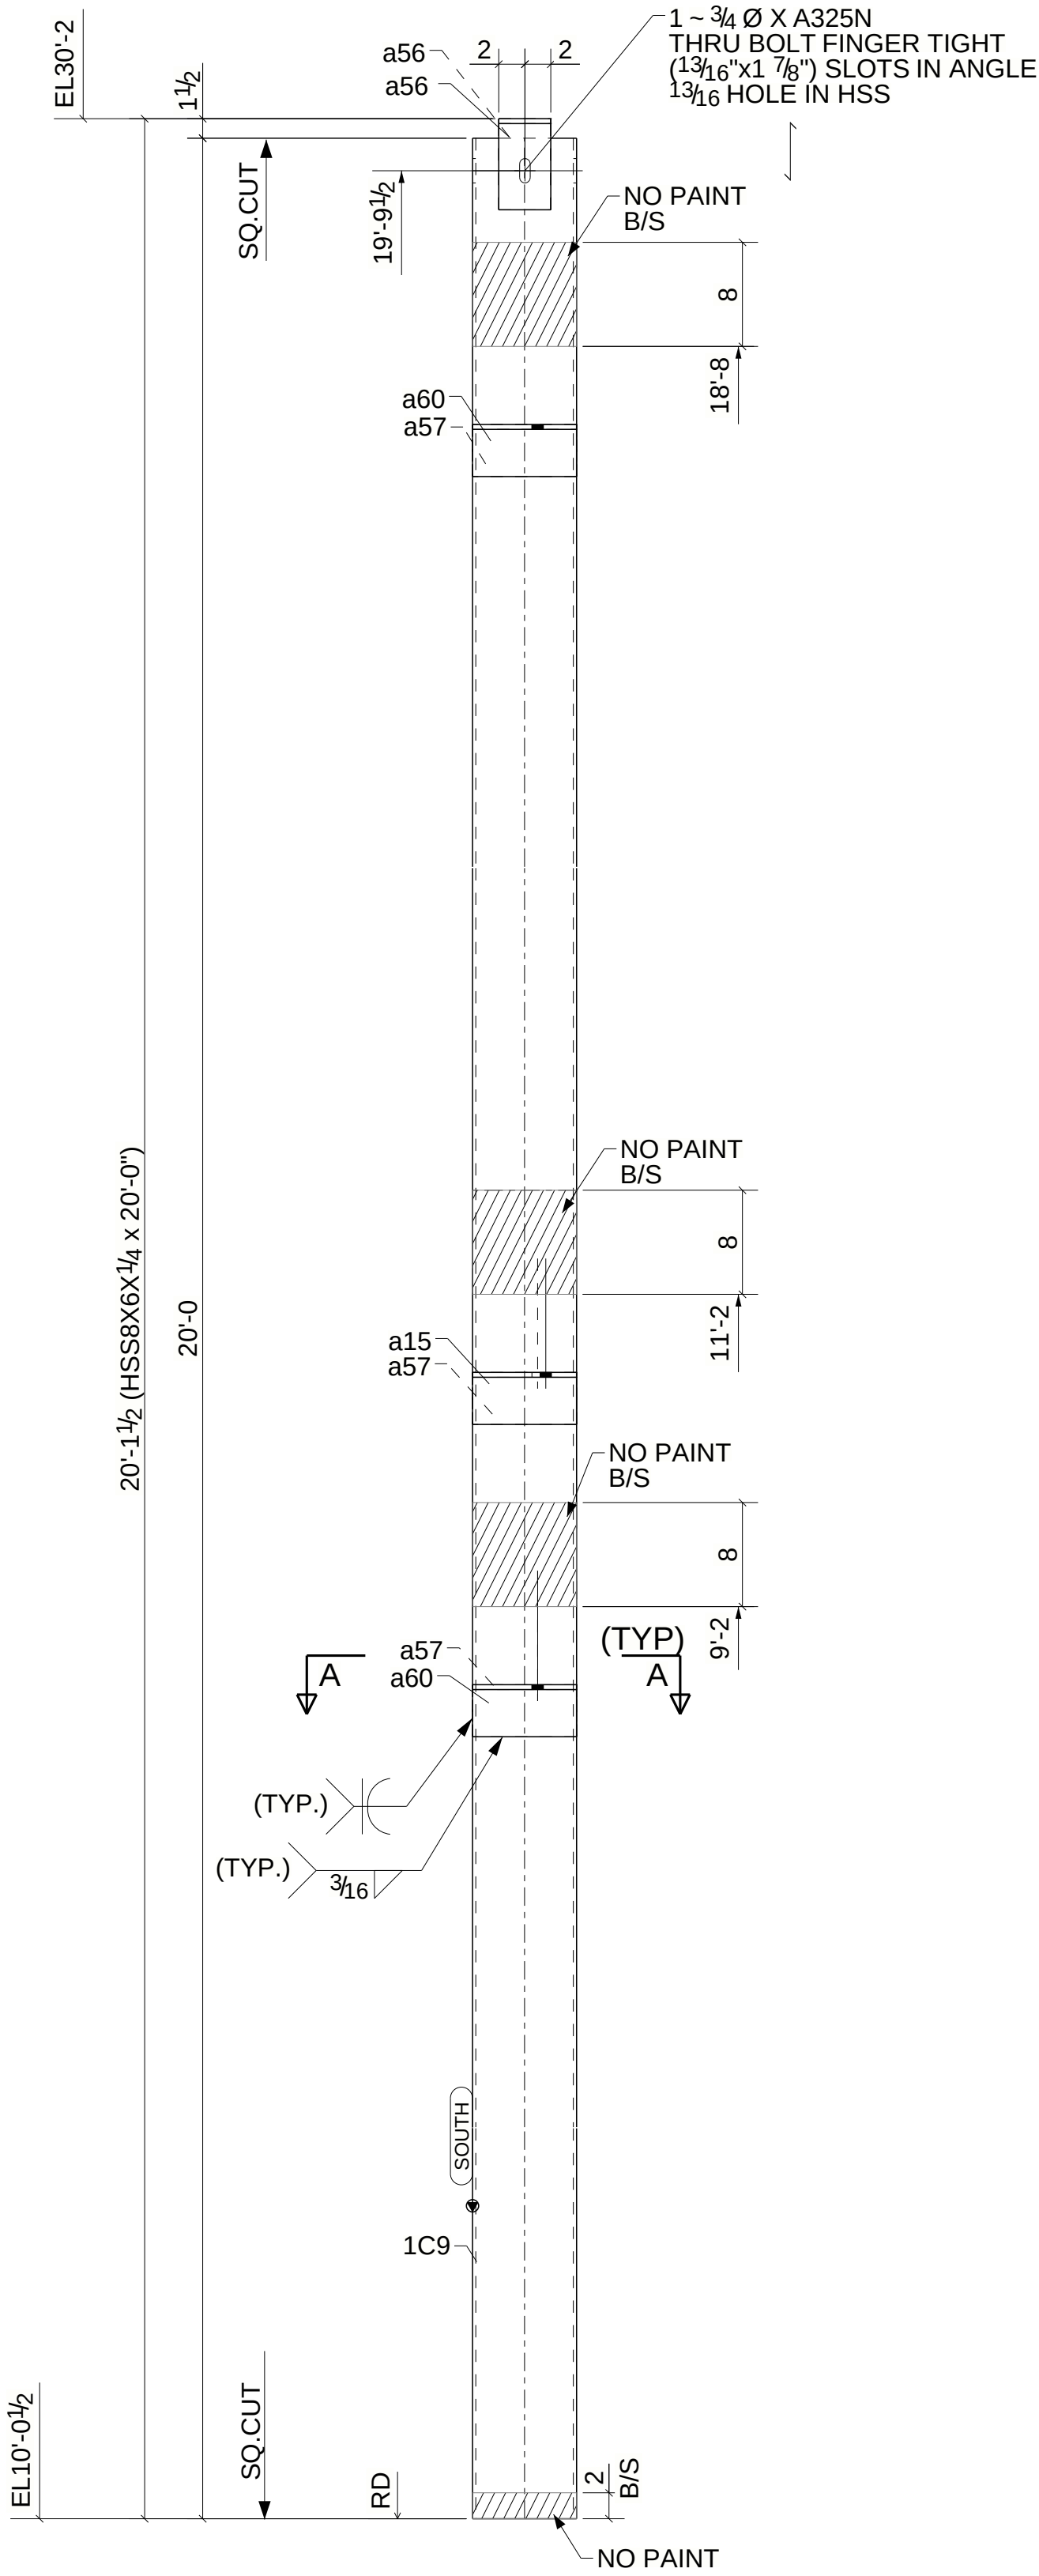


BILL OF MATERIAL							
MARK	TOTAL QTY	SHAPE	LENGTH	TOTAL WEIGHT	REMARKS	ADV MILL #	STEEL GRADE
1C9	1	HSS8X6X1/4	20'-0"	420	SQ-2		A500-GR B
a15	1	L4X4X3/8	0'-8"	6			A36
a56	2	L7X4X3/8	0'-4"	9			A36
a57	3	L4X4X3/8	0'-8"	19			A36
a60	2	L4X4X3/8	0'-8"	13			A36
	1	3/4"Ø A325N BOLT	0'-8"	1	Workshop		

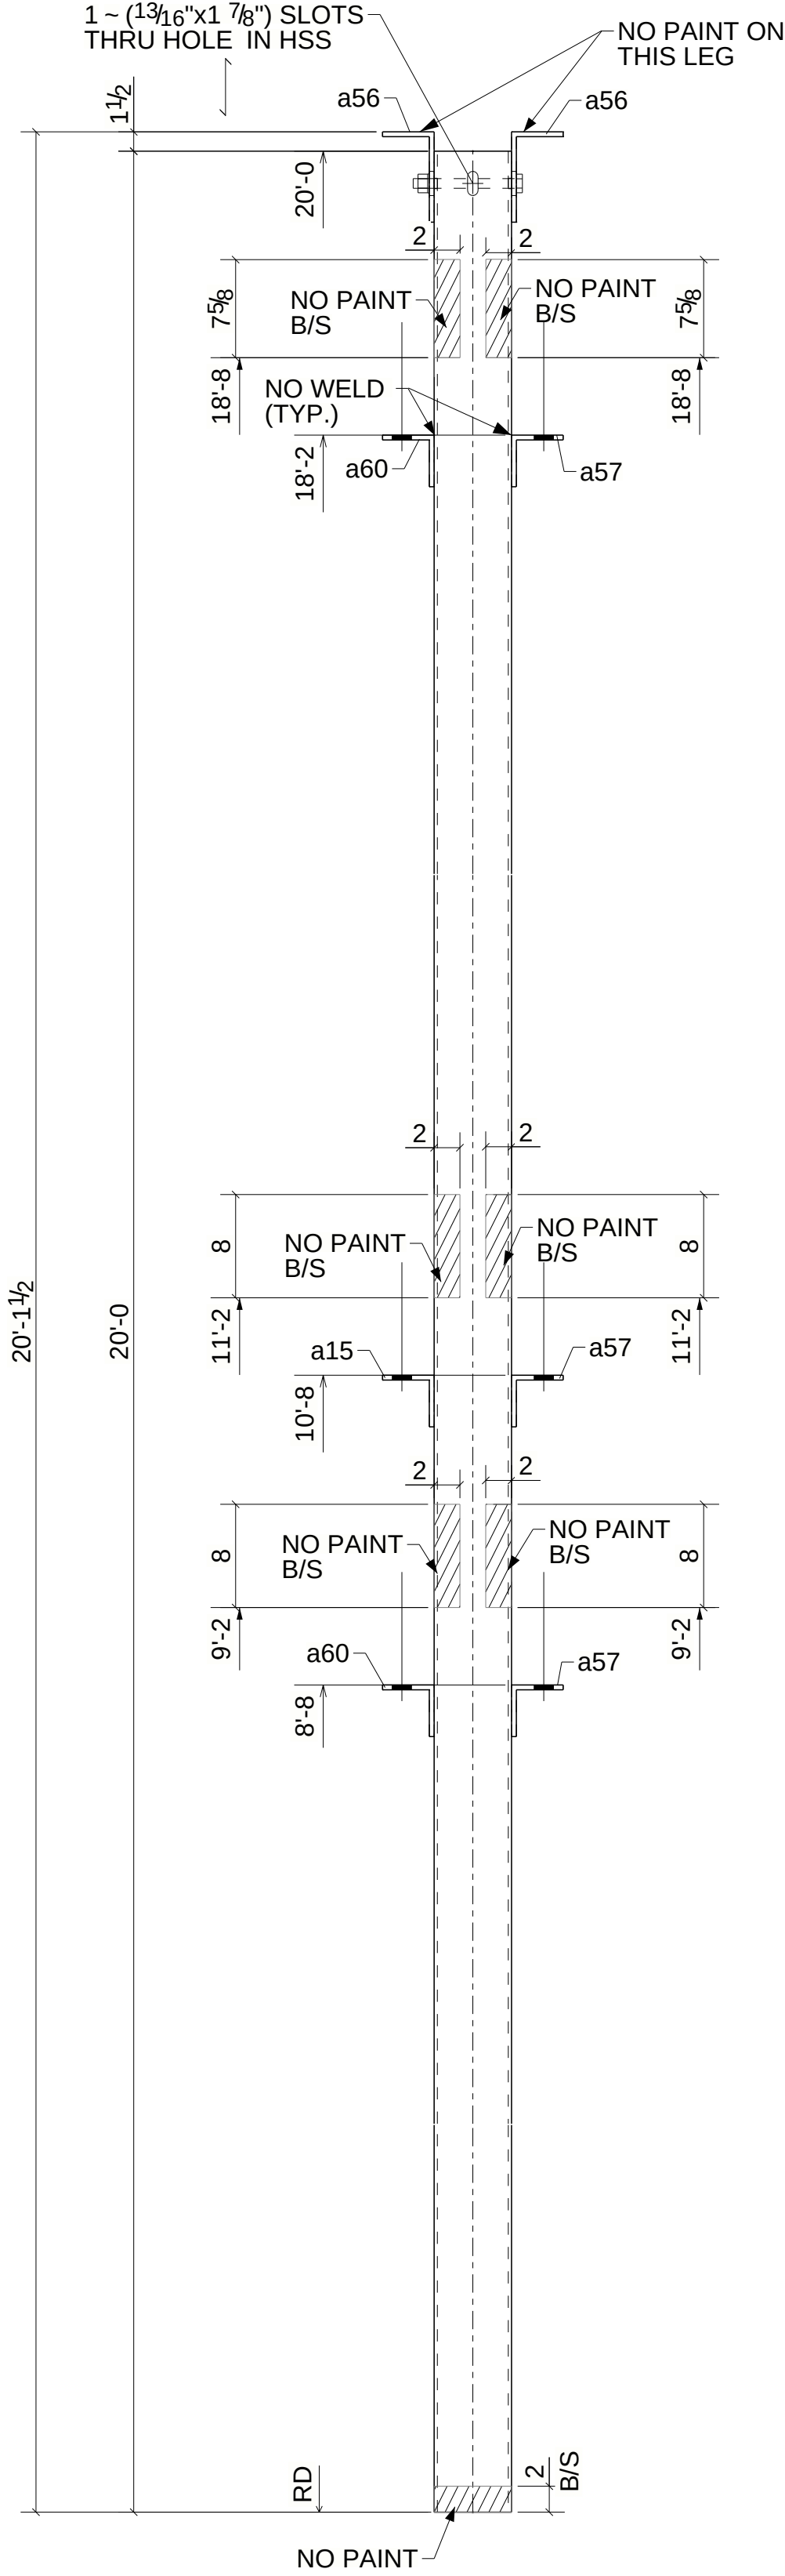

ONE - COLUMN - 1C9

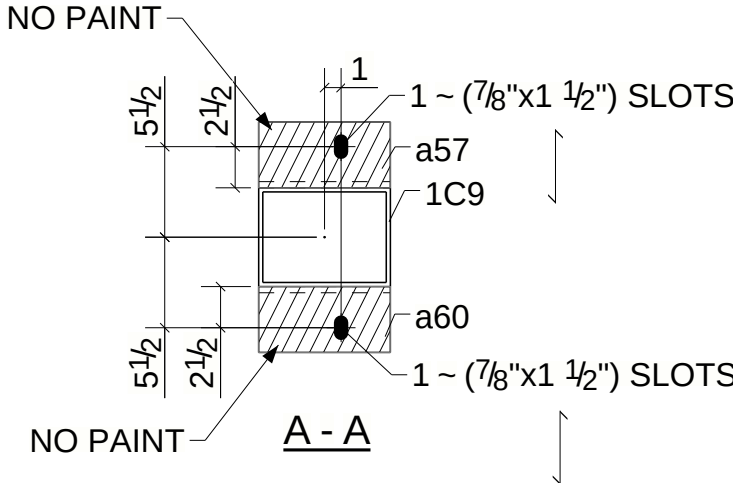

0	04/11/2025	For Fabrication
A	10/16/2024	For Approval
REV.	DATE	DESCRIPTION
MATERIAL A36 UNO		
HOLES 13/16Ø UNO		
WELDS E70XX		
SURFACE PREP. SSPC SP2		
PAINT NOTE: SW SHOP PRIMER		

GRID LOCATION 102.5/ZZ.5		BOTTOM ELEVATION 10'-0"1/2
--	--	--

Building Envelope Systems



20 HIGH STREET

PLAINSVILLE, MA 02762

PHONE (508) 381-0429

www.teambes.com

PROJECT NAME GSC JUNIPER RBP PHASE-II			
LOCATION PARKWAY EVERETT, MA			
CONTRACTOR BUILDING ENVELOPE SYSTEMS			
DWG TITLE COLUMN			
DRAWN BY ABJ	CHECKED BY HSR	DATE DRAWN 10/15/2024	PLOT DATE 10/15/2024
CONTRACT NO. 24050		DWG NO. 1C9	DGSTS No. -- REV. 0