
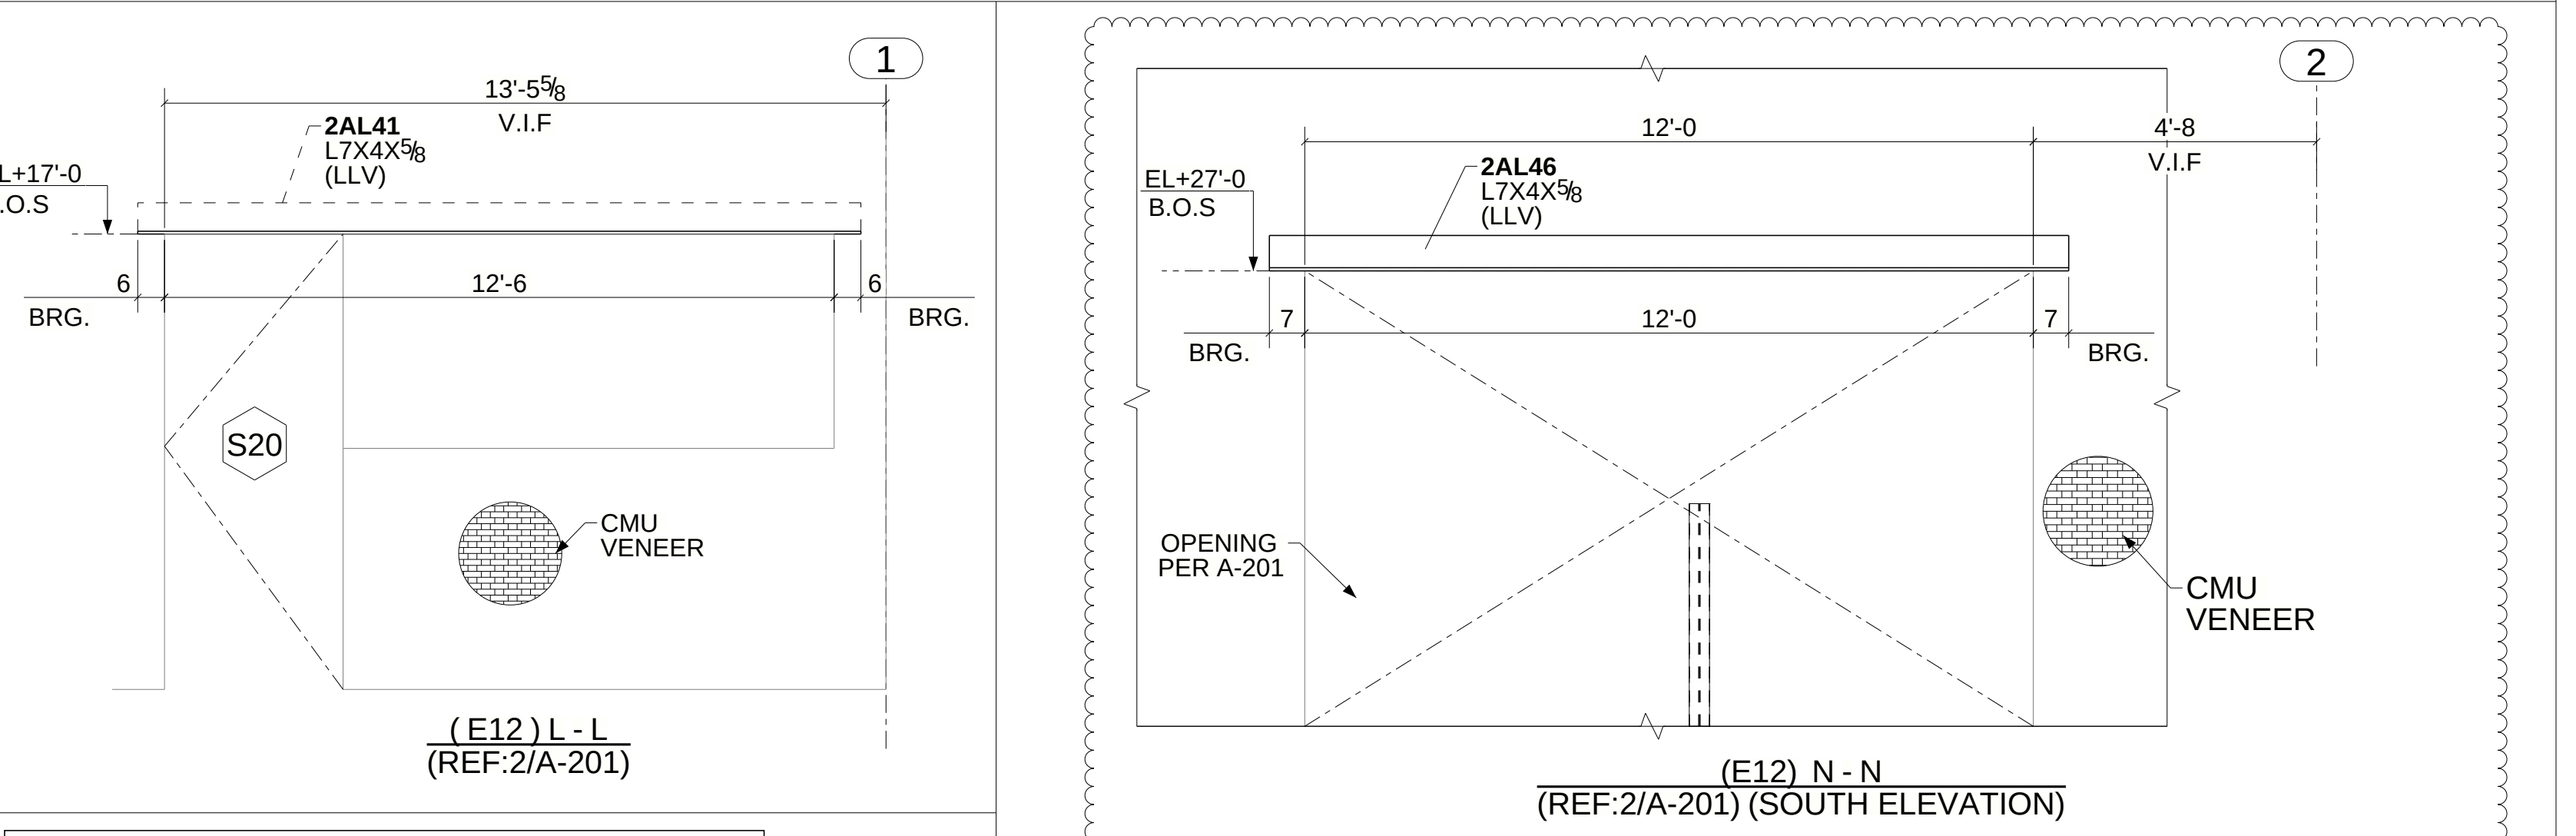
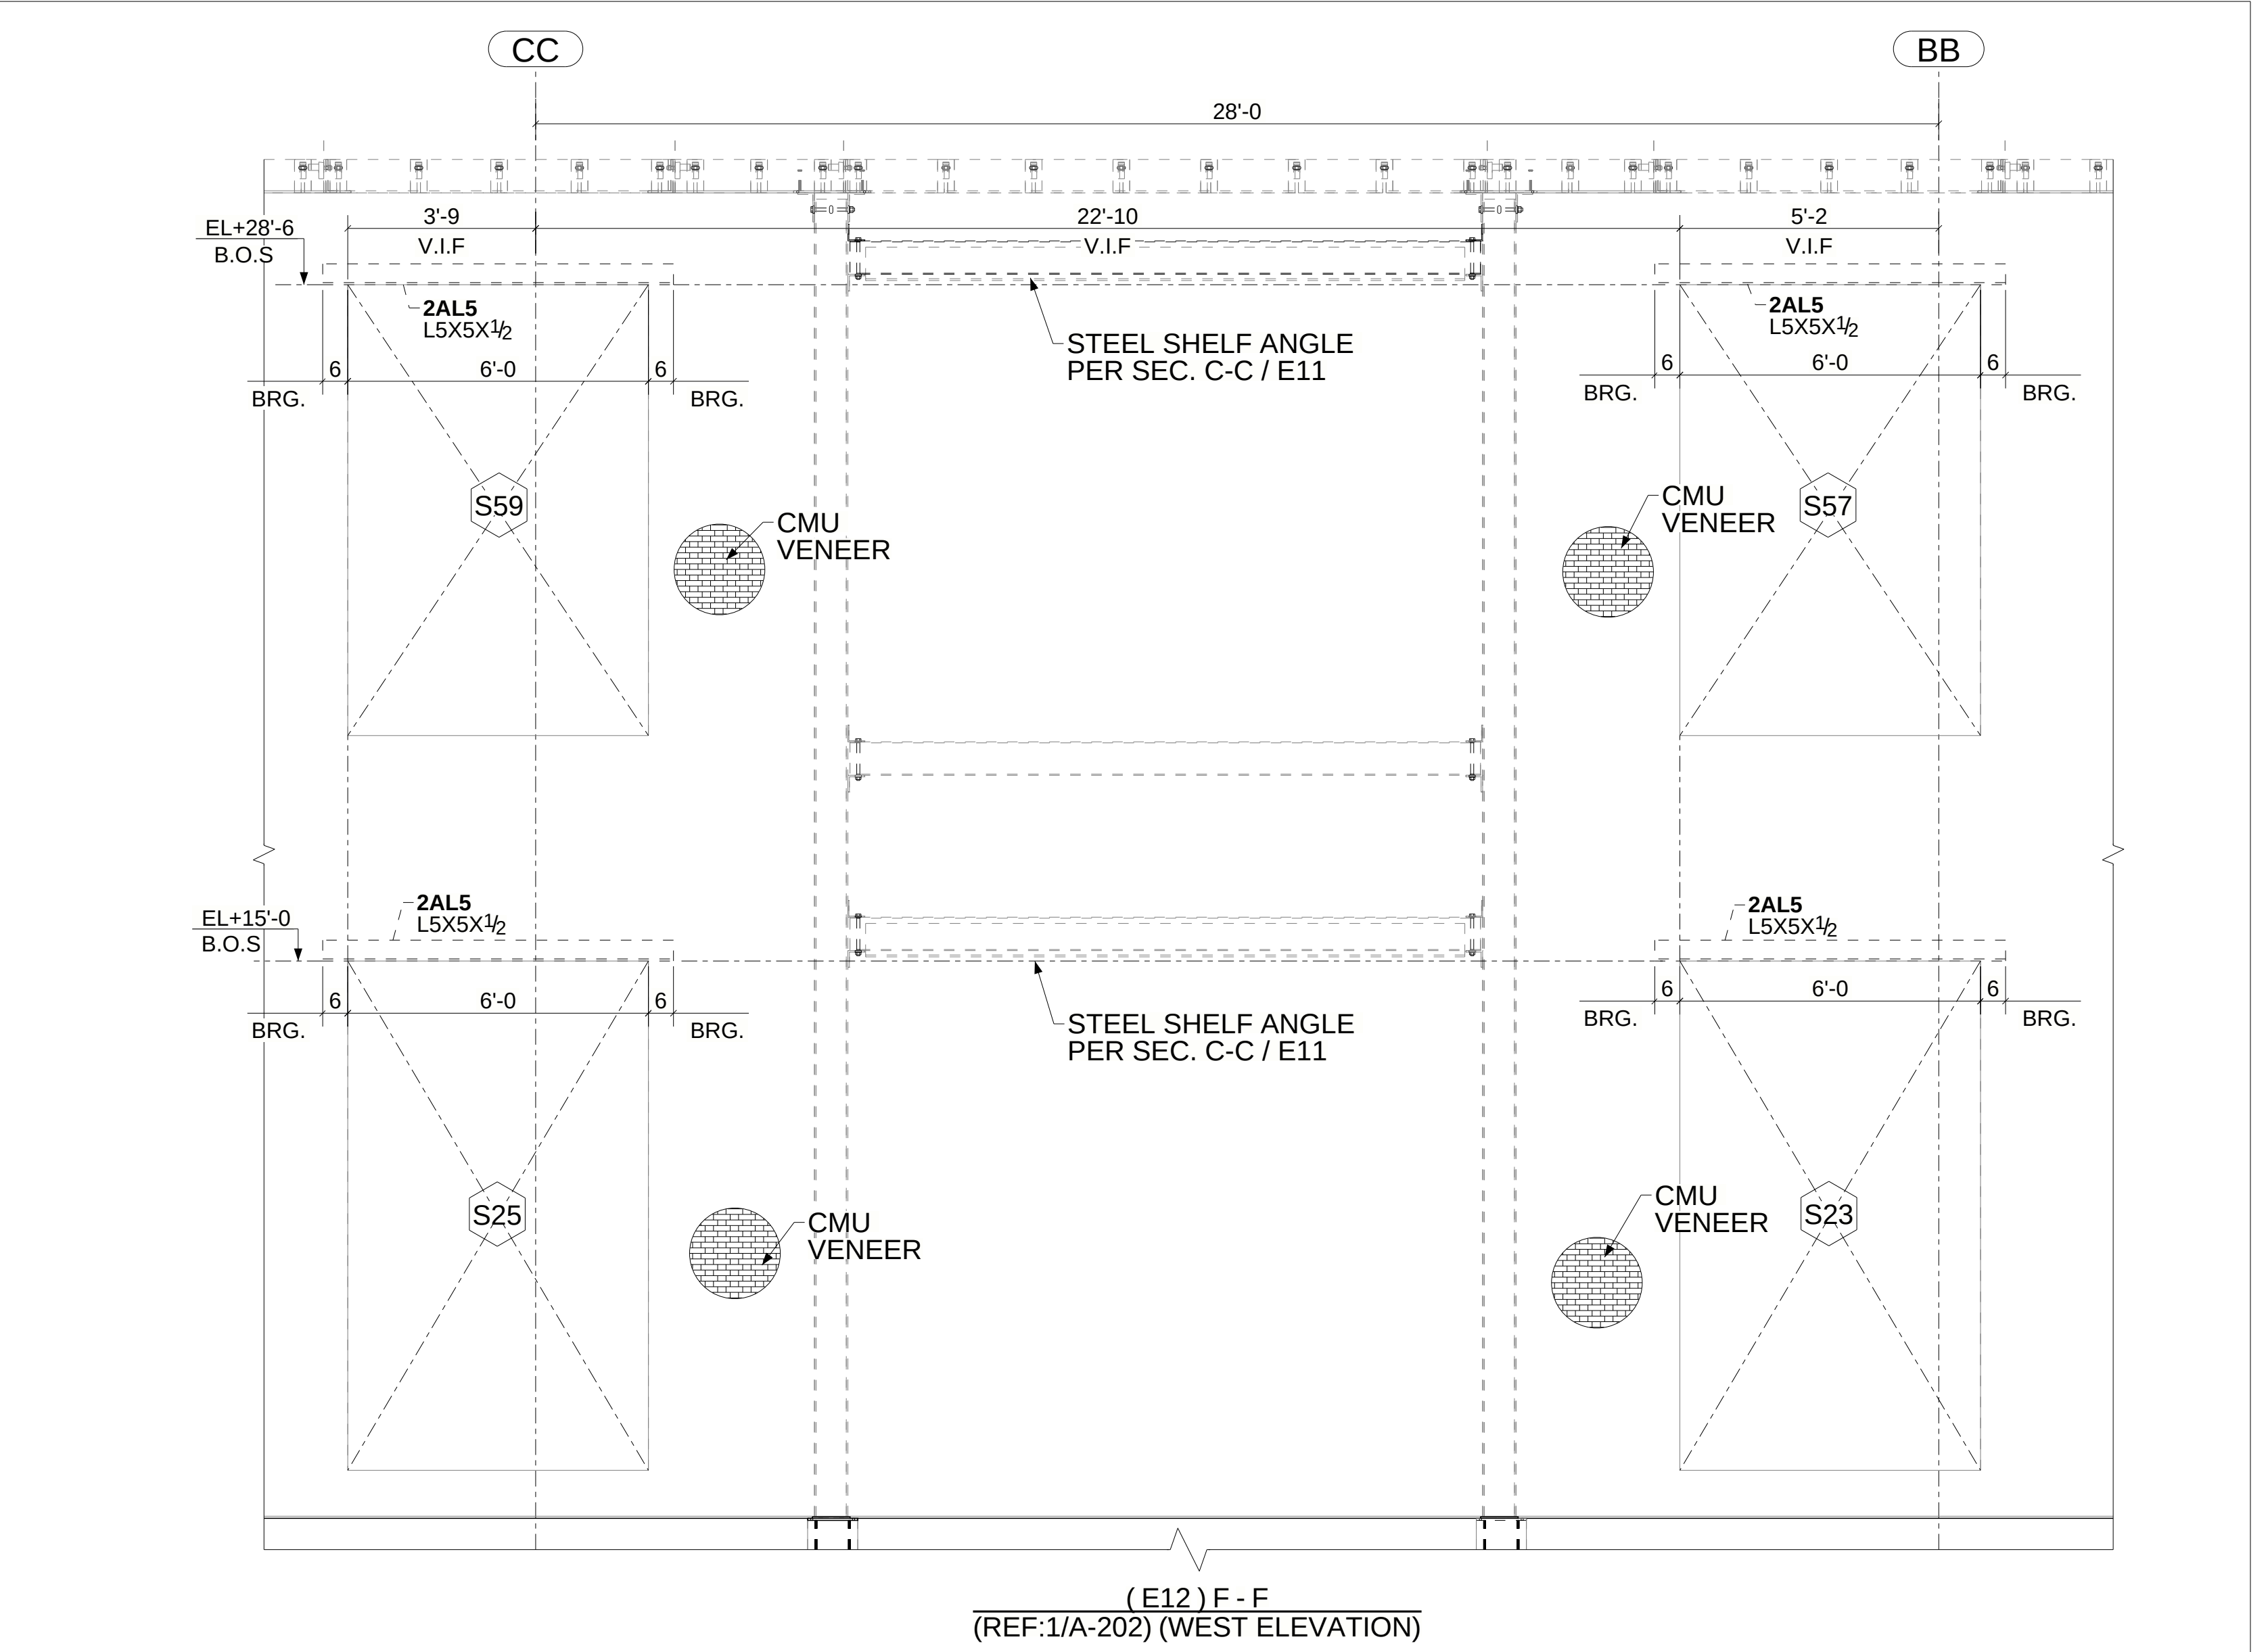


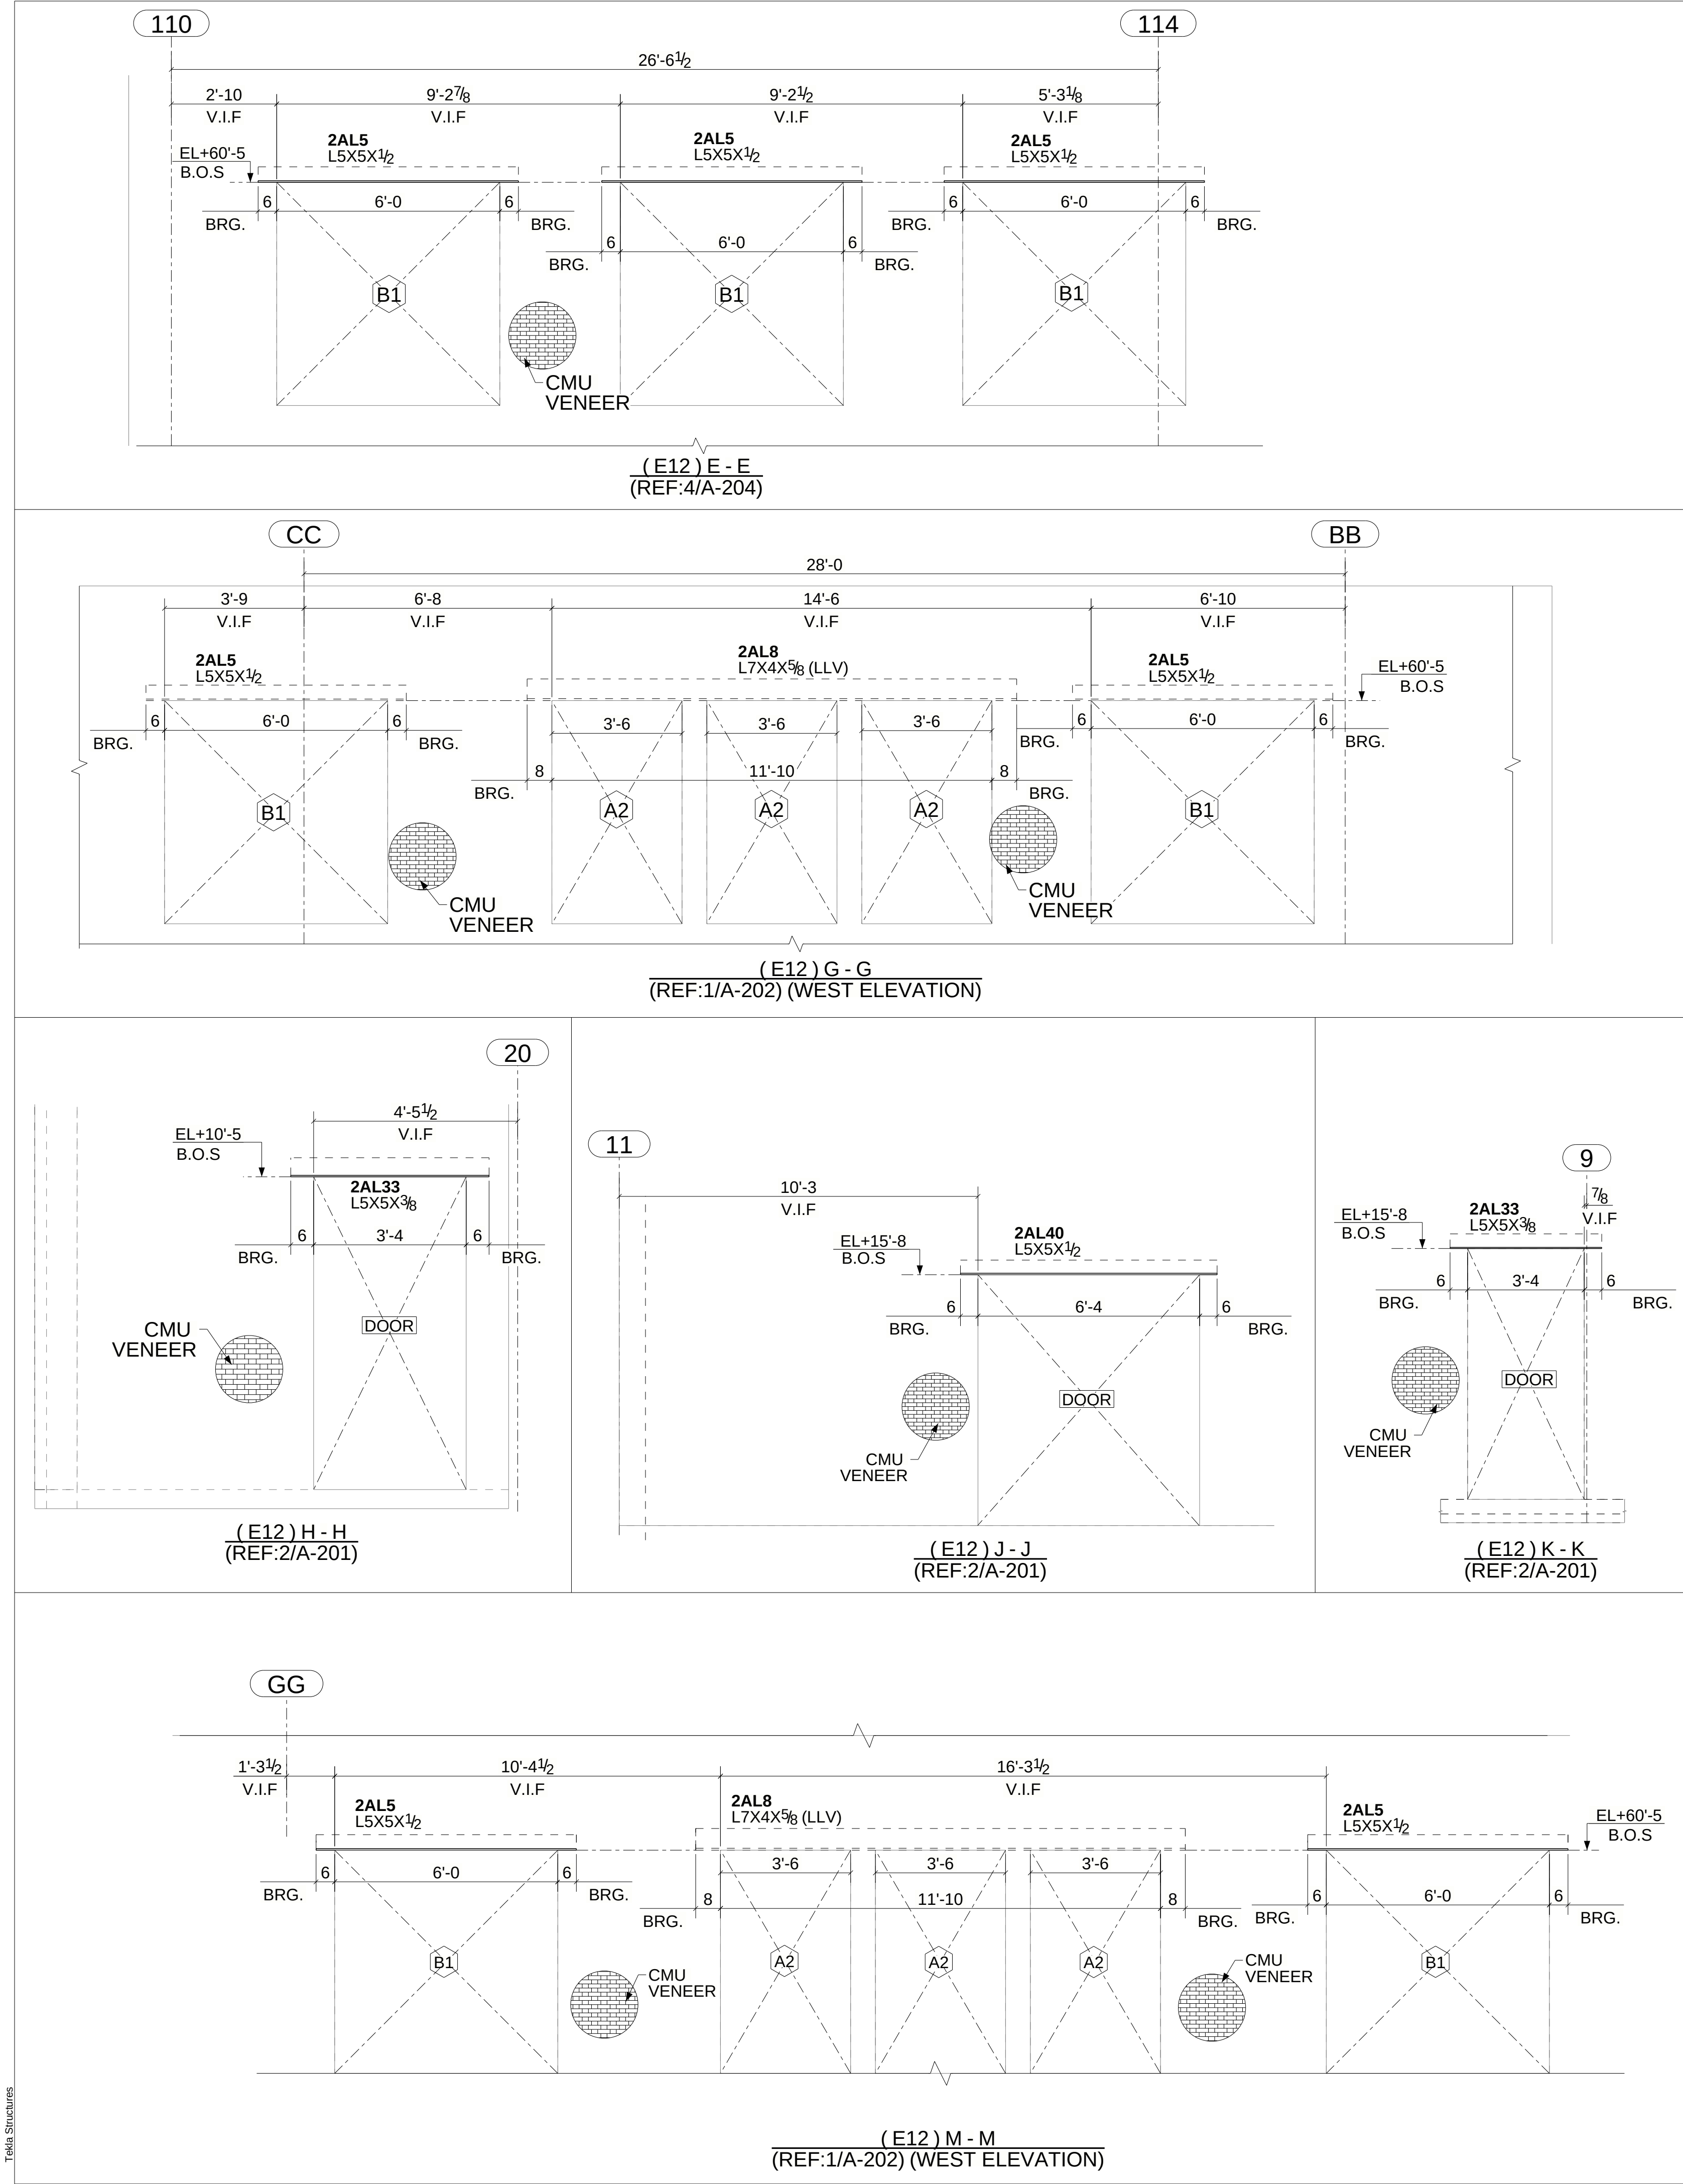

LEGEND:

- WINDOW / STORE FRONT TYPE
- BRG - BEARING
- B.O.S - BOTTOM OF STEEL
- V.I.F - VERIFY IN FIELD

GENERAL NOTE:

1.U.N.O ALL WINDOW LOCATIONS NOTED PER ELEVATIONS ARE TO BE FIELD VERIFIED WITH STORE FRONT OR WINDOW LOCATION DRAWINGS AS THESE ARE MEASURED PER ARCH REFERENCE.

1	06/26/2025	Revised As Noted
0	04/18/2025	For Construction
A	10/16/2024	For Approval
REV.	DATE	DESCRIPTION

CONTRACT No.24050	DWG No. E13
-------------------	-------------

Building Envelope Systems

20 HIGH STREET
PLAINSVILLE, MA 02762
PHONE (508) 381-0429
www.teambes.com

PROJECT NAME
GSC JUNIPER RBP PHASE-II

LOCATION
PARKWAY EVERETT, MA

CONTRACTOR
BUILDING ENVELOPE SYSTEMS

DWG TITLE
LOOSE LINTEL FRAMING PLAN (ZONE-2)

DRAWN BY DRK
CHECKED BY HSR
DATE DRAWN 06/26/2025
PLOT DATE 06/26/2025
DGSTS No. --
REV. 1